


ПОЭТАЖНЫЙ ПЛАН
 по адресу: Проезд №604
наименование ул. (просп., бульв. и т.д.)
 домовл. (ед.) _____ ДЗМ _____
нужное подчеркнуть
 корпус 2 строение (сооружение) 1
нужное подчеркнуть
 квартал № _____ СВ АО г. Москвы

1 Северо-Западное
 территориальное бюро
 технической инвентаризации
 города Москвы


1 ЭТАЖ

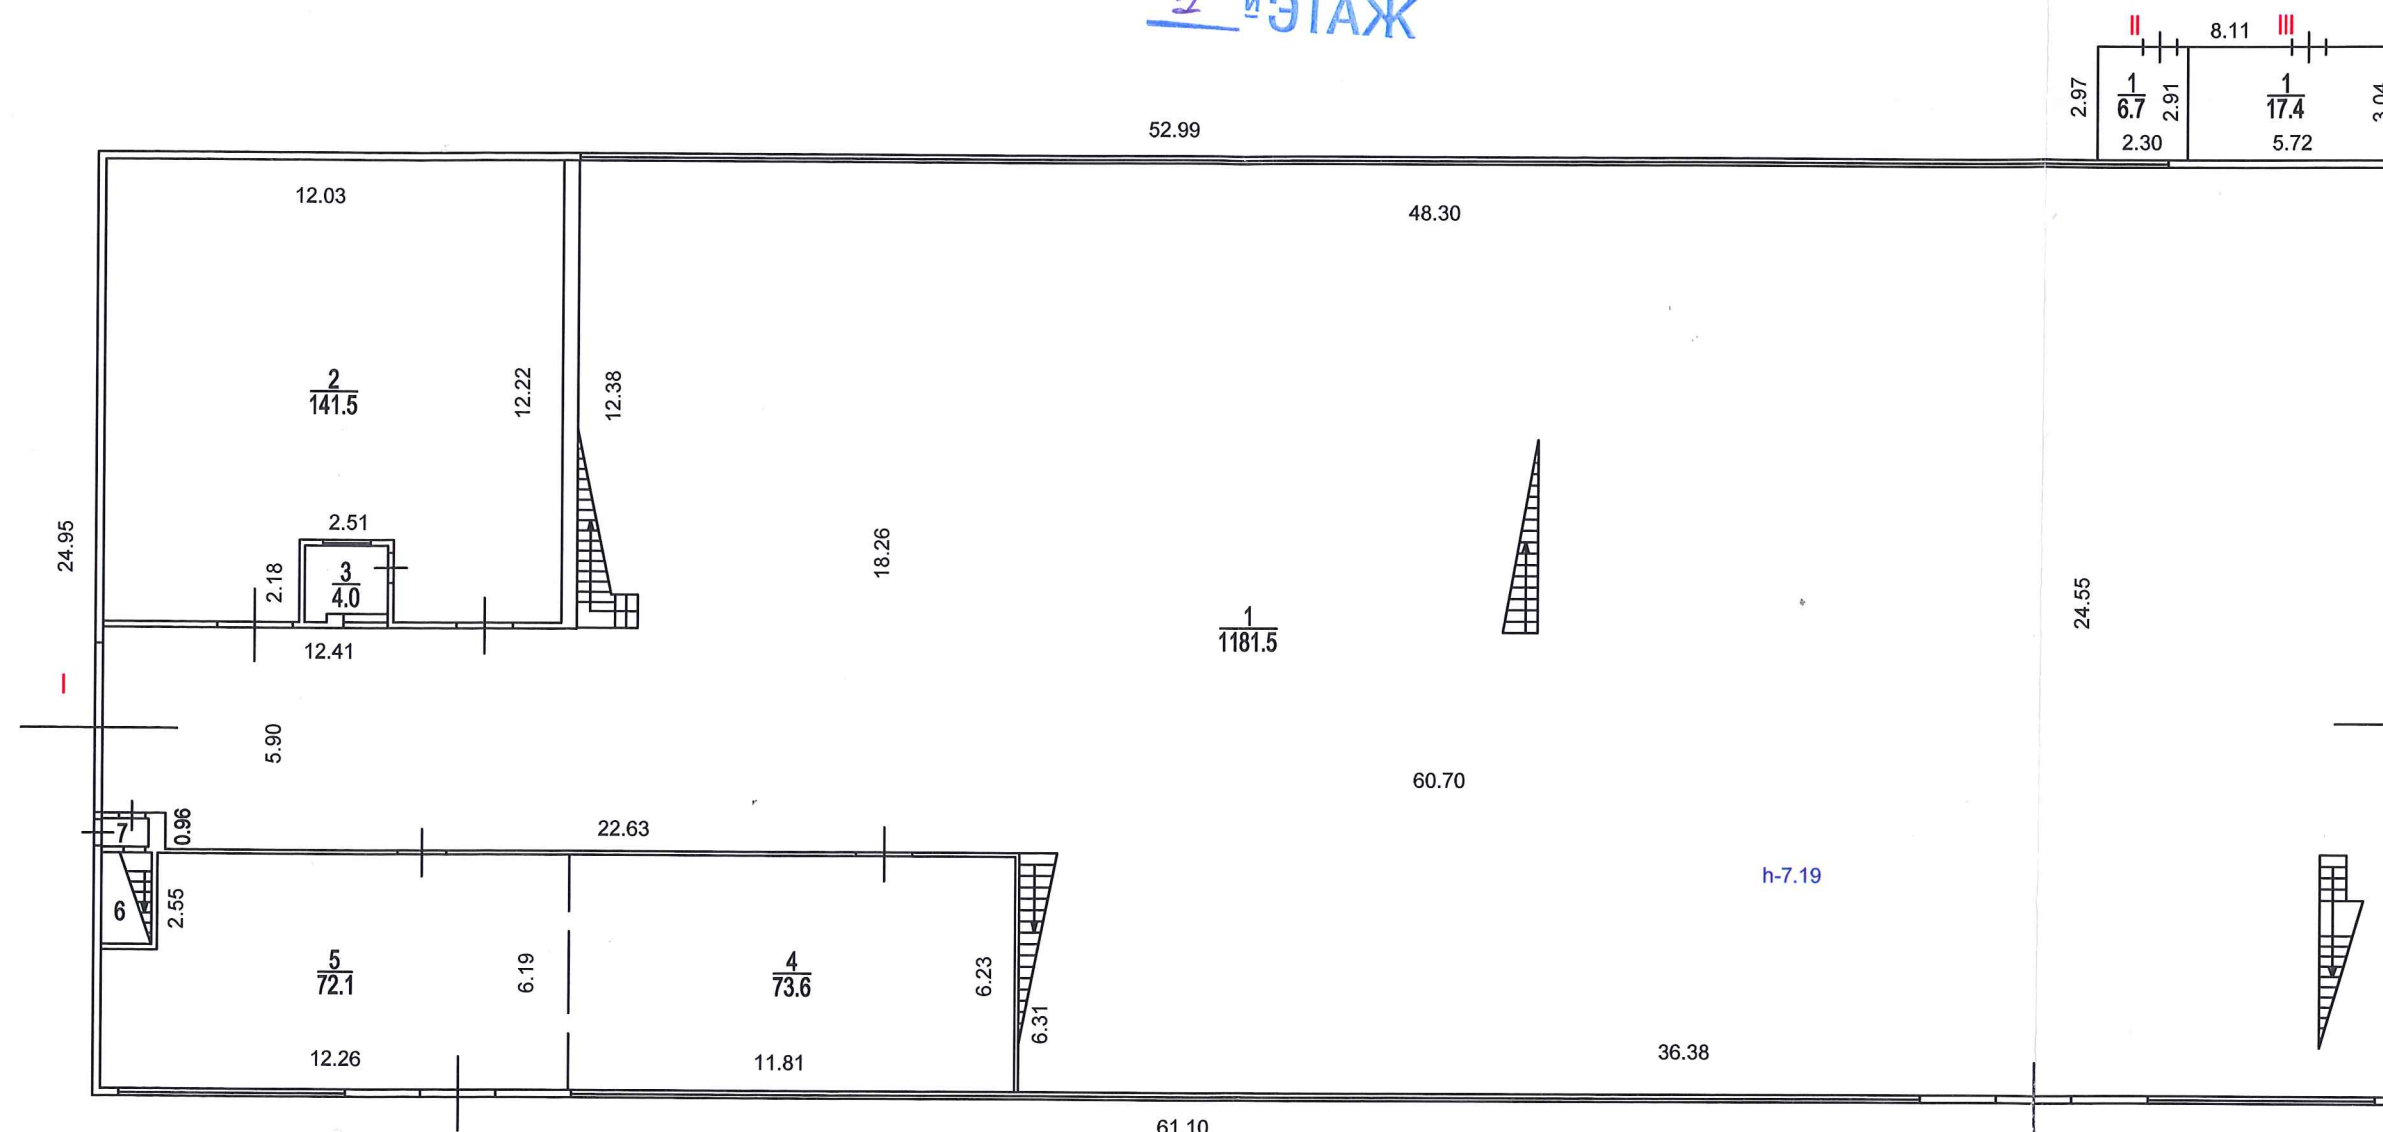

2.97	II	8.11	III	3.04
1	6.7	1	17.4	
2.30	2.91	5.72		

АНТРЕСОЛЬ 1 ЭТАЖ

① Северо-Западное
территориальное бюро
технической инвентаризации
города Москвы

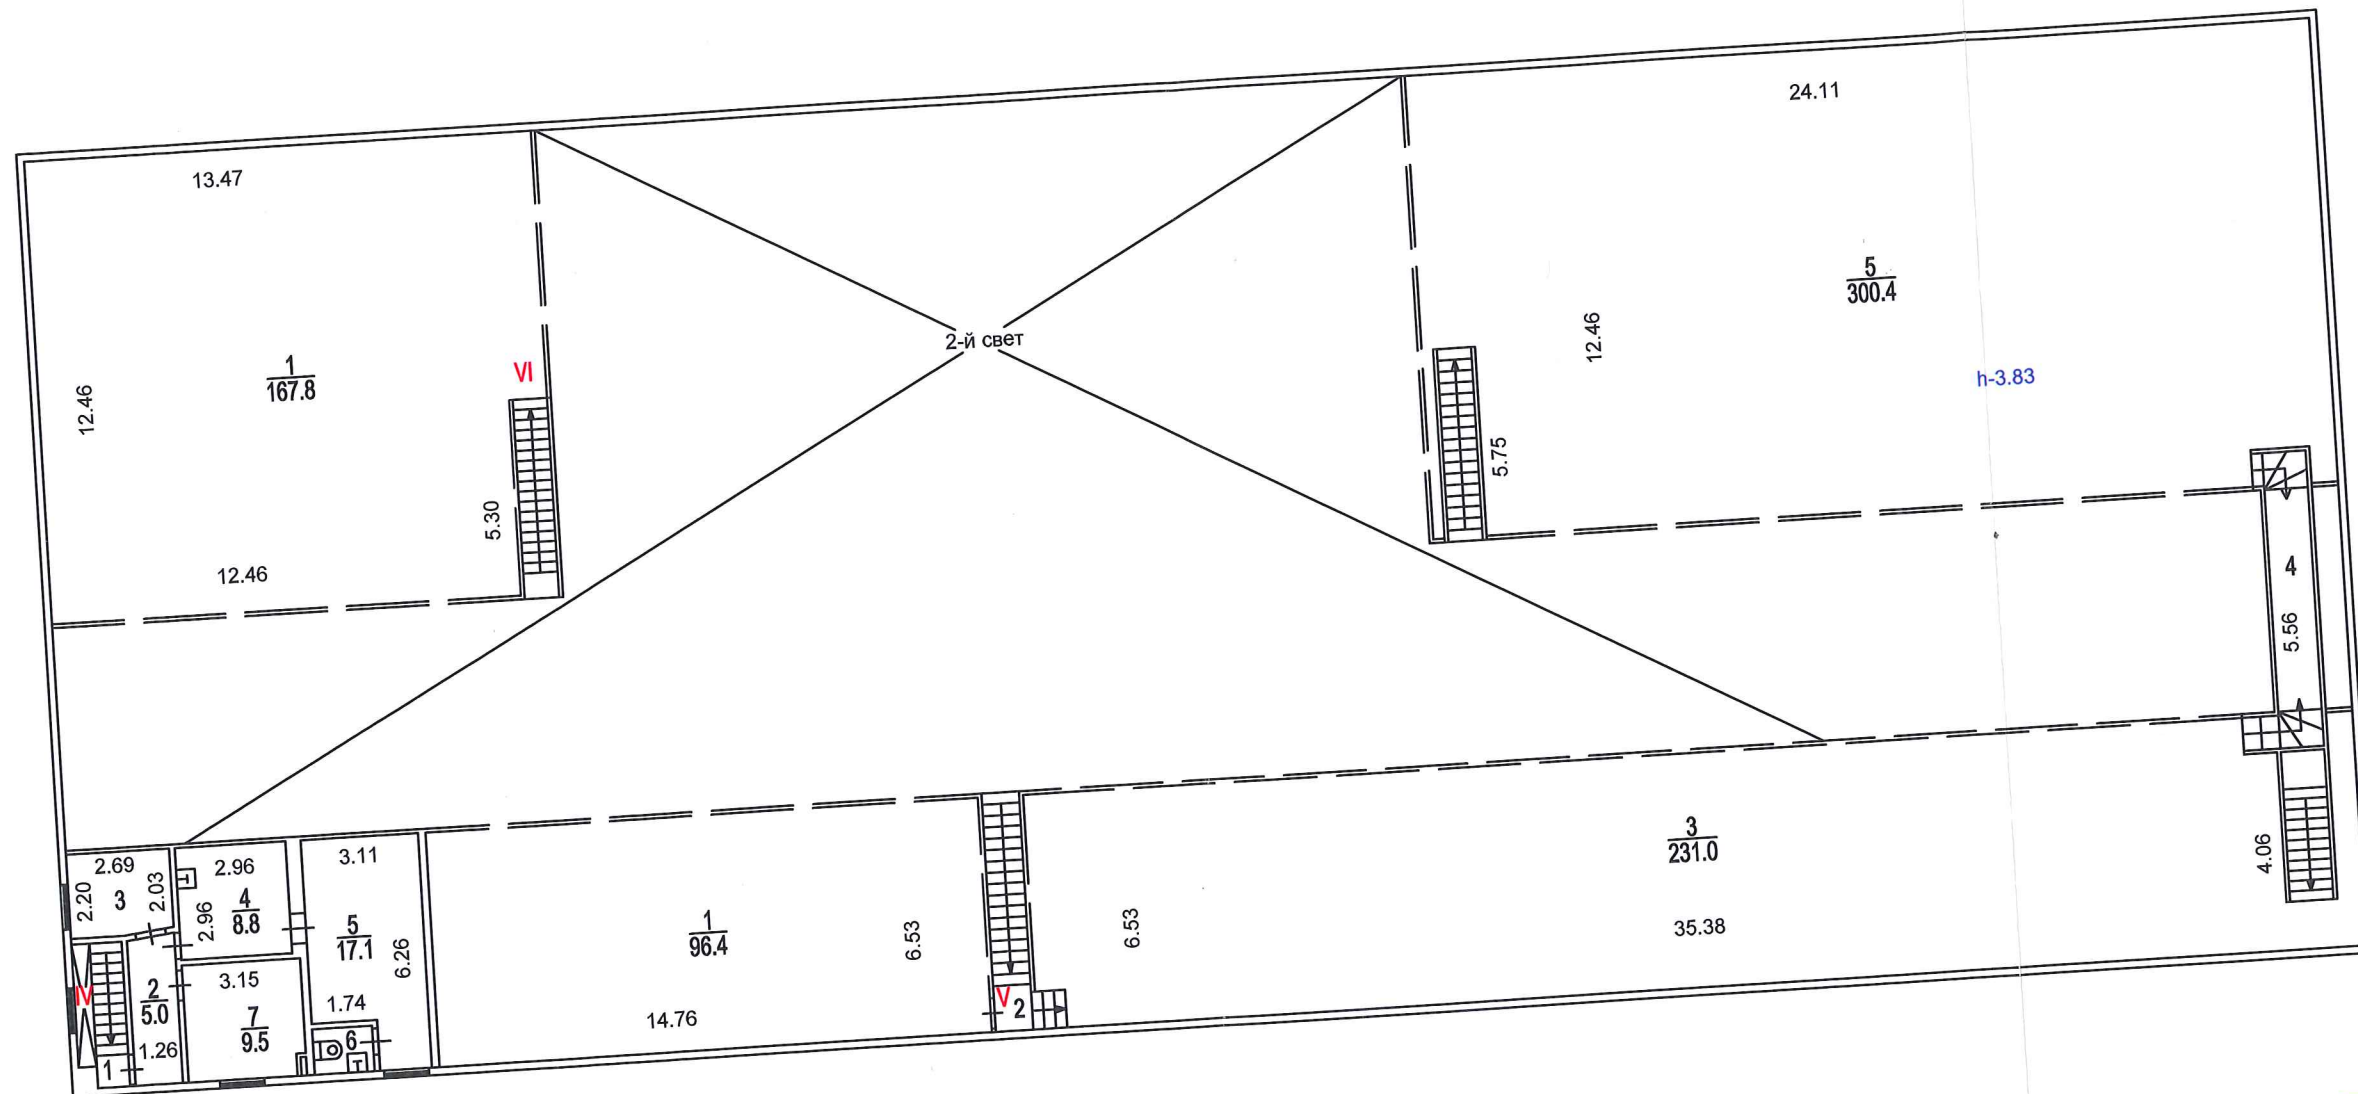

Руководитель группы
Северо-Западного ТБТИ
Кулаков Е. В.

12 80 318882

Постажный план составлен по состоянию на
« 28 » 10 200 9 г.
Масштаб: 1:100
Проверил: [Signature]
« 30 » 12 200 11 г.



Зам. начальника
СЗ ТБТИ
Гусева Т.В.

Северо-Осетинский государственный технический университет
Институт защиты труда
Министерство образования и науки Российской Федерации

Северо-Осетинский государственный технический университет
Институт защиты труда
Министерство образования и науки Российской Федерации