


КОНЦЕПЦИЯ ГЕНЕРАЛЬНОГО ПЛАНА
 посадка здания склада на земельный участок с кадастровым номером: 34:34:020032:36 по объекту: «Индустриальный парк Шайба»

СИТУАЦИОННАЯ СХЕМА

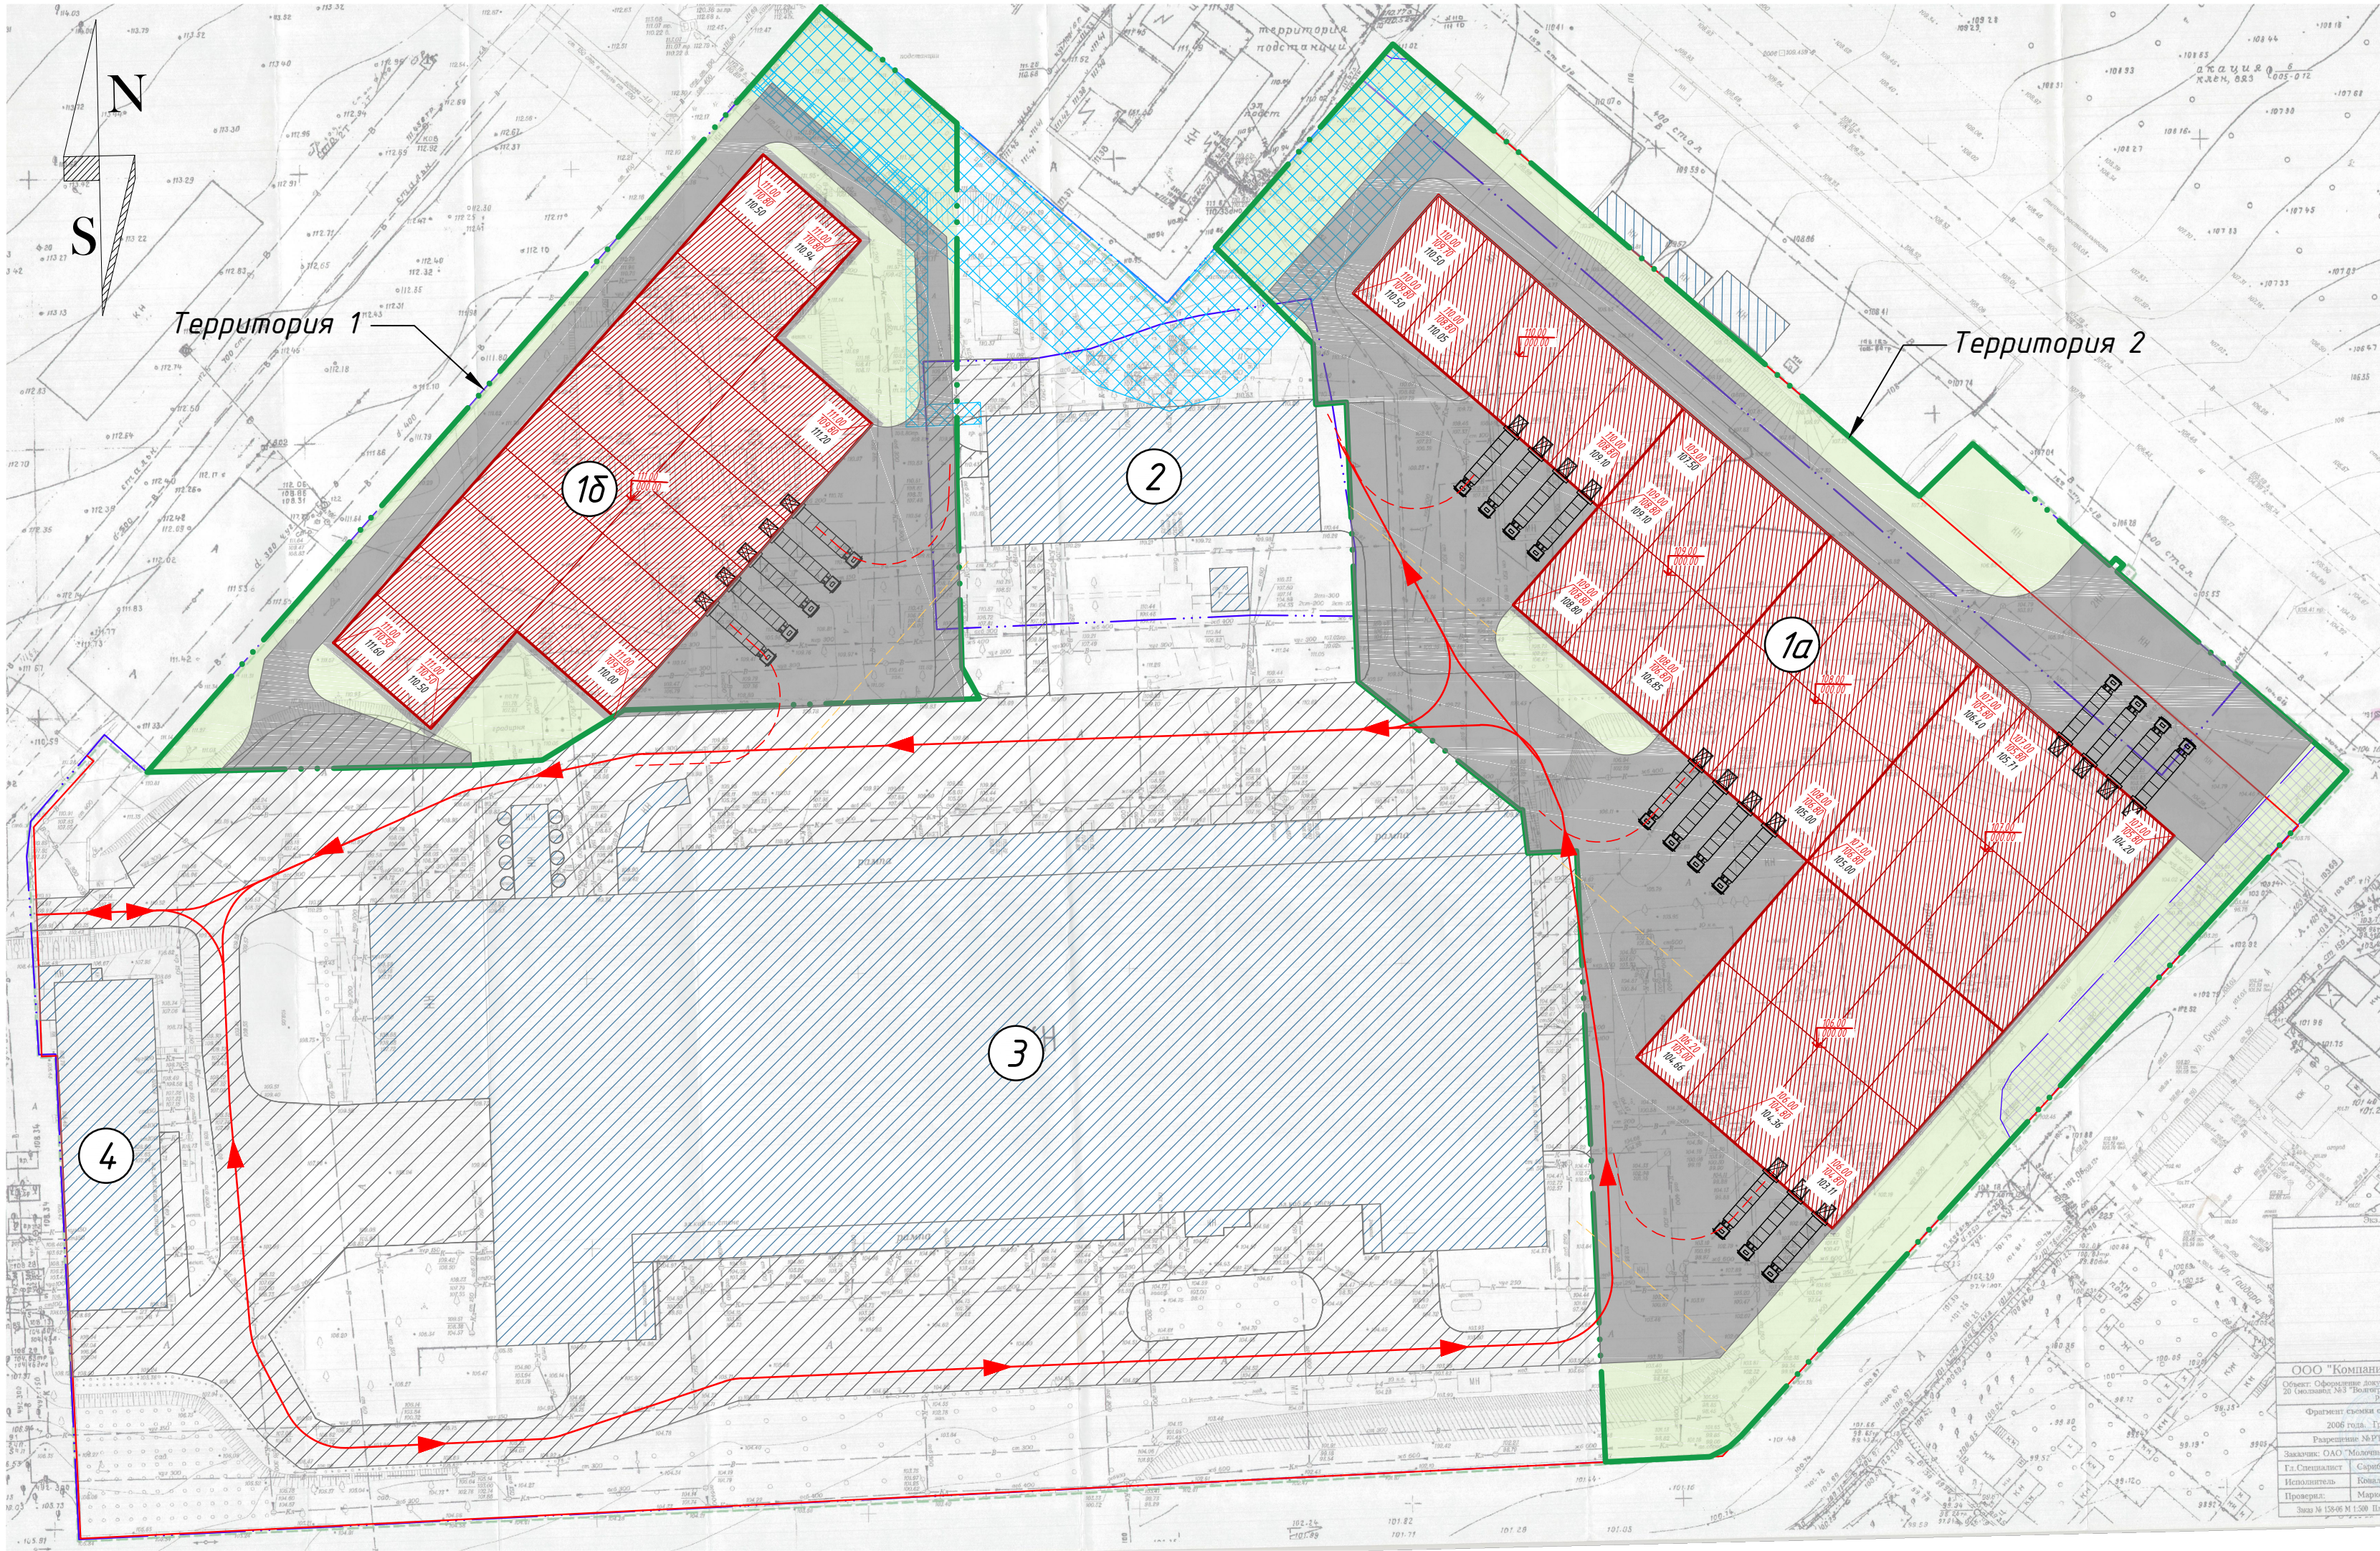


УСЛОВНЫЕ ОБОЗНАЧЕНИЯ

 Условная граница проектирования

ЭКСПЛИКАЦИЯ ЗДАНИЙ И СООРУЖЕНИЙ

Н/п	Наименование
1а	Склад проектируемый №1
1б	Склад проектируемый №2
2	Котельная (сущ.)
3	Главный корпус (сущ.)
4	АБК

УСЛОВНЫЕ ОБОЗНАЧЕНИЯ

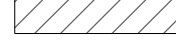-  Граница благоустройства
-  Граница зем.участка
-  Здание проектируемое
-  Здания и сооружения существующие
-  Твердые покрытия проектируемые
-  Твердые покрытия существующие
-  Озеленение
-  Движение транспорта по территории
-  Твердые покрытия существующие
-  Зона публичного сервитута

ОСНОВНЫЕ ПОКАЗАТЕЛИ ГЕНЕРАЛЬНОГО ПЛАНА
Территория 1

Наименование показателей	Ед. изм	Кол-во	%
Общая площадь двух смежных зем.участков	м2	80 792.46	
Площадь благоустройства	м2	11 154.78	100
Площадь застройки	м2	4 608	42
Площадь твердых покрытий	м2	4165.70*	37
Площадь озеленения	м2	2 381.08*	21

ОСНОВНЫЕ ПОКАЗАТЕЛИ ГЕНЕРАЛЬНОГО ПЛАНА
Территория 2

Наименование показателей	Ед. изм	Кол-во	%
Общая площадь двух смежных зем.участков	м2	80 792.46	
Площадь благоустройства	м2	23 688.16	100
Площадь застройки	м2	9 504	40
Площадь твердых покрытий	м2	9 636.13*	41
Площадь озеленения	м2	4 548.03*	19

Согласно ПЗЗ городского округа город-герой Волгоград
 ст.19,п.1,таб.2
 минимальное кол-во мест 20м/м на 100 работающих в
 двух смежных сменах...