


[illegible]

1. Производственно-складское здание (проект).
2. Непроницаемая выгребная яма.
—x—x— существующие границы участка.


Максимальное количество людей одновременного нахождения в здании = 28 человек:
в том числе:
1) Посетители – 20 человек,
2) Работники – 8 человек.
Всего: 28 человек.

№	Наименование.	Ед. изм.	Кол-во.
1	Этажность	эт.	1
2	Площадь земельного участка	кв. м.	2160,0
3	Площадь застройки	кв. м.	1298,7
4	Строительный объем	куб. м.	10400,0
5	Площадь здания в соответствии с Приказом № П/0393	кв. м.	1283,3
6	Общая площадь	кв. м.	1282,6


						2024 - 059			
						Объект: Производственно-складское здание по адресу: Ростовская область, Мясниковский район, 1-й км автодороги Ростов-на-Дону-Новошахтинск, уч. № 10/8.			
						Кад. № земельного участка: 61:25:0600401:4136. Заказчик: Агаджанян Т.А.			
Изм.	Кол.уч.	Лист	№ док.	Подпись.	Дата				
						Проект производственно-складского здания	Стадия	Лист	Листов
Архитектор	Гайдарян А.А.			2024			П		
Проверил	Гайдарян А.А.			2024					
						Схема генплана. Ситуационный план. Основные показатели.	И.П. Гайдарян А.А. с.Чалтырь.		

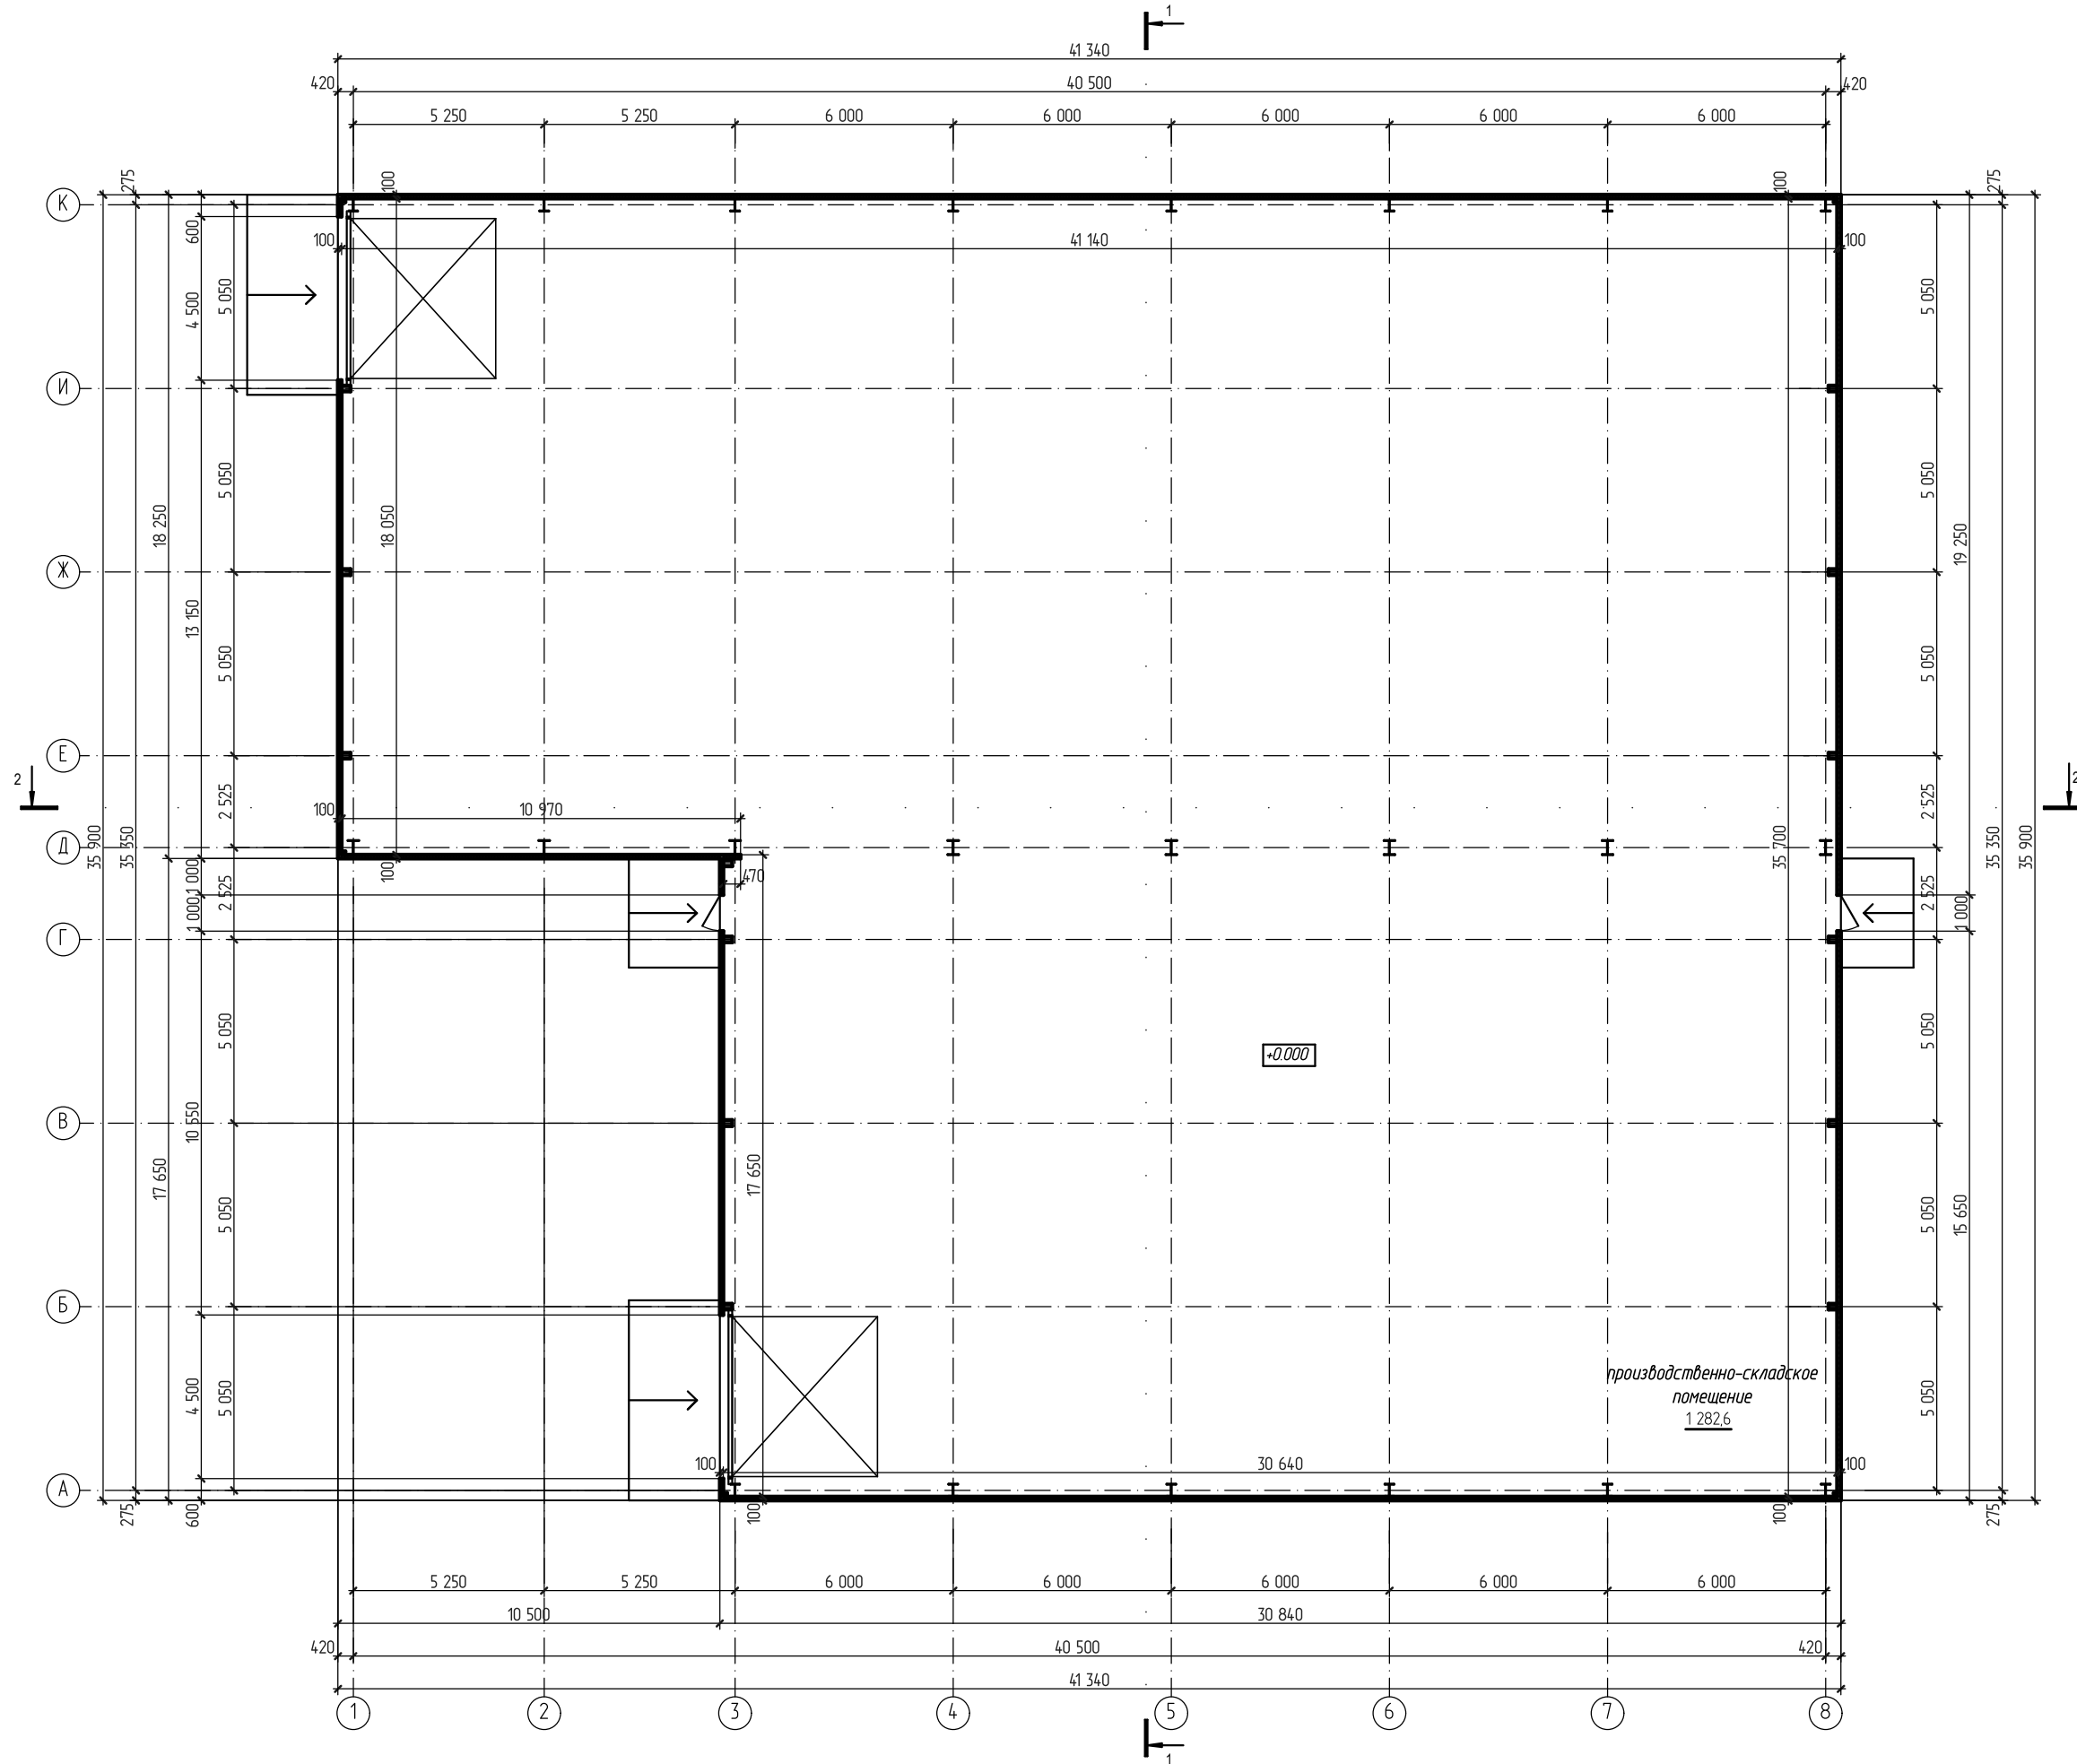

Изм.	Кол.уч.	Лист	№ док.	Подпись	Дата

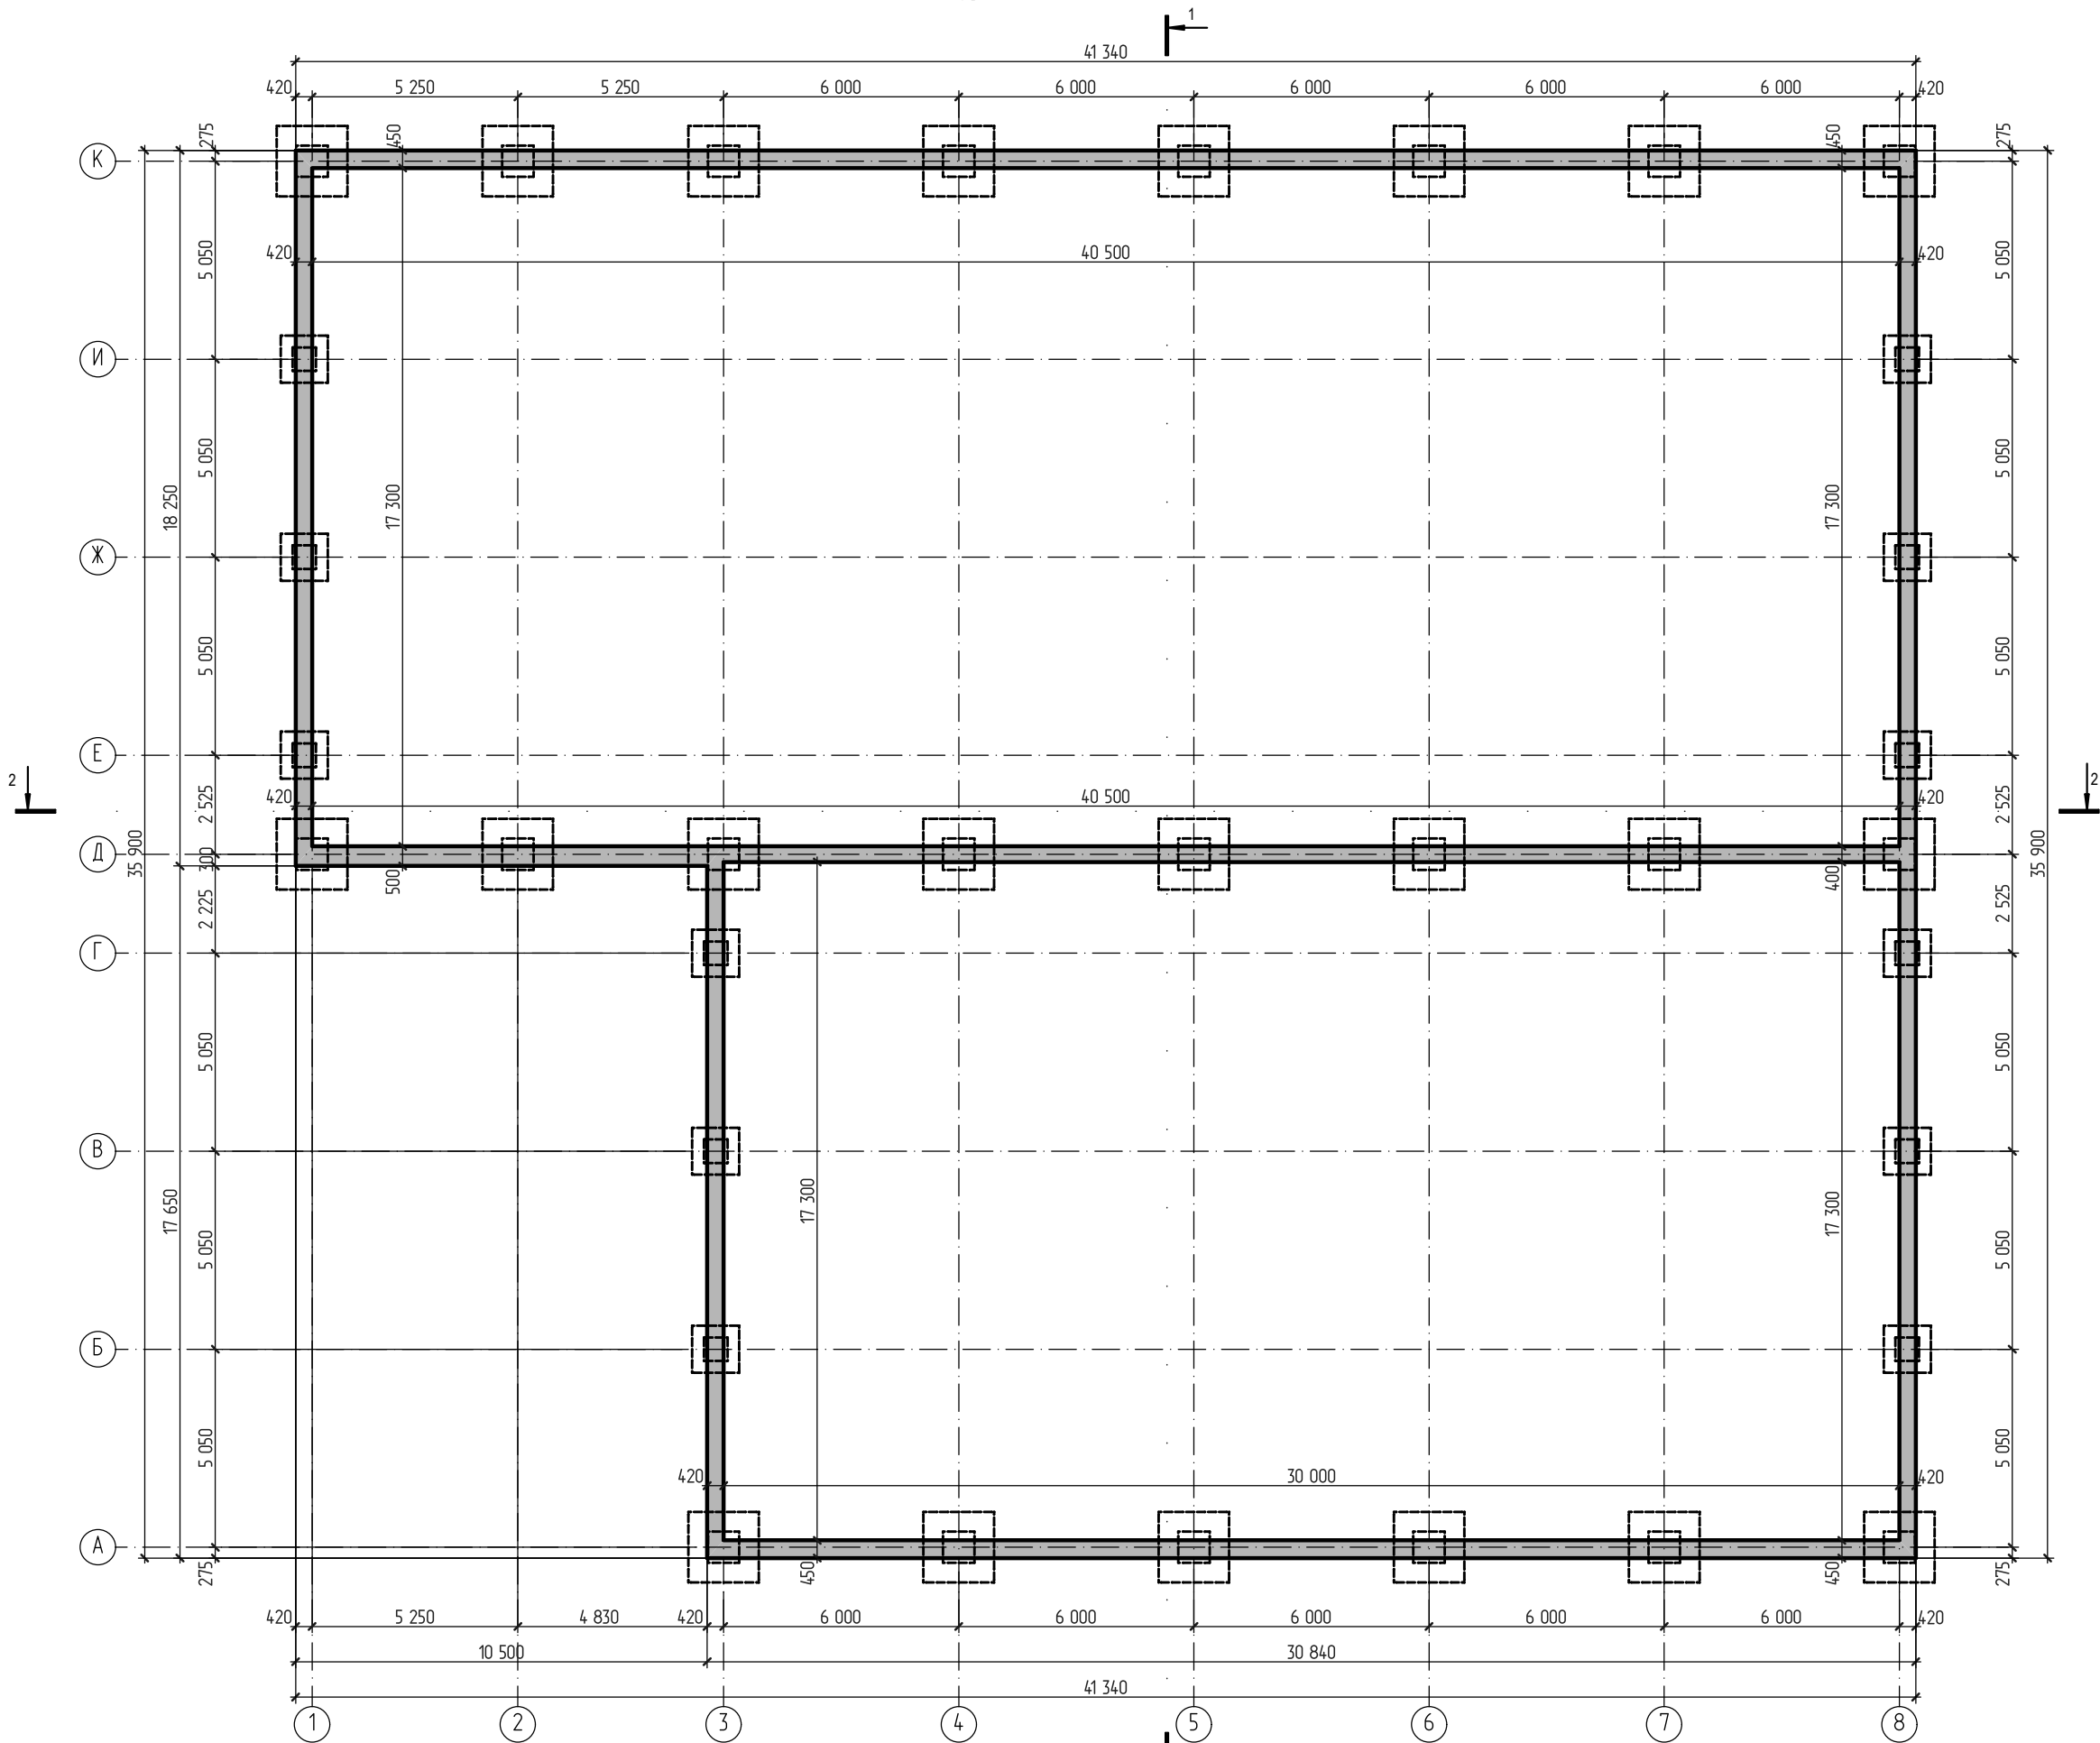


Изм.	Кол.уч.	Лист	№ док.	Подпись	Дата

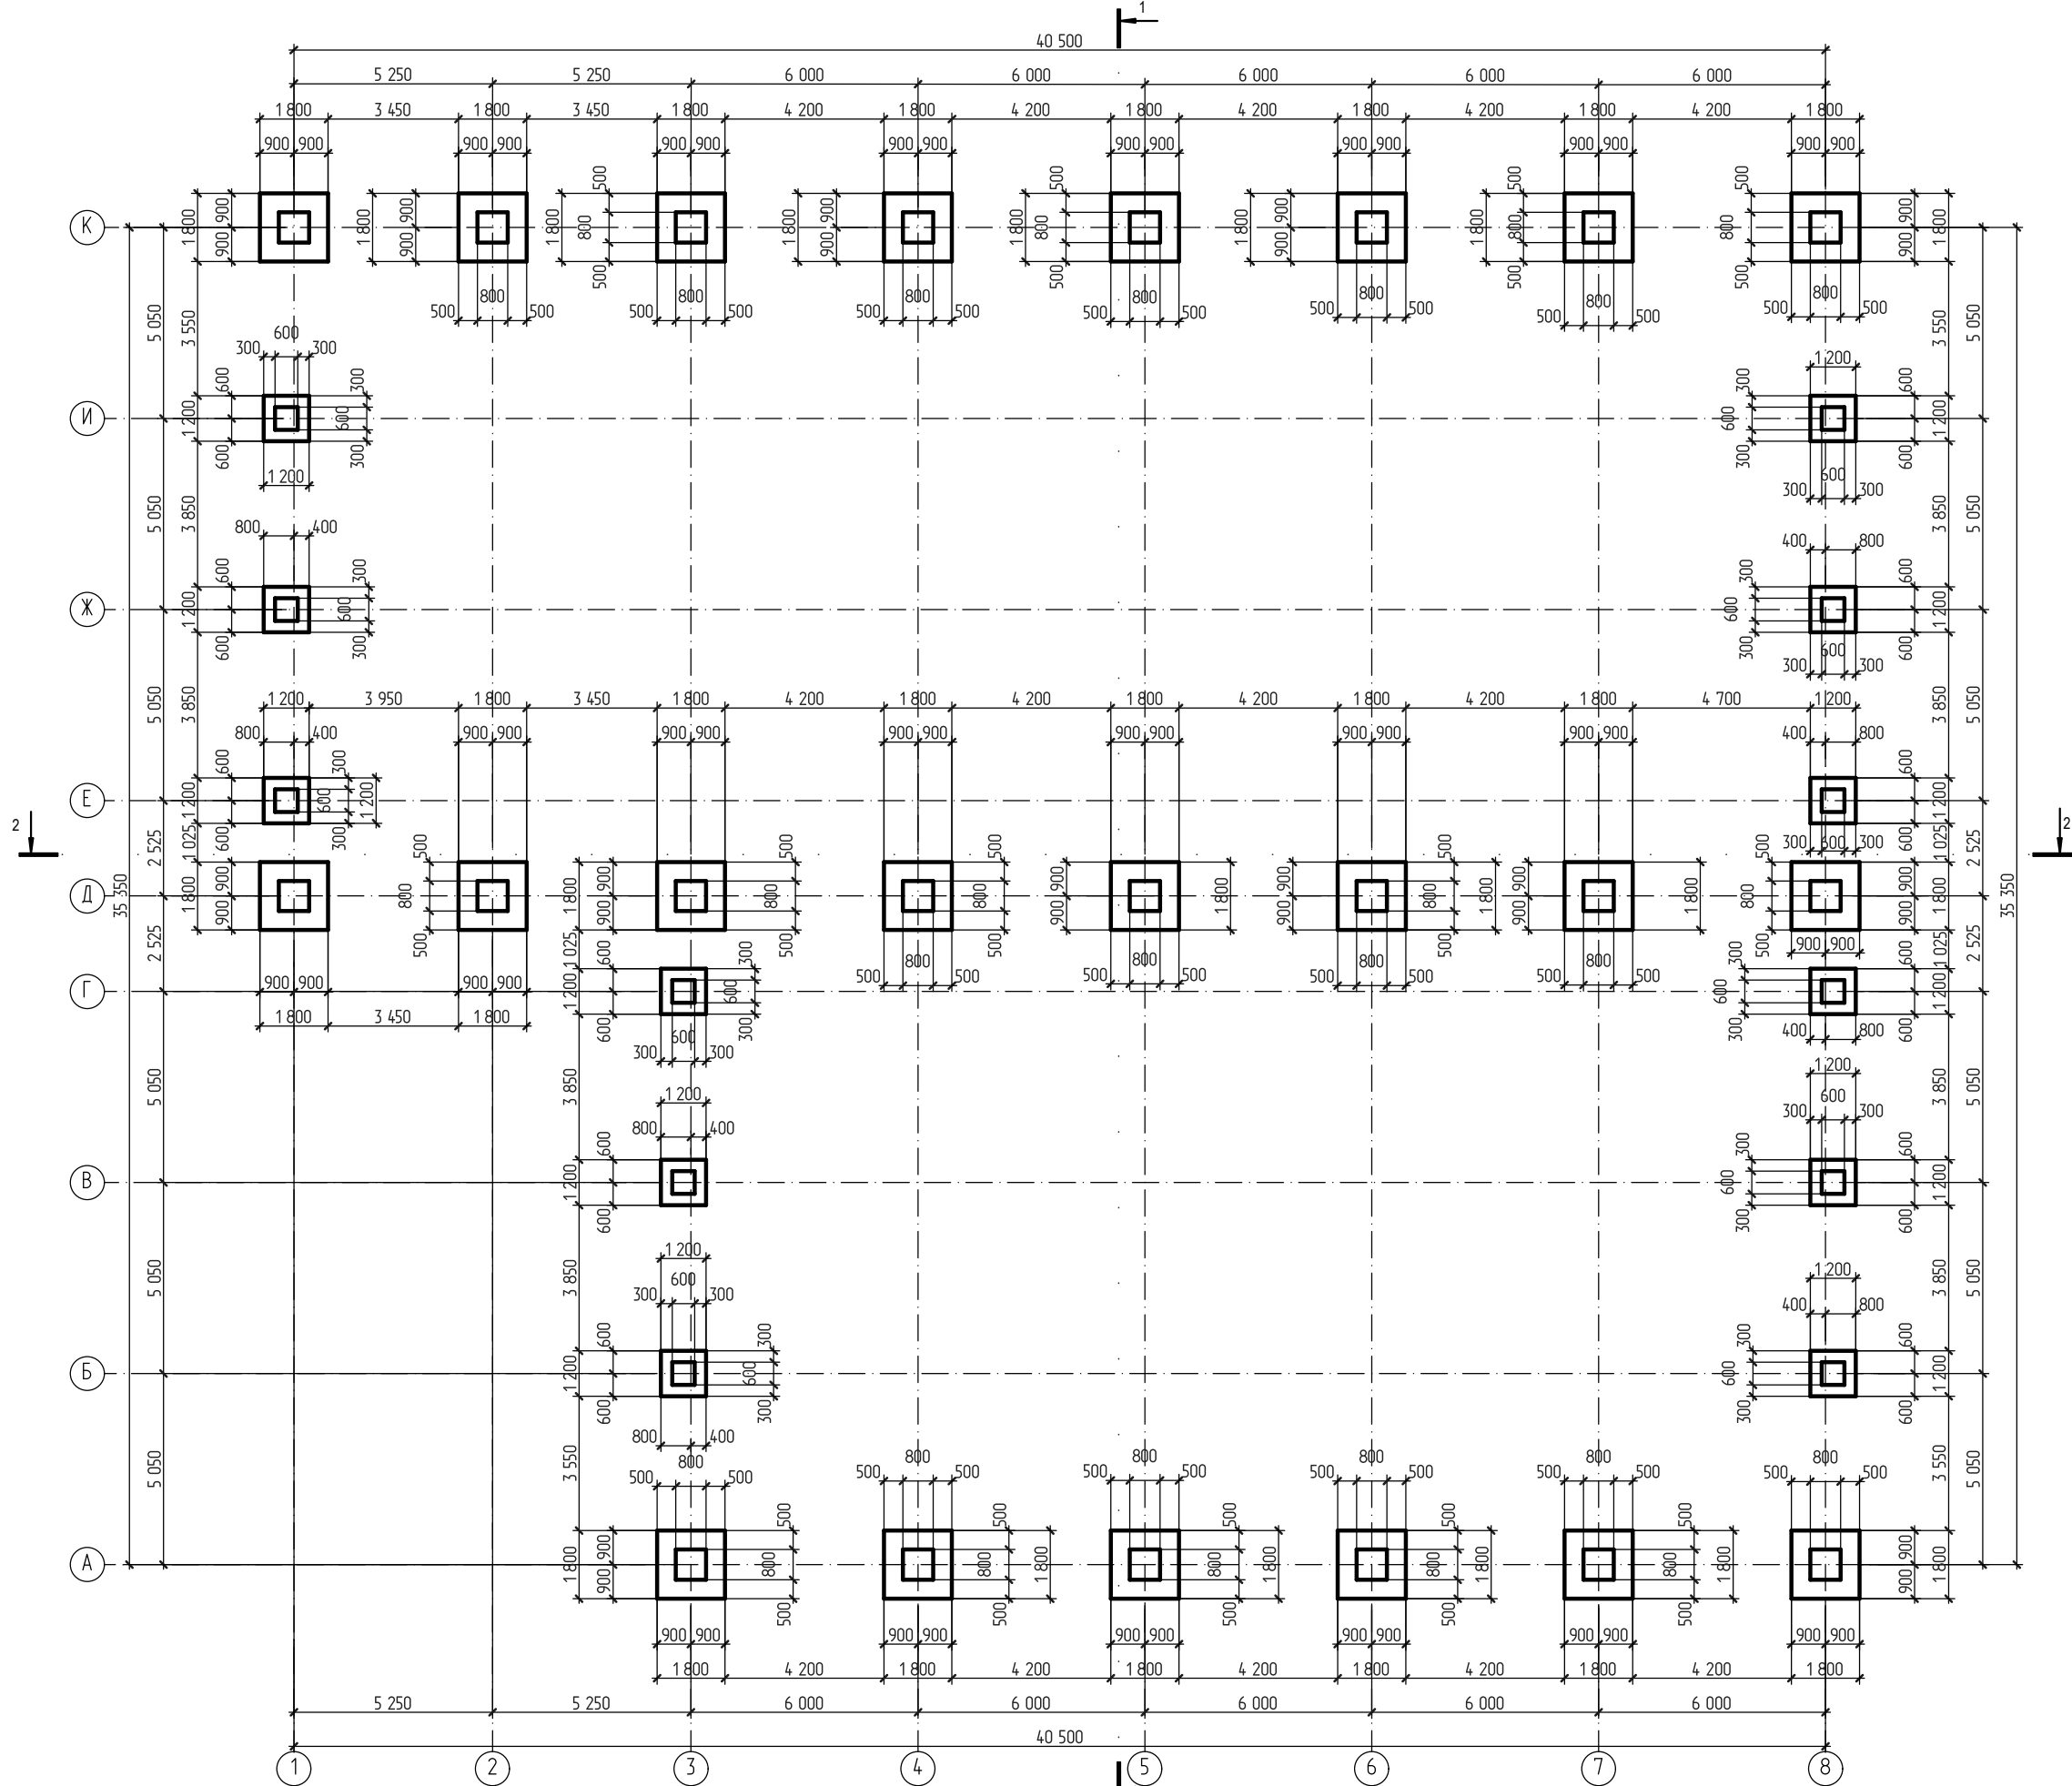

Изм.	Кол.уч.	Лист	№ док.	Подпись	Дата

План кровлі. М 1:200.

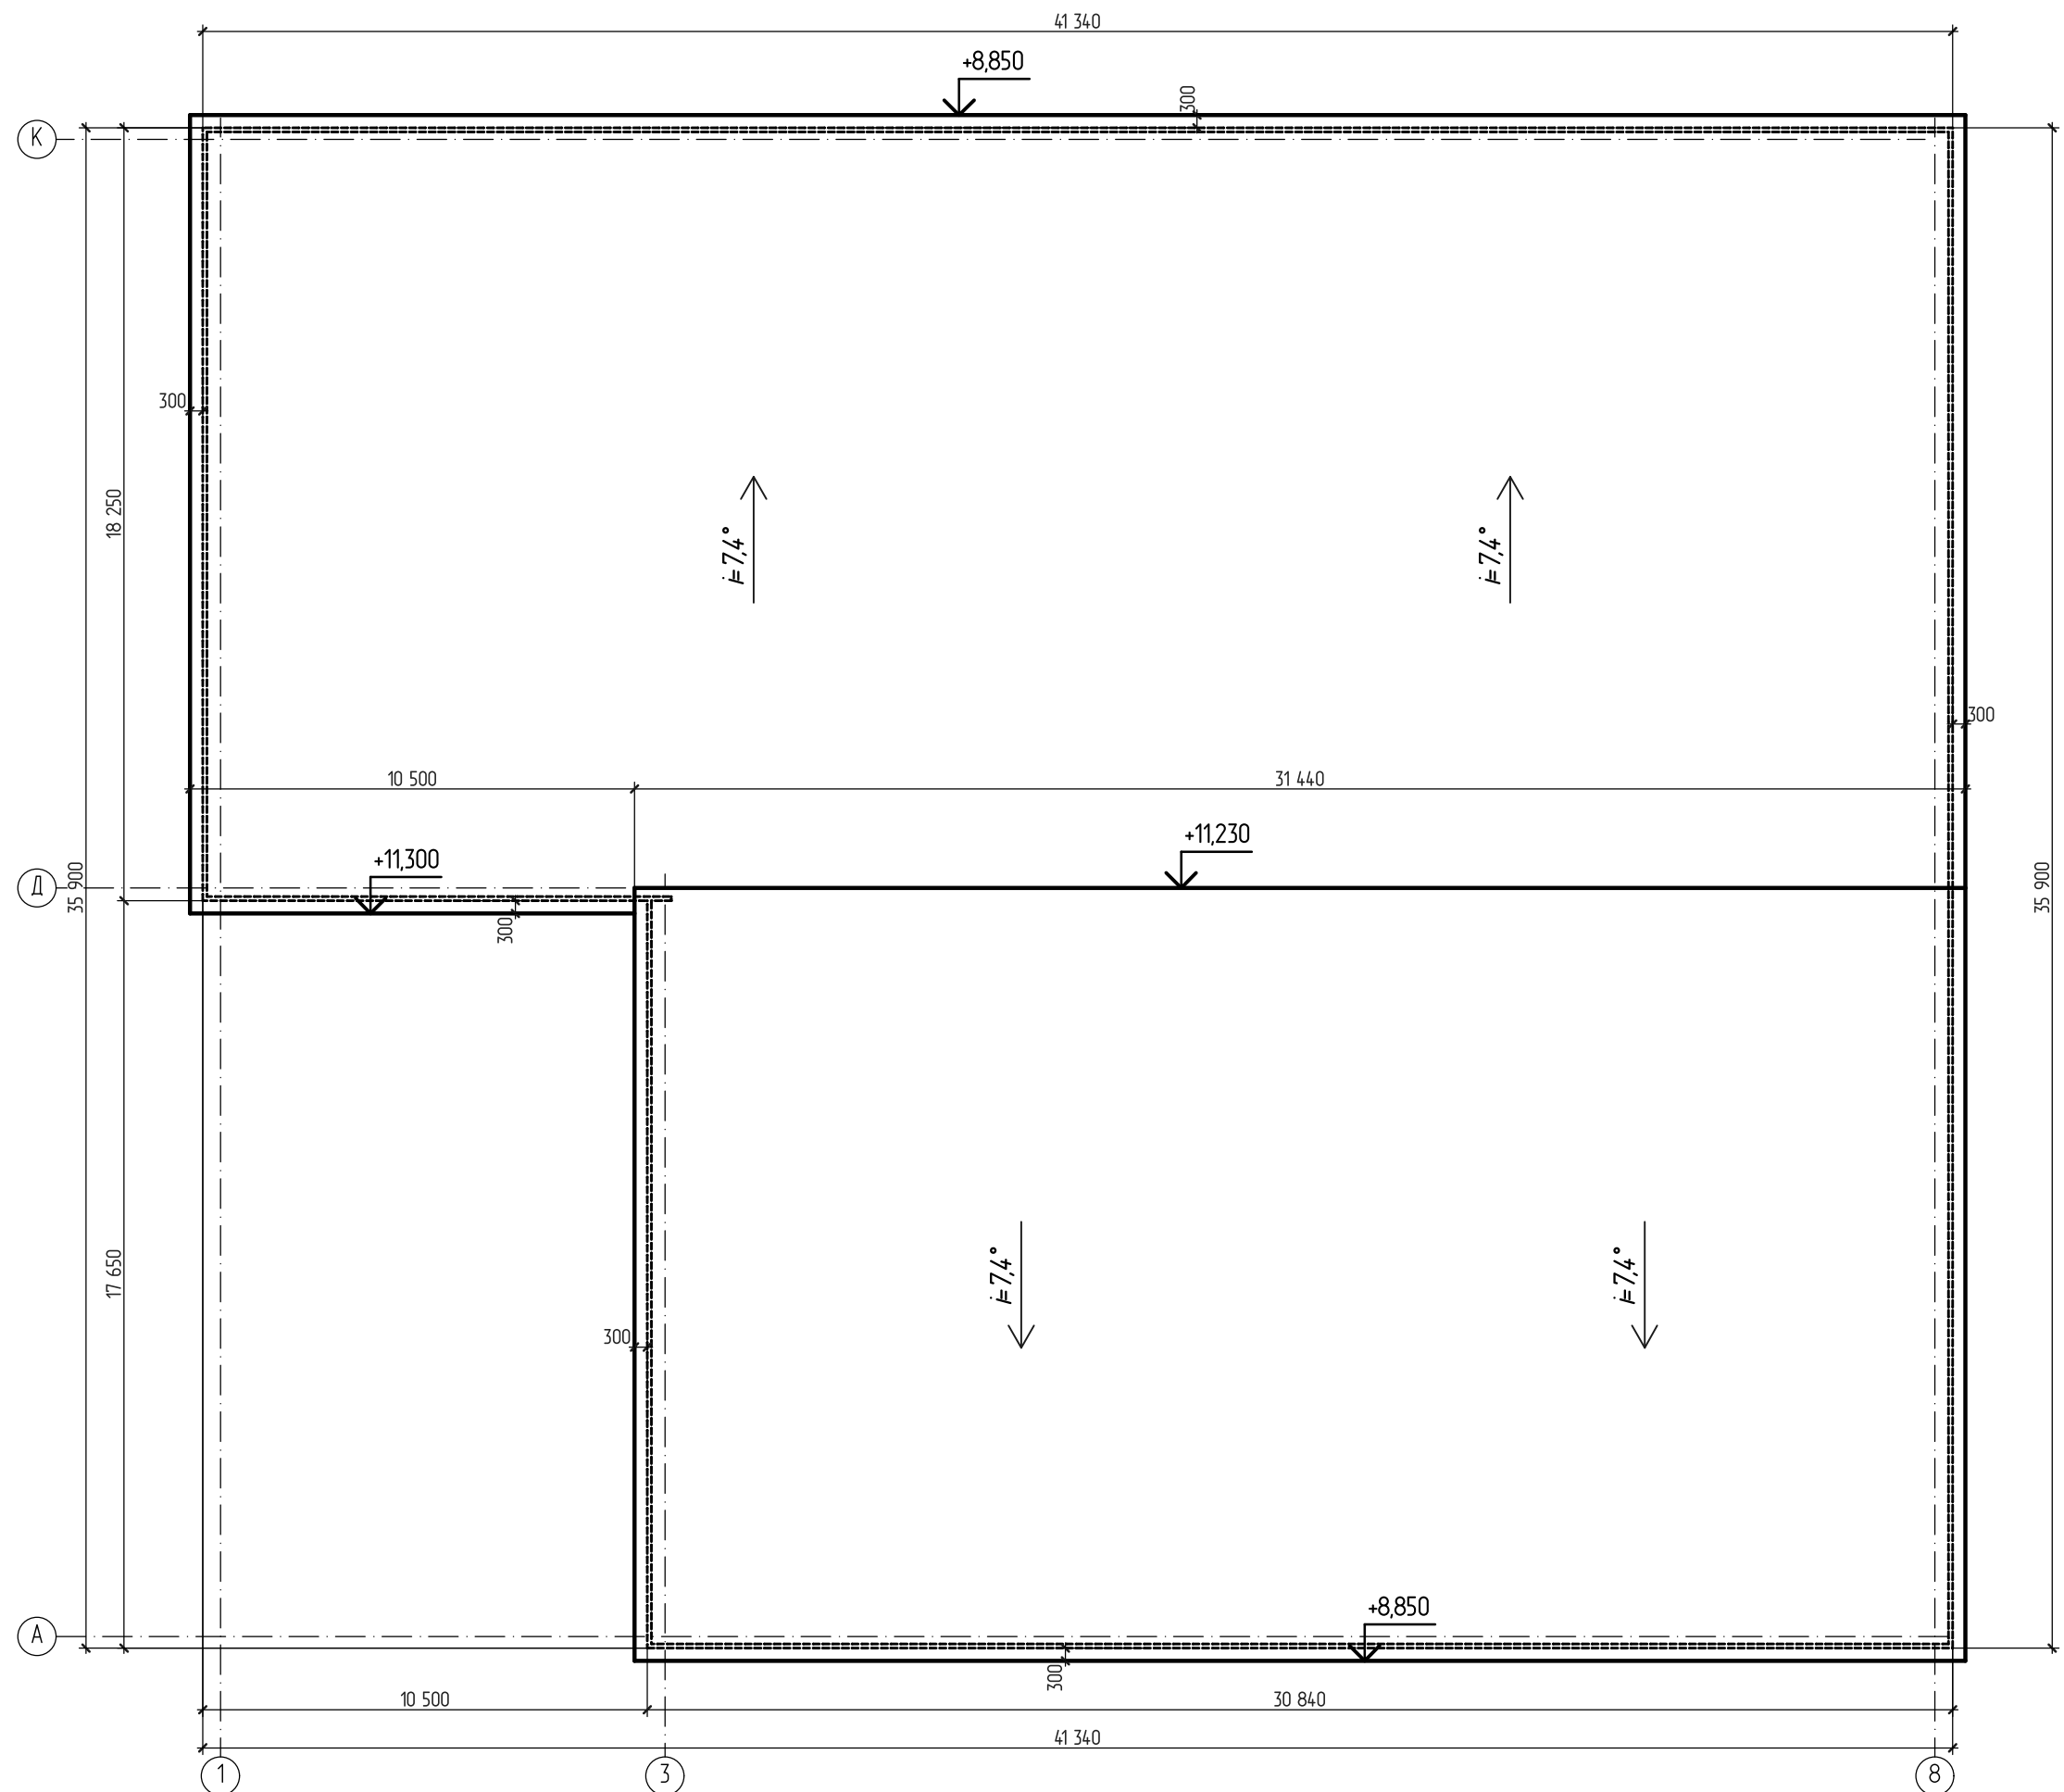


Изм.	Кол.лч.	Лист	№ док.	Подпись.	Дата

План кровли.

Лист

114


Схема расположения металлических колонн на отм. +0.000. М 1:200.

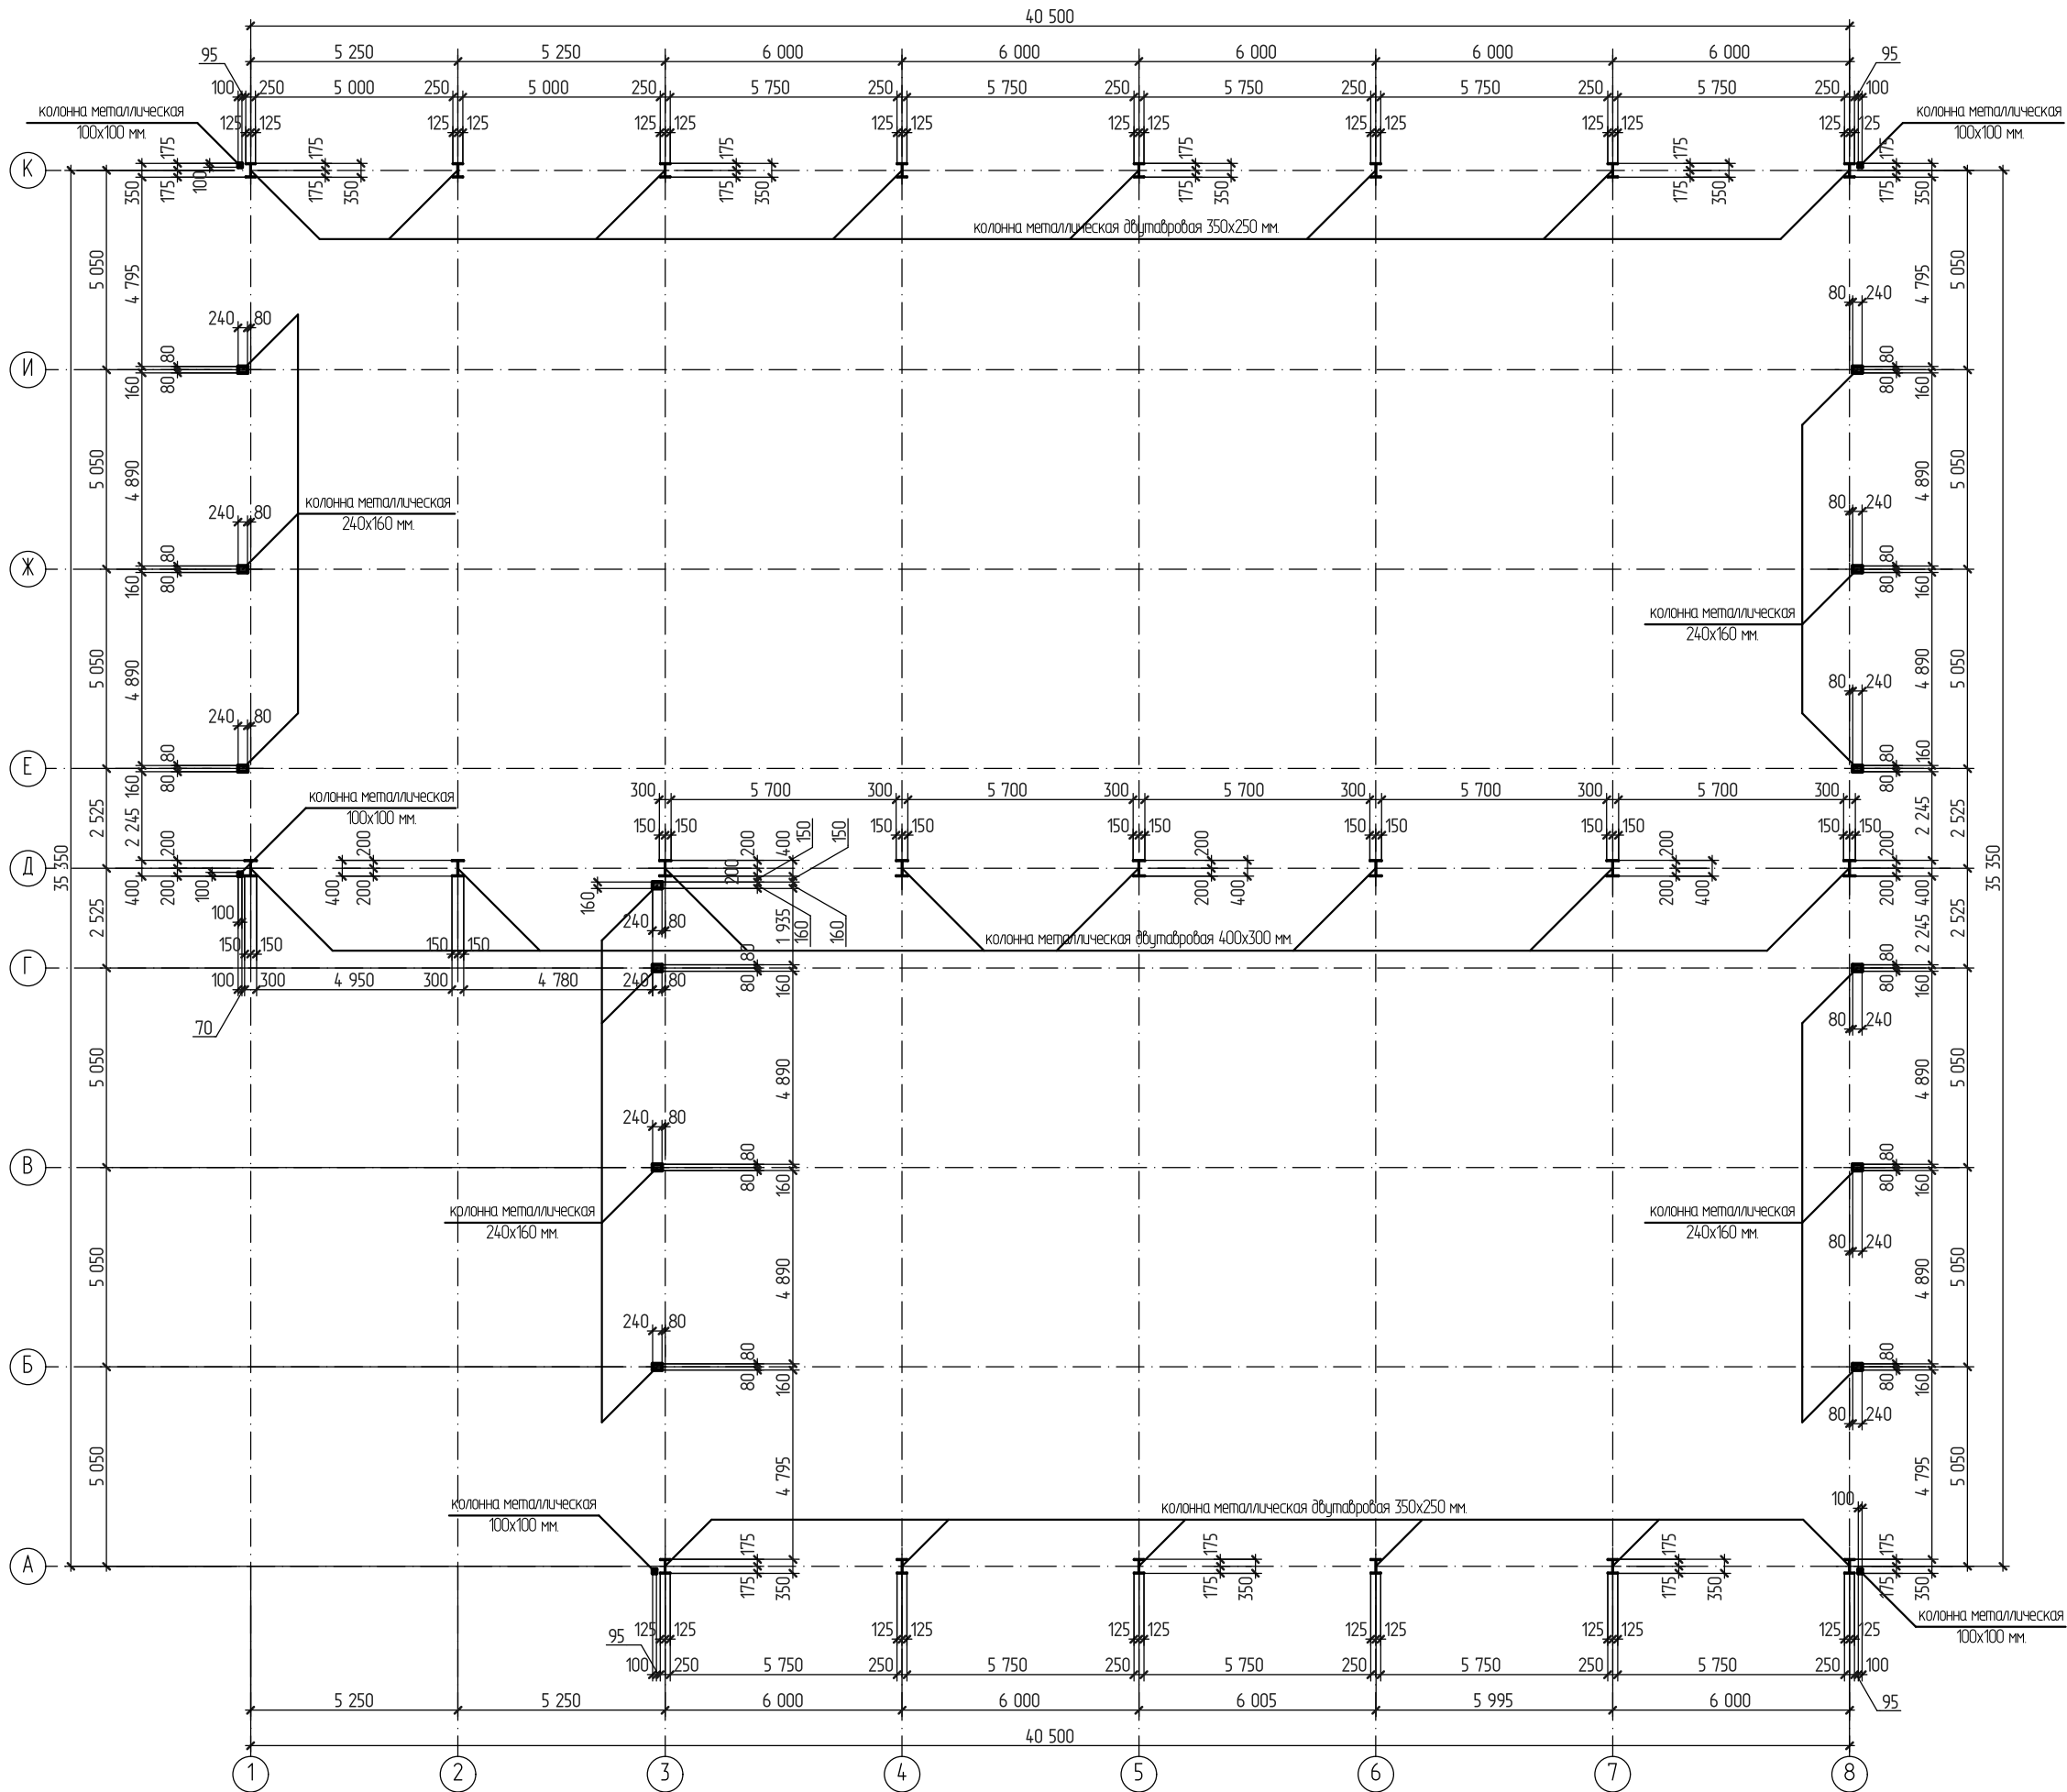

Изм.	Кол.уч.	Лист	№ док.	Подпись	Дата

Схема металлических колонн.

Схема расположения металлических ферм, прогонов и связей. М 1:200.

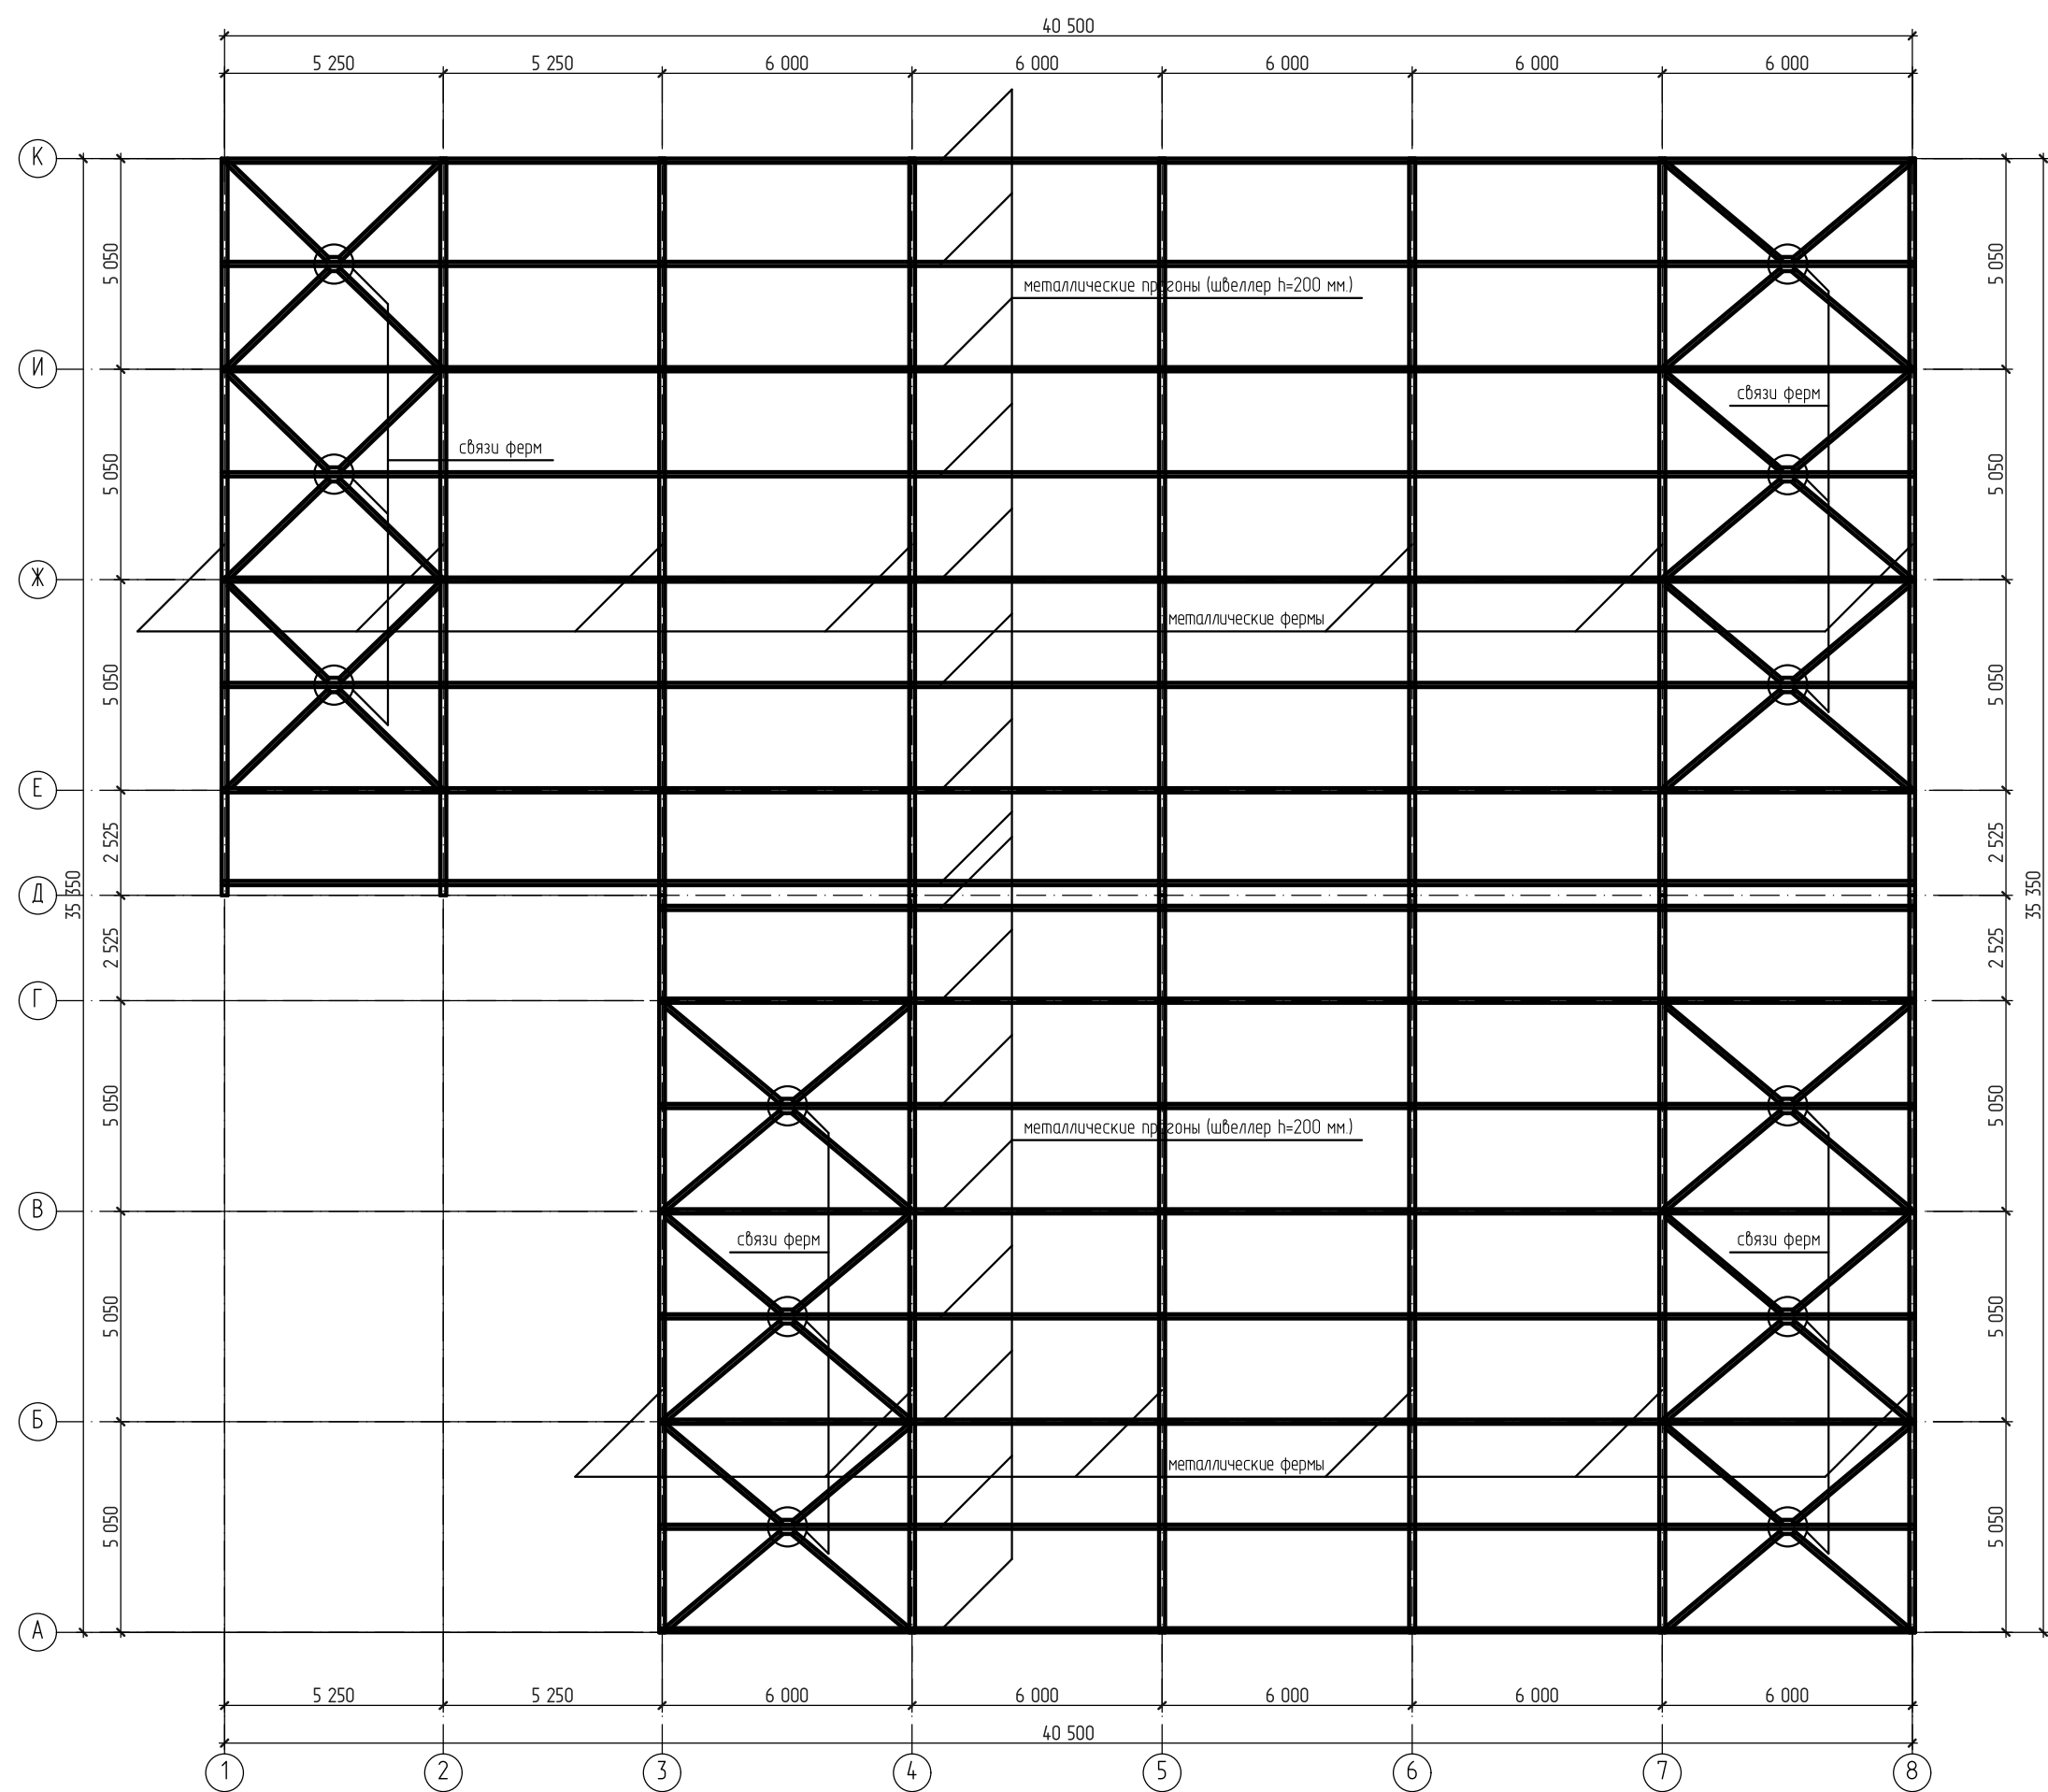


Изм.	Кол.уч.	Лист	№ док.	Подпись	Дата

Схема расположения металлических ферм, прогонов и связей.


Лист

Разрез 1-1. М 1:100.

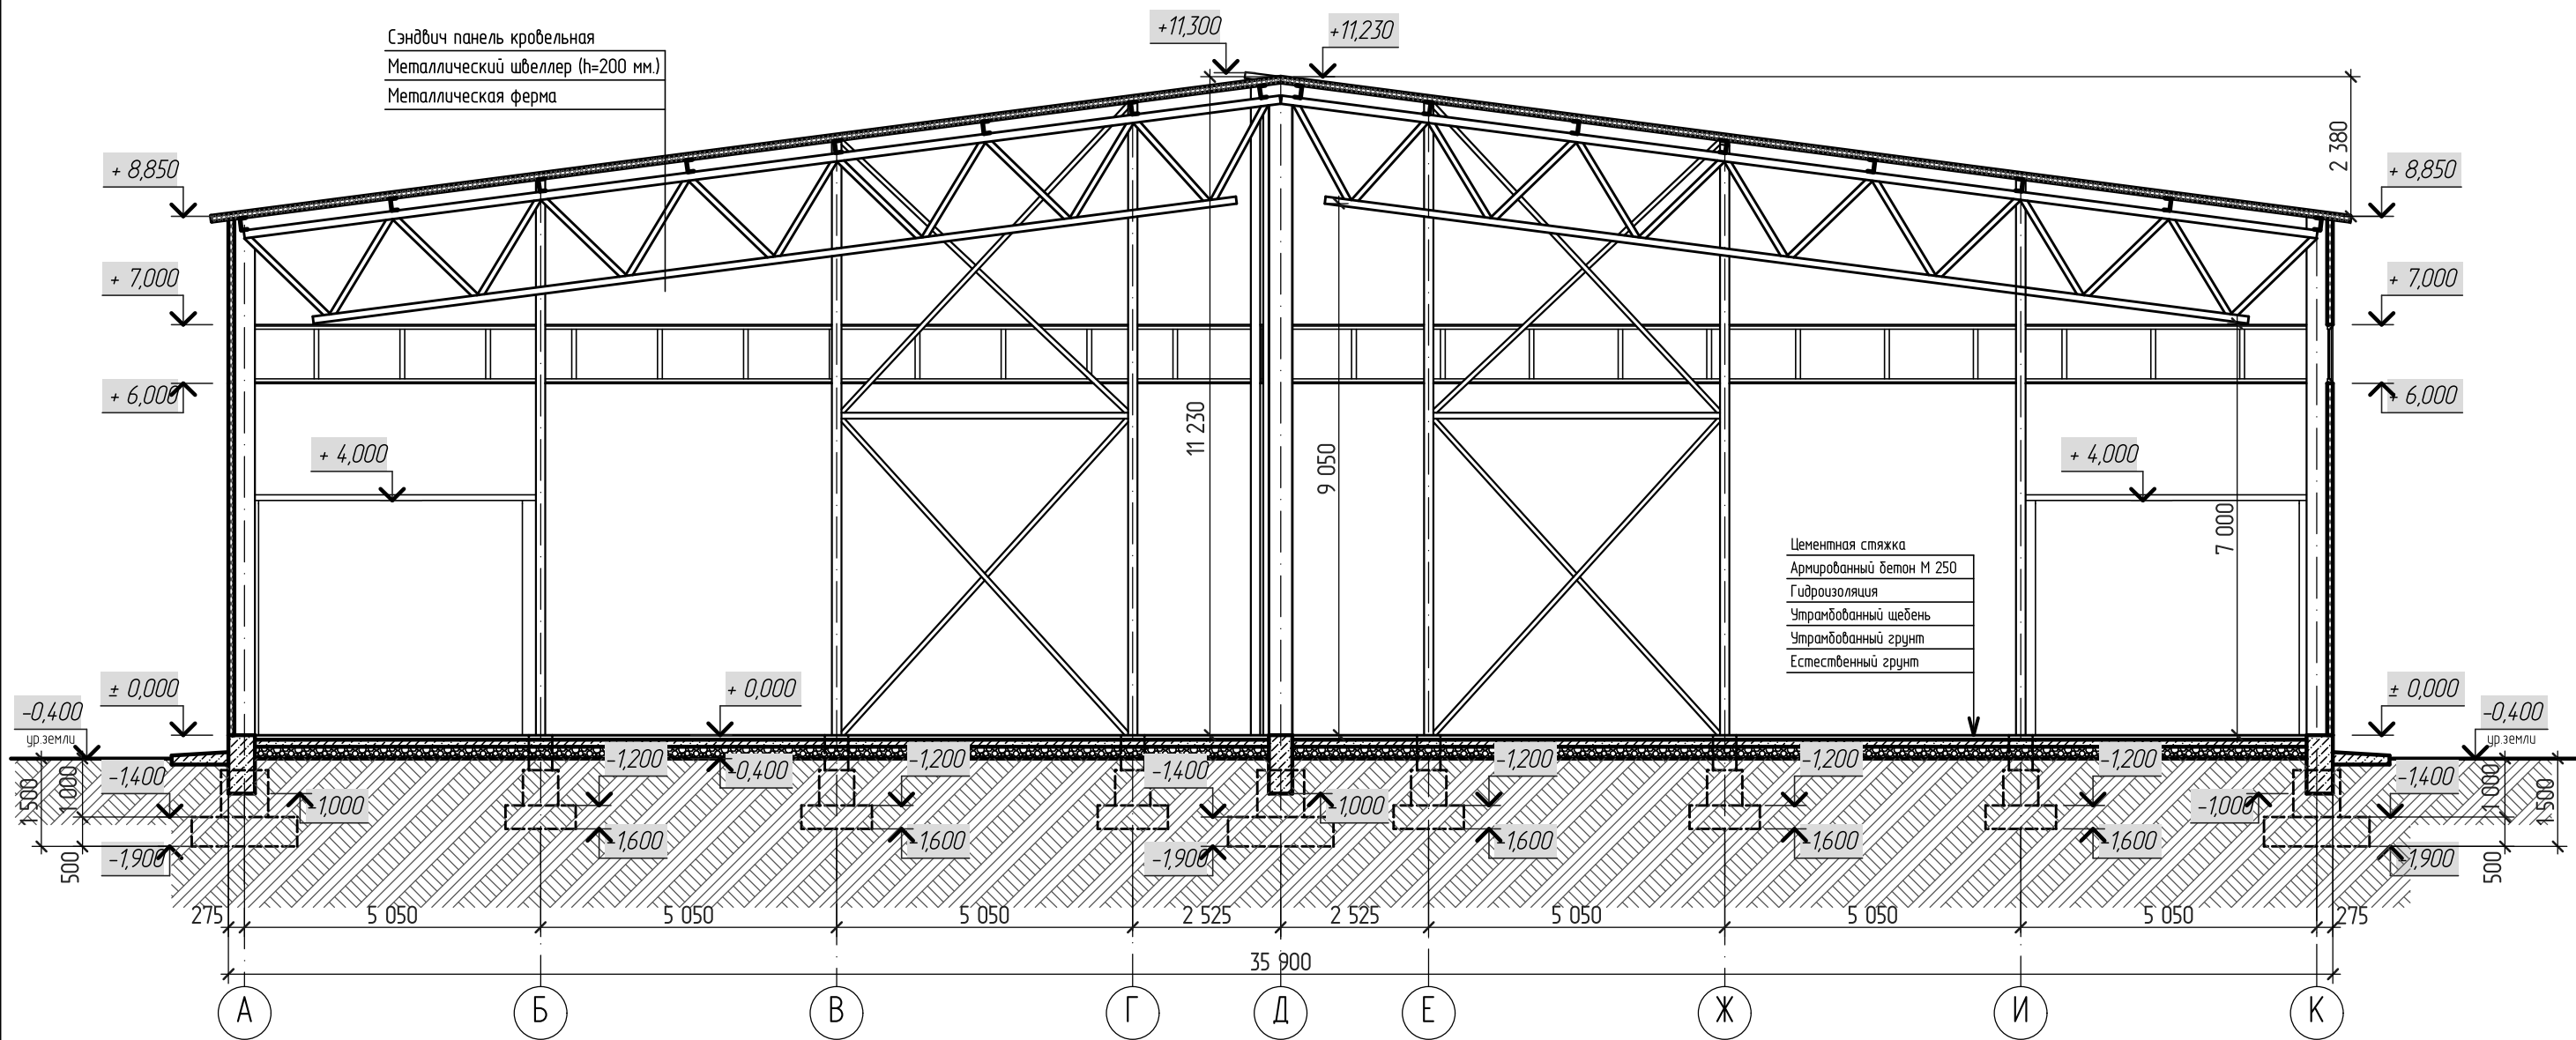


						2024 - 059		
						Объект: Производственно-складское здание по адресу: Ростовская область, Мясниковский район, 1-й км автодороги Ростов-на-Дону-Новошахтинск, уч. № 10/8. Кад. № земельного участка: 61:25:0600401:4136. Заказчик: Агаджанян Т.А.		
Изм.	Кол.уч.	Лист	№ док.	Подпись	Дата	Проект производственно-складского здания	Стадия	Лист
Архитектор	Гайдарян А.А.				2024		П	
Проверил	Гайдарян А.А.				2024	Разрез 1-1.	ИП. Гайдарян А.А. с.Чалтырь.	


Разрез 2-2. М 1:150.

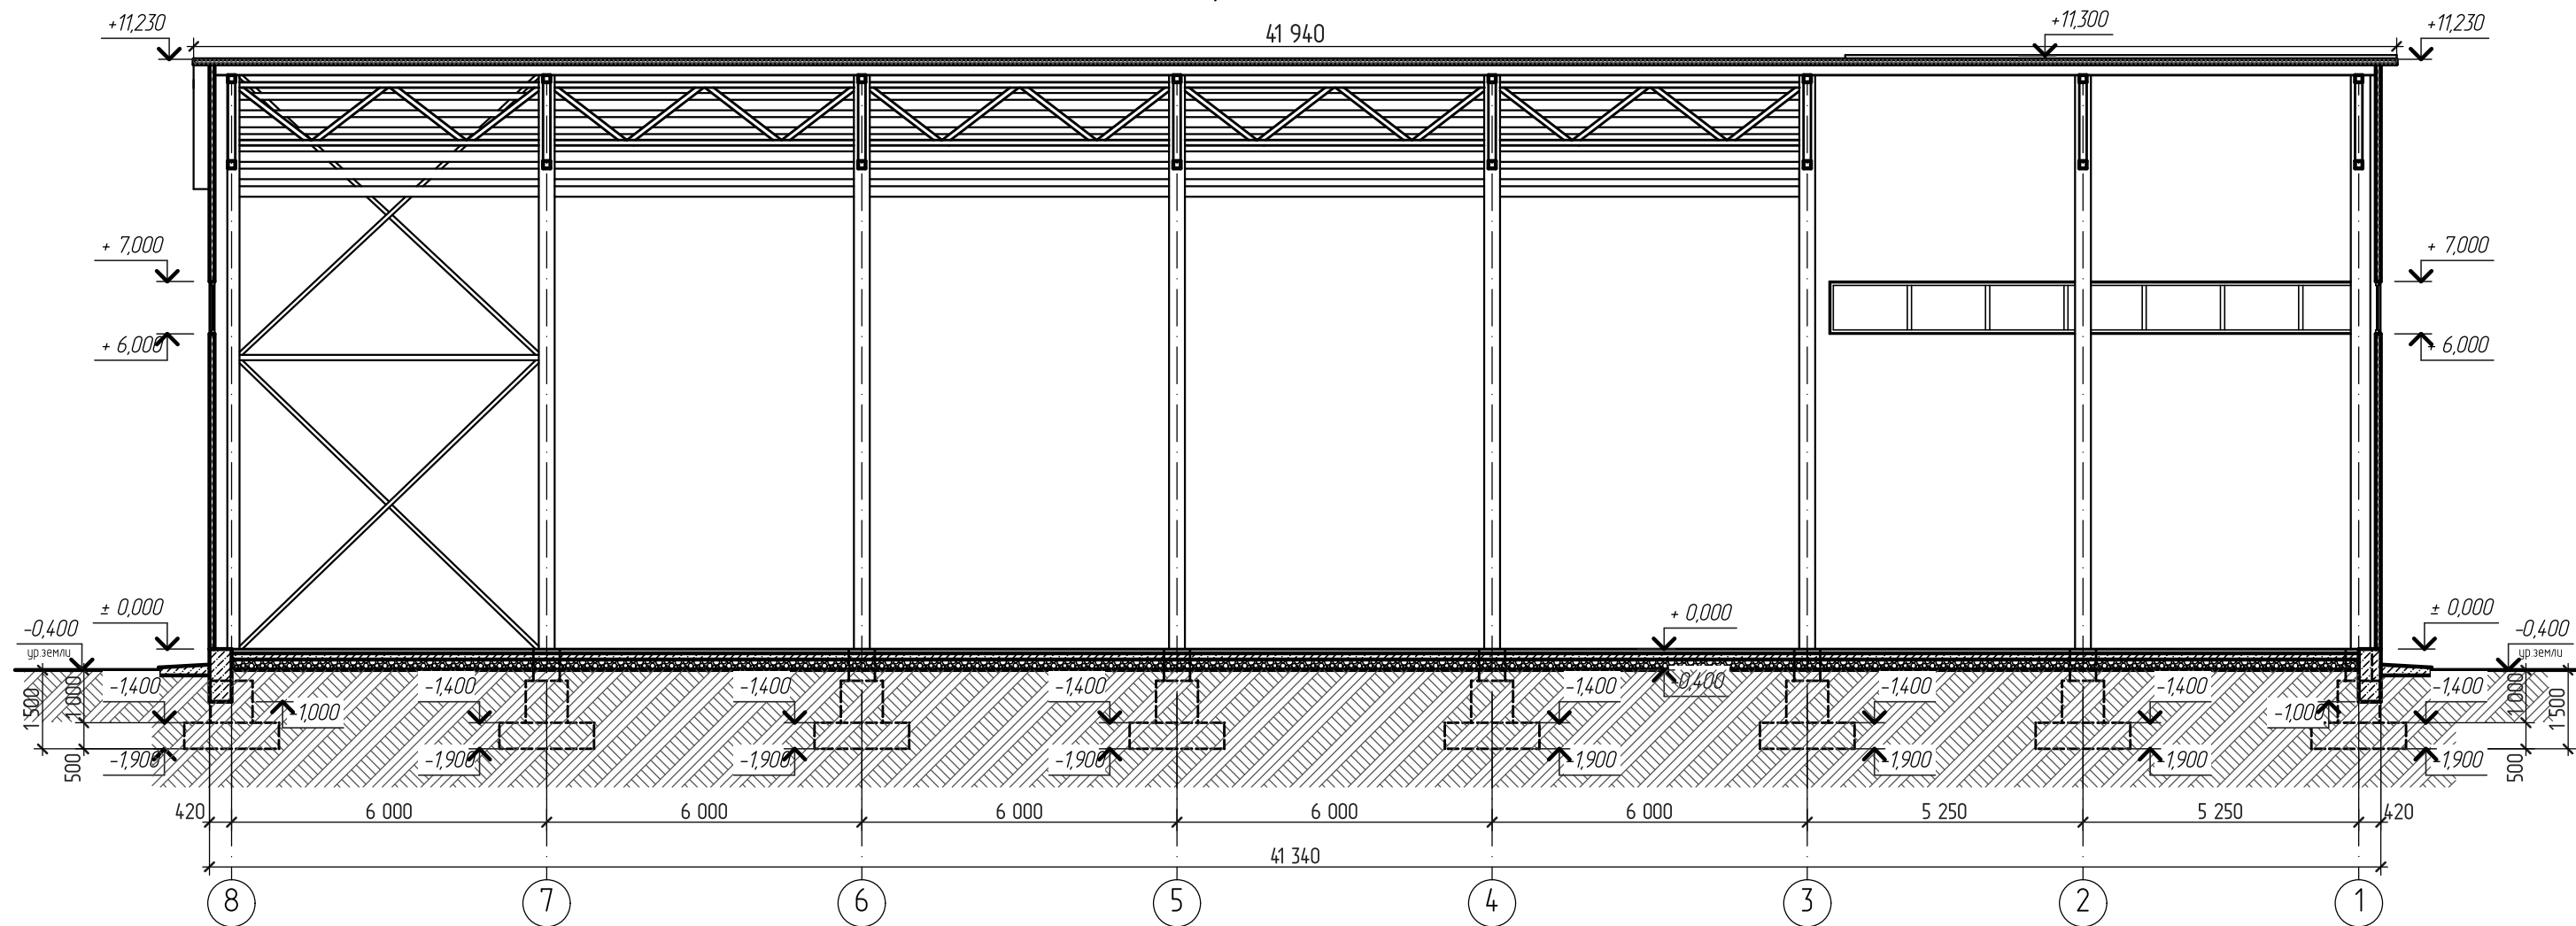

						2024 - 059		
						Объект: Производственно-складское здание по адресу: Ростовская область, Мясниковский район, 1-й км автодороги Ростов-на-Дону-Новошахтинск, уч. № 10/8. Кад. № земельного участка: 61:25:0600401:4136. Заказчик: Агаджанян Т.А.		
Изм.	Кол.уч.	Лист	№ док.	Подпись	Дата	Проект производственно-складского здания	Стадия	Лист
							П	Листов
Архитектор	Гайдарян А.А.			2024		Разрез 2-2.	И.П. Гайдарян А.А. с.Чалтырь.	
Проверил	Гайдарян А.А.			2024				

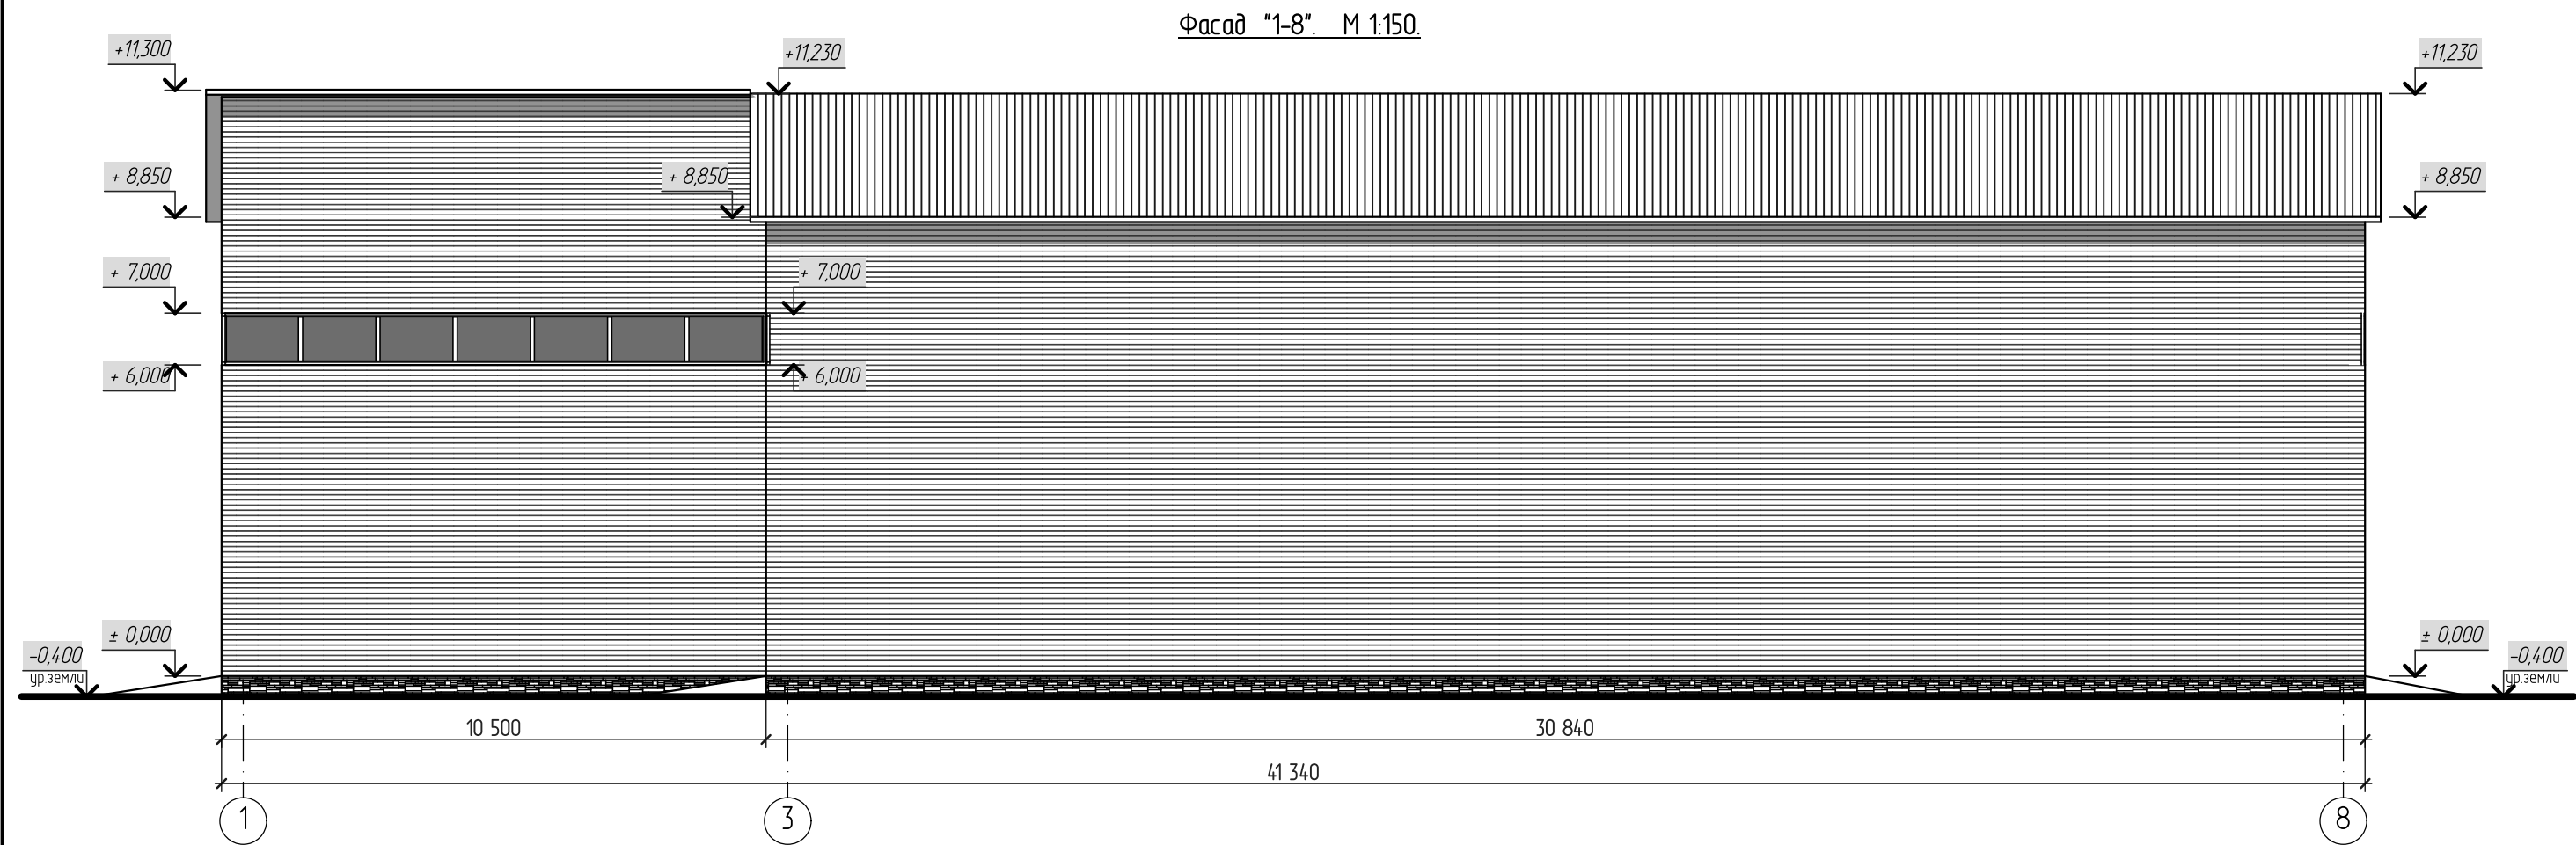


						2024 - 059			
						Объект: Производственно-складское здание по адресу: Ростовская область, Мясниковский район, 1-й км автодороги Ростов-на-Дону-Новошахтинск, уч. № 10/8.			
						Кад. № земельного участка: 61:25:0600401:4136. Заказчик: Агаджанян Т.А.			
Изм.	Кол.уч.	Лист	№ док.	Подпись	Дата	Проект производственно-складского здания	Стадия	Лист	Листов
Архитектор	Гайдарян А.А.			2024	П				
Проверил	Гайдарян А.А.			2024					
						Фасад 1-8.	ИП. Гайдарян А.А. с.Чалтырь.		

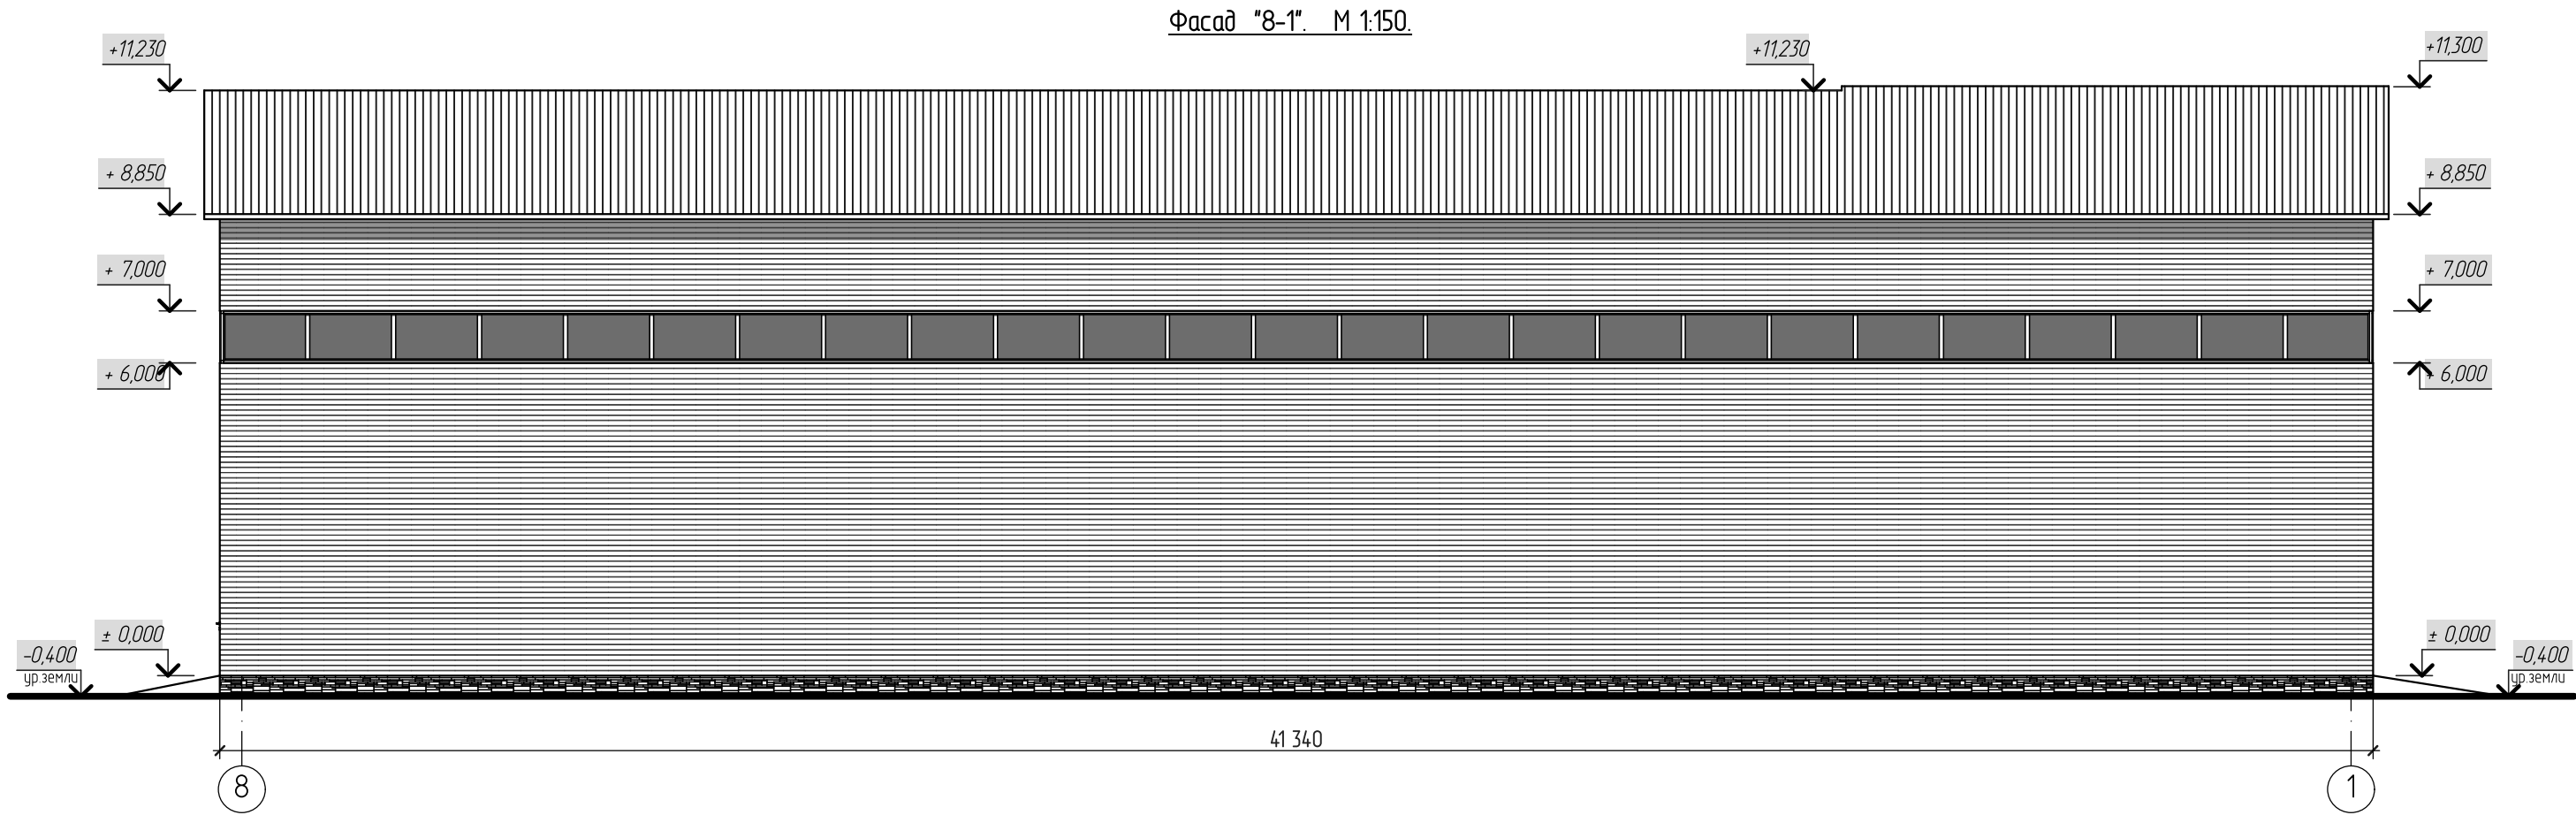


						2024 - 059			
						Объект: Производственно-складское здание по адресу: Ростовская область, Мясниковский район, 1-й км автодороги Ростов-на-Дону-Новошахтинск, уч. № 10/8. Кад. № земельного участка: 61:25:0600401:4136. Заказчик: Агаджанян Т.А.			
Изм.	Кол.уч.	Лист	№ док.	Подпись	Дата	Проект производственно-складского здания	Стадия	Лист	Листов
Архитектор		Гайдарян А.А.			2024		П		
Проверил		Гайдарян А.А.			2024				
						Фасад 8-1.	ИП. Гайдарян А.А. с.Чалтырь.		

Фасад "А-К". М 1:100.




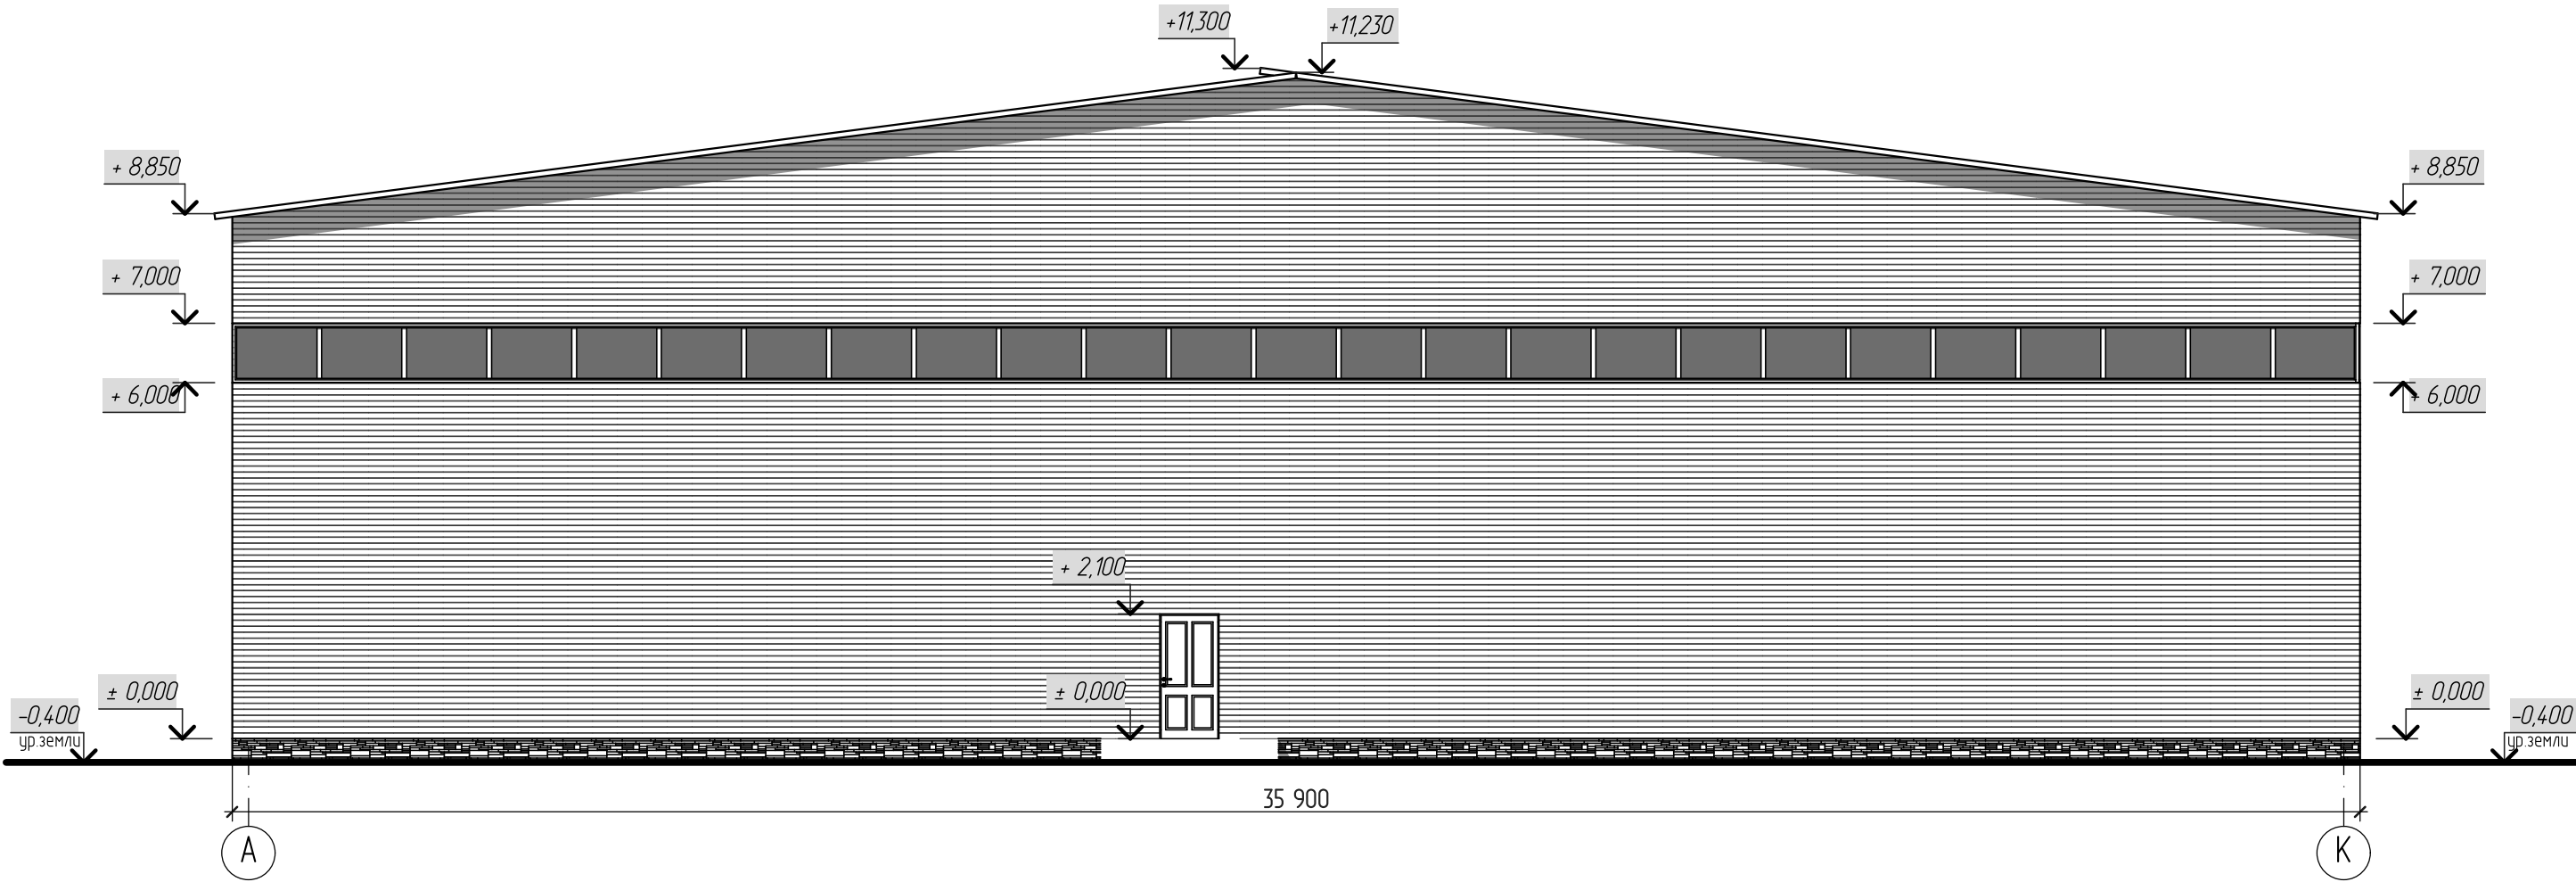


						2024 - 059			
						Объект: Производственно-складское здание по адресу: Ростовская область, Мясниковский район, 1-й км автодороги Ростов-на-Дону-Новошахтинск, уч. № 10/8. Кад. № земельного участка: 61:25:0600401:4136. Заказчик: Агаджанян Т.А.			
Изм.	Кол.уч.	Лист	№ док.	Подпись	Дата	Проект производственно-складского здания	Стадия	Лист	Листов
Архитектор		Гайдарян А.А.			2024		П		
Проверил		Гайдарян А.А.			2024				
						Фасад А-К.	ИП. Гайдарян А.А. с.Чалтырь.		

Фасад "К-А". М 1:100.

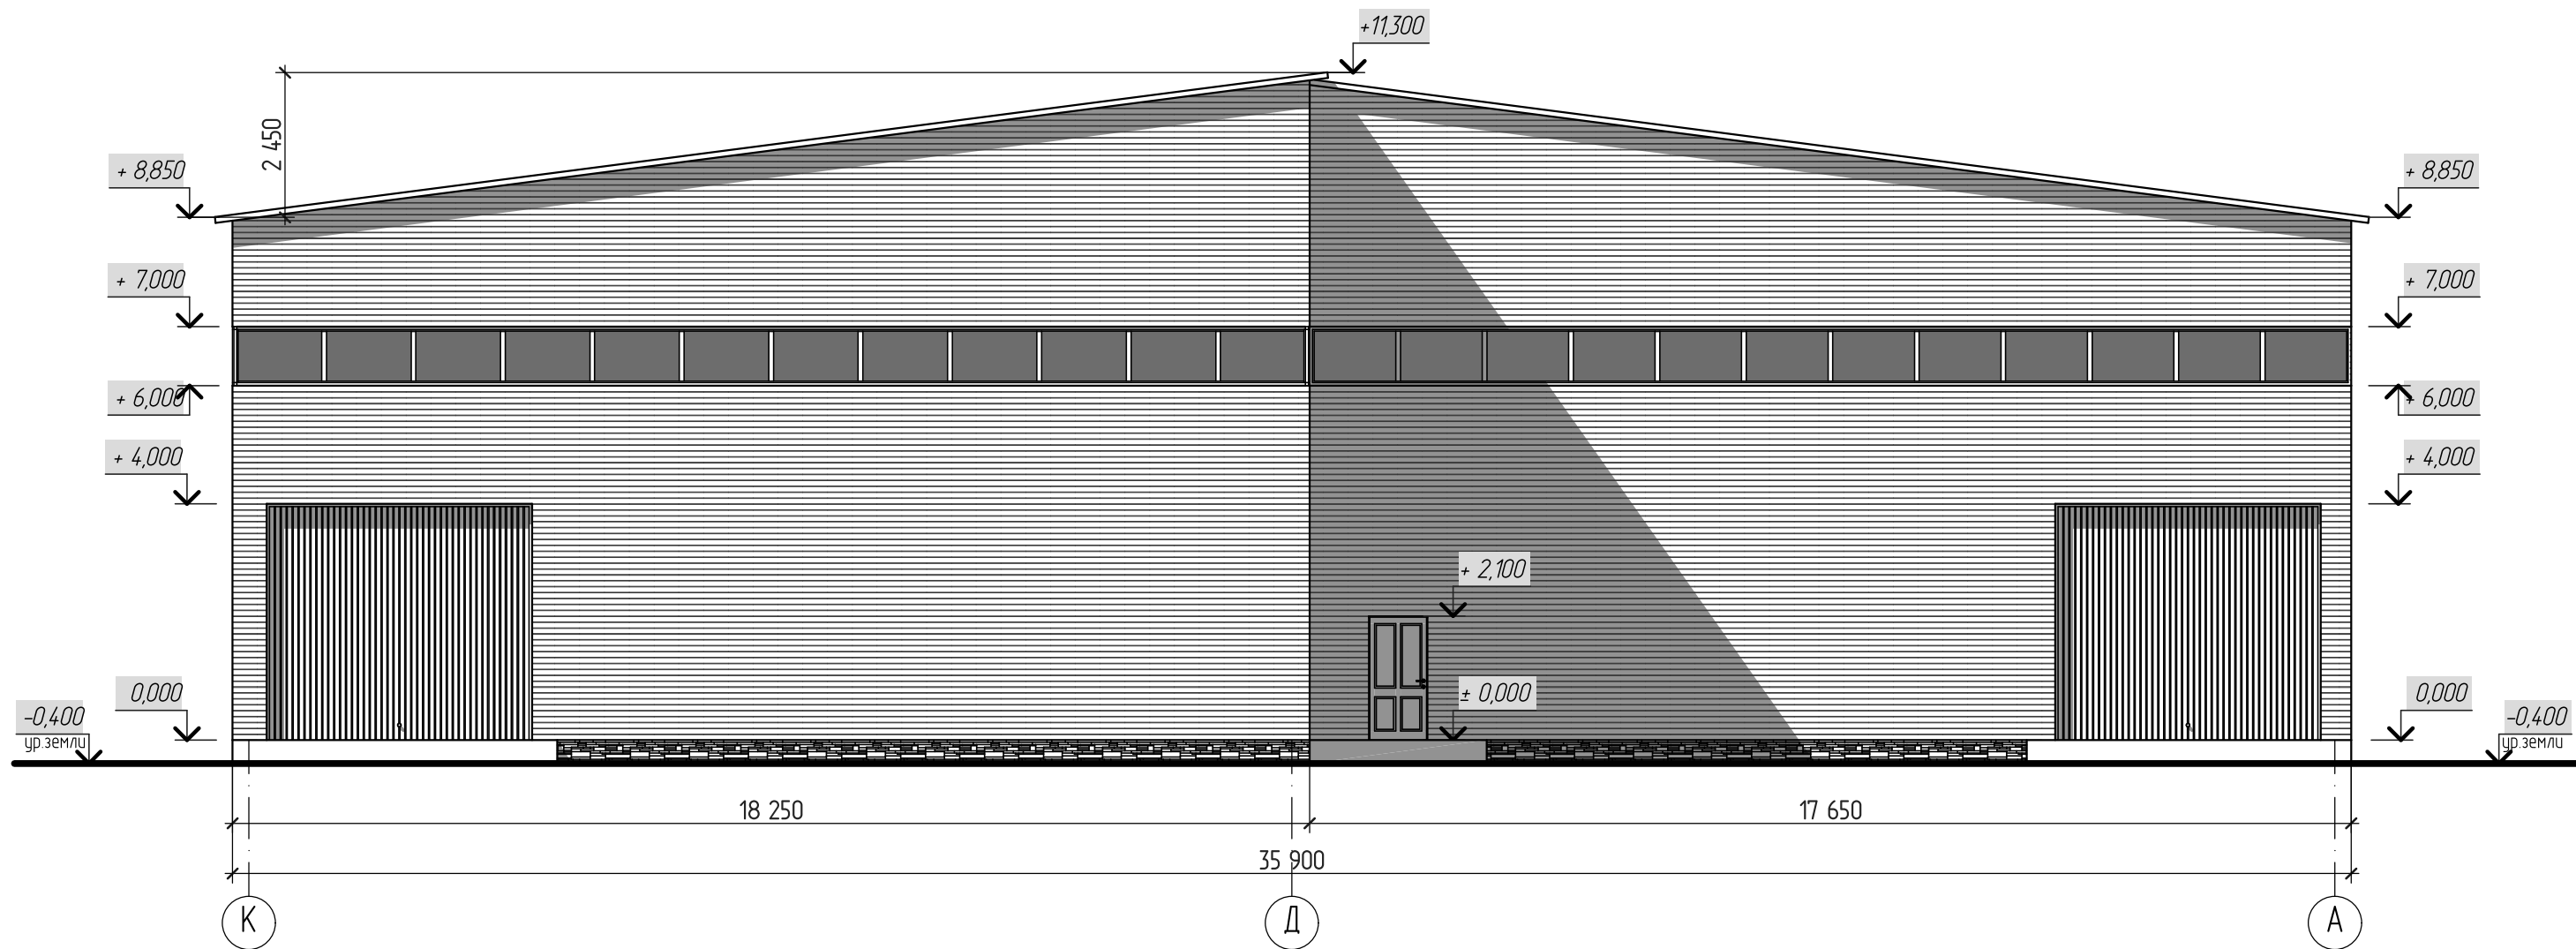

						2024 - 059			
						Объект: Производственно-складское здание по адресу: Ростовская область, Мясниковский район,1-й км автодороги Ростов-на-Дону-Новошахтинск, уч. № 10/8. Кад. № земельного участка: 61:25:0600401:4136. Заказчик: Агаджанян Т.А.			
Изм.	Кол.уч.	Лист	№ док.	Подпись.	Дата	Проект производственно-складского здания	Стадия	Лист	Листов
Архитектор		Гайдарян А.А.			2024		П		
Проверил		Гайдарян А.А.			2024				
						Фасад К-А.	ИП. Гайдарян А.А. с.Чалтырь.		

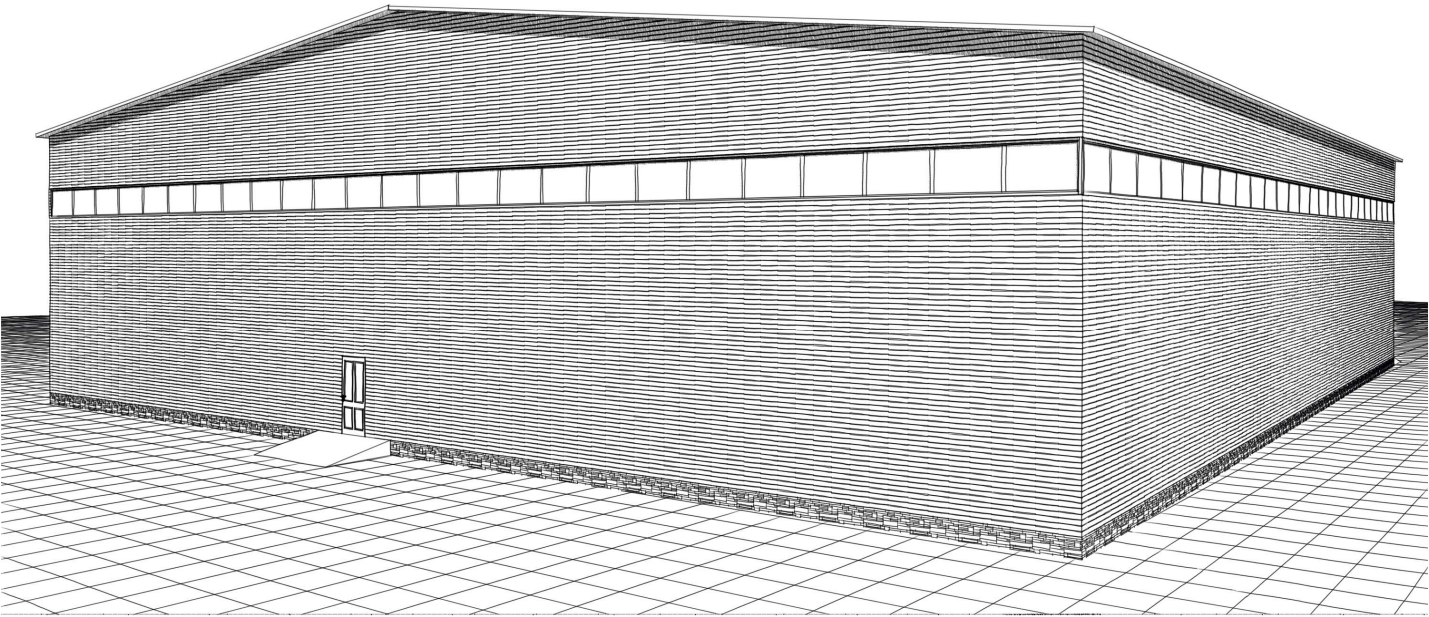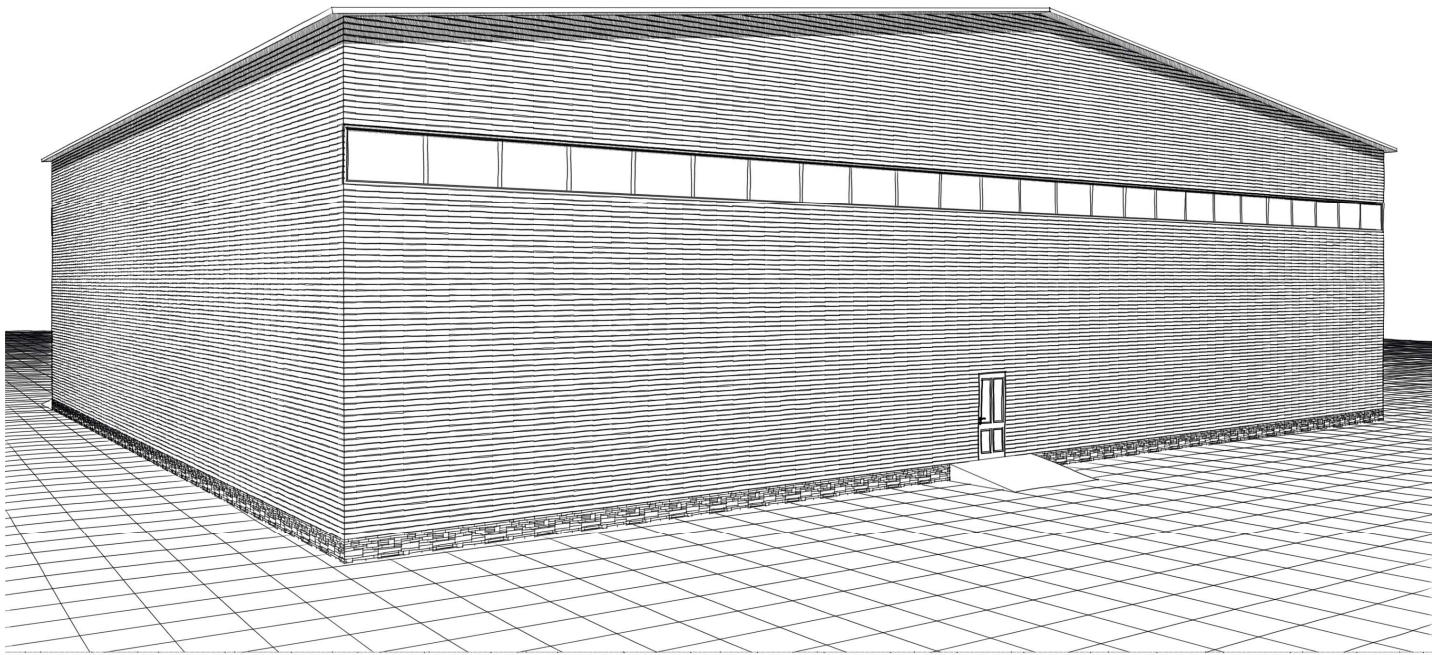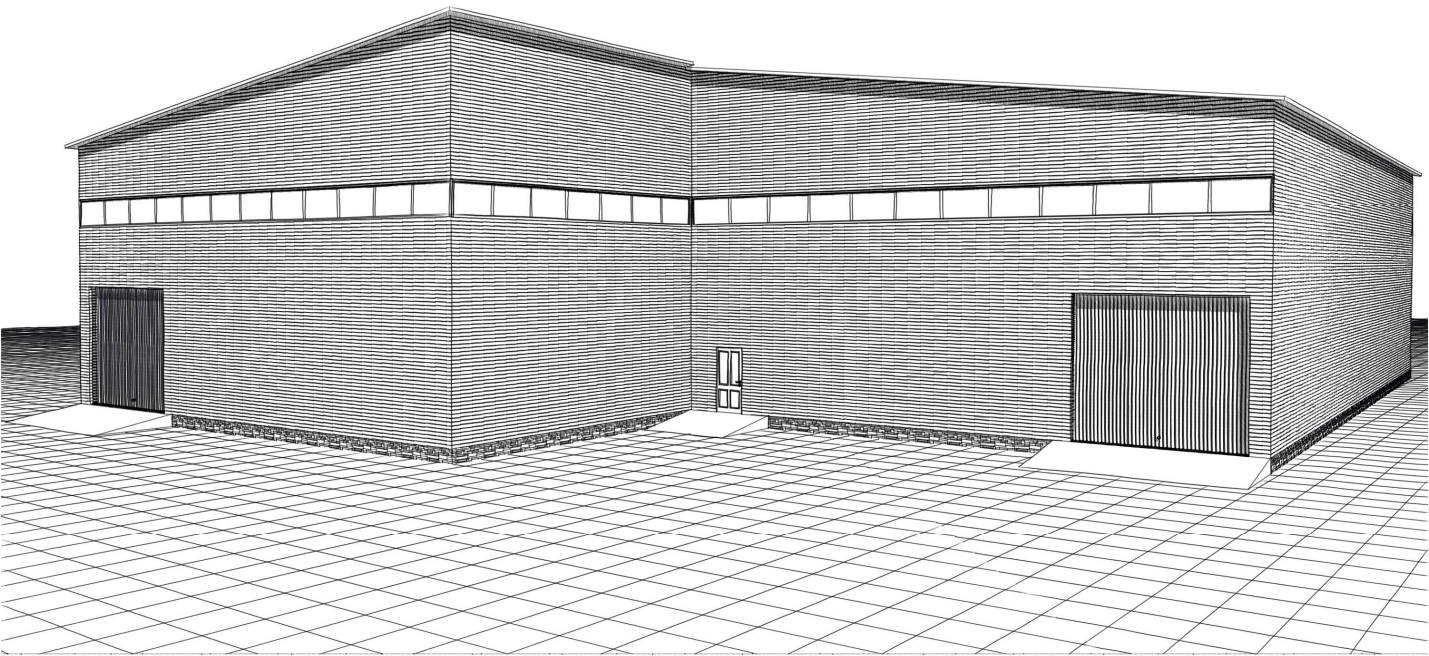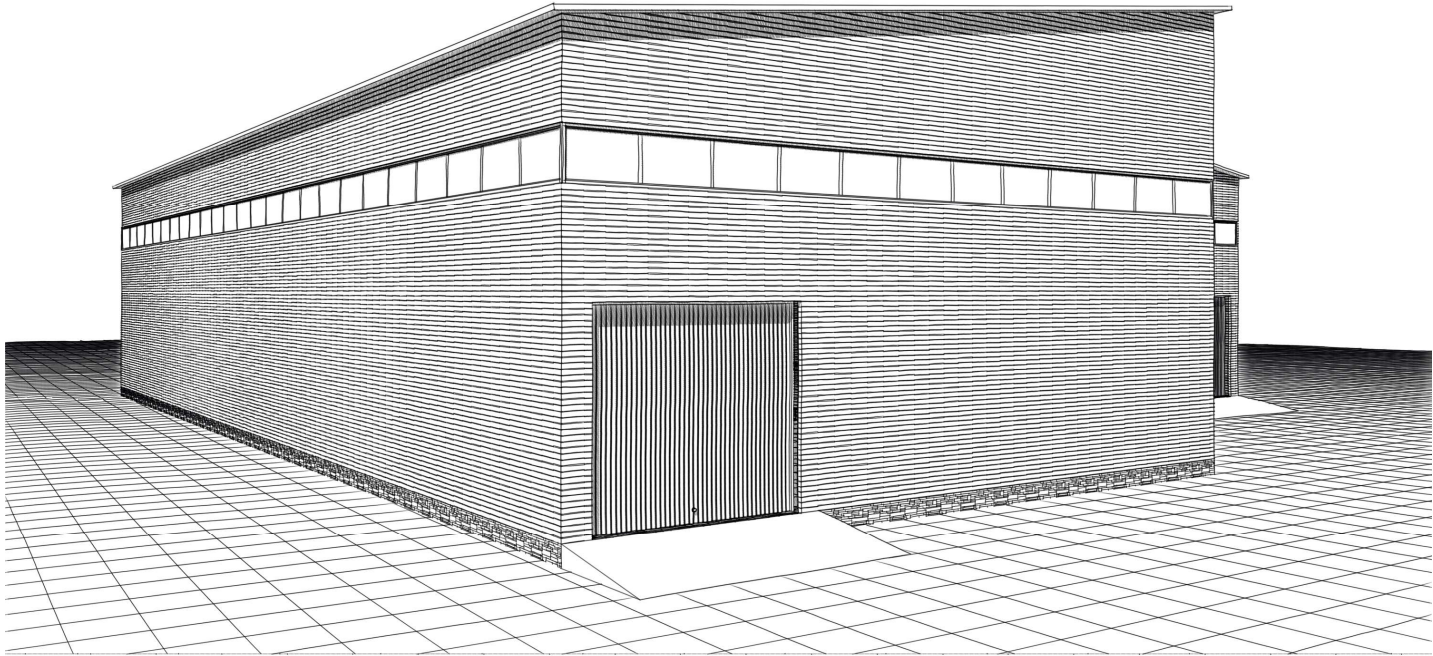

						2024 - 059			
						Объект: Производственно-складское здание по адресу: Ростовская область, Мясниковский район, 1-й км автодороги Ростов-на-Дону-Новошахтинск, уч. № 10/8. Кад. № земельного участка: 61:25:0600401:4136. Заказчик: Агаджанян Т.А.			
Изм.	Кол.уч.	Лист	№ док.	Подпись	Дата	Проект производственно-складского здания	Стадия	Лист	Листов
Архитектор		Гайдарян А.А.			2024		П		
Проверил		Гайдарян А.А.			2024				
						Общая перспектива.	ИП. Гайдарян А.А. с.Чалтырь.		