

Межмуниципальный отдел по г. Электросталь и Ногинскому району Управления Федеральной службы государственной регистрации, кадастра и картографии по Московской области
полное наименование органа регистрации прав

Выписка из Единого государственного реестра недвижимости об основных характеристиках и зарегистрированных правах на объект недвижимости

Сведения об основных характеристиках объекта недвижимости

В Единый государственный реестр недвижимости внесены следующие сведения:

Раздел 1 Лист 1

Земельный участок			
вид объекта недвижимости			
Лист № 1 раздела 1	Всего листов раздела 1: 1	Всего разделов: 3	Всего листов выписки: 3
06.08.2021г.			
Кадастровый номер:	50:46:0010201:515		
Номер кадастрового квартала:	50:46:0010201		
Дата присвоения кадастрового номера:	26.11.2012		
Ранее присвоенный государственный учетный номер:	данные отсутствуют		
Местоположение:	Московская область, г. Электросталь, ул. Красная, дом 19		
Площадь, м2:	7645 +/- 31		
Кадастровая стоимость, руб:	12205701.2		
Кадастровые номера расположенных в пределах земельного участка объектов недвижимости:	50:46:0000000:3996		
Категория земель:	Земли населенных пунктов		
Виды разрешенного использования:	для производственных цехов ОАО "Электростальский завод тяжелого машиностроения"		
Статус записи об объекте недвижимости:	Сведения об объекте недвижимости имеют статус "актуальные"		
Особые отметки:	данные отсутствуют		
Получатель выписки:	Велтистов Михаил Георгиевич (представитель правообладателя), Правообладатель: от имени заявителя Общество с ограниченной ответственностью "Торговое оборудование "Евромаркет", 7719756952		



полное наименование должности		
	подпись	инициалы, фамилия

М.П.

Выписка из Единого государственного реестра недвижимости об основных характеристиках и зарегистрированных правах на объект недвижимости

Сведения о зарегистрированных правах

Земельный участок			
вид объекта недвижимости			
Лист № 1 раздела 2	Всего листов раздела 2: 1	Всего разделов: 3	Всего листов выписки: 3
06.08.2021г.			
Кадастровый номер:		50:46:0010201:515	

1	Правообладатель (правообладатели):	1.1	Общество с ограниченной ответственностью "Торговое оборудование "Евромаркет", ИНН: 7719756952, ОГРН: 1107746622433
2	Вид, номер, дата и время государственной регистрации права:	2.1	Собственность 50:46:0010201:515-50/706/2021-15 05.08.2021 14:20:35
3	Документы-основания	3.1	Договор купли-продажи квартиры, № 01-21/644, выдан 25.06.2021
4	Сведения об осуществлении государственной регистрации сделки, права, ограничения права без необходимого в силу закона согласия третьего лица, органа:	4.1	данные отсутствуют
5	Ограничение прав и обременение объекта недвижимости:	не зарегистрировано	
6	Заявленные в судебном порядке права требования:	данные отсутствуют	
7	Сведения о возражении в отношении зарегистрированного права:	данные отсутствуют	
8	Сведения о наличии решения об изъятии объекта недвижимости для государственных и муниципальных нужд:	данные отсутствуют	
9	Сведения о невозможности государственной регистрации без личного участия правообладателя или его законного представителя:	данные отсутствуют	
10	Правопритязания и сведения о наличии поступивших, но не рассмотренных заявлений о проведении государственной регистрации права (перехода, прекращения права), ограничения права или обременения объекта недвижимости, сделки в отношении объекта недвижимости:	Представлены документы на государственную регистрацию: Право: Реестровая запись	
11	Сведения о невозможности государственной регистрации перехода, прекращения, ограничения права на земельный участок из земель сельскохозяйственного назначения:	данные отсутствуют	



полное наименование должности	подпись	инициалы, фамилия

М.П.

Выписка из Единого государственного реестра недвижимости об основных характеристиках и зарегистрированных правах на объект недвижимости


Описание местоположения земельного участка

Земельный участок			
вид объекта недвижимости			

Лист № 1 раздела 3	Всего листов раздела 3: 1	Всего разделов: 3	Всего листов выписки: 3
--------------------	---------------------------	-------------------	-------------------------

06.08.2021г.	
Кадастровый номер:	50:46:0010201:515

План (чертеж, схема) земельного участка

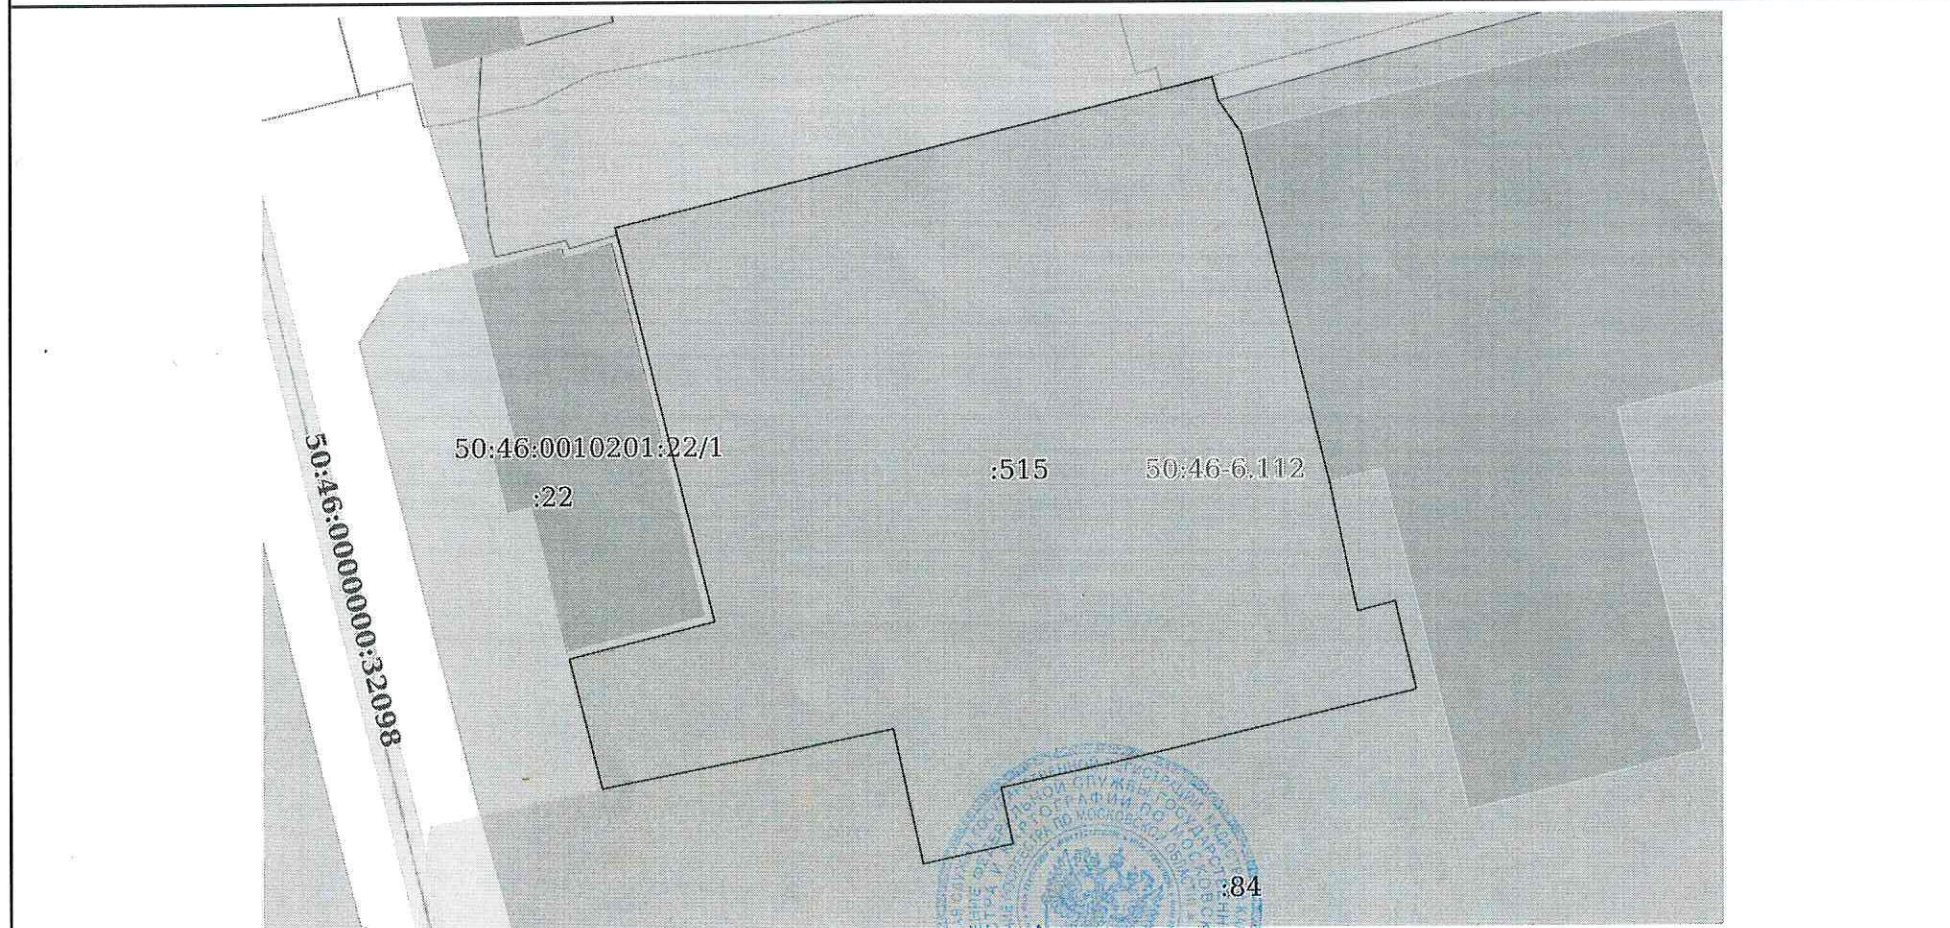

Масштаб 1:1000	Условные обозначения:	
----------------	-----------------------	--

полное наименование должности	подпись	инициалы, фамилия
-------------------------------	---------	-------------------

М.П.