

**ОБЩЕСТВО
С ОГРАНИЧЕННОЙ
ОТВЕТСТВЕННОСТЬЮ
«ГЕРАСИМОВ-ПРОЕКТ.К»**



Сайт: gerasimov-proekt.ru
E-mail: gerasimov100@mail.ru
Тел.: +7 (495) 961-44-08

**Здание склада по адресу:
Московская область, д. Грибки, д. 62**

Проектная документация

Архитектурные решения

03.04.23--АР

Москва – 2023

**ОБЩЕСТВО
С ОГРАНИЧЕННОЙ
ОТВЕТСТВЕННОСТЬЮ
«ГЕРАСИМОВ-ПРОЕКТ.К»**



Сайт: gerasimov-proekt.ru
E-mail: gerasimov100@mail.ru
Тел.: +7 (495) 961-44-08

**Здание склада по адресу:
Московская область, д. Грибки, д. 62**

Проектная документация

Архитектурные решения

03.04.23--АР

Генеральный директор

Главный инженер проекта



Герасимов Д. А.

Герасимов Д. А.

Москва – 2023

ВЕДОМОСТЬ ЧЕРТЕЖЕЙ										
Лист		Наименование							Примечание	
1		Общие данные								
2		План 1 этажа, М 1:100								
3		План 2 этажа, М 1:100								
4		Разрезы, М 1:100								
5		Фасады, М 1:100								
6		Спецификация сэндвич-панелей								
7		Элементы заполнения наружных проемов								
8		Схема посадки на участок								
ВЕДОМОСТЬ ССЫЛОЧНЫХ И ПРИЛАГАЕМЫХ ДОКУМЕНТОВ										
Обозначение			Наименование						Примечание	
СП 55.13330.2016			"Дома жилые многоквартирные"							
СП 112.13330.2011			"Пожарная безопасность зданий и сооружений"							
СП 4.13130.2013			Системы противопожарной защиты. Ограничение распространения пожара на объектах защиты. Требования к объемно-планировочным и конструктивным решениям							
СП 52.13330.2016			"Естественное и искусственное освещение" Актуализированная редакция СНиП 23-05-95*							
СП 131.13330.2012			"Строительная климатология"							
Настоящий проект выполнен в соответствии с действующими нормами, правилами и стандартами, в том числе и по взрывопожаробезопасности.										
Главный архитектор проекта Гр /Герасимов/										
03.04.23-АР										
Здание склада по адресу: Московская область, д. Грибки, д. 62										
Изм.		Кол. уч.		Лист		№ док.		Подп.		Дата
ГИП				Герасимов				Гр		
Исполн.				Танайлов						
Н. контр.				Герасимов				Гр		
Архитектурные решения								Стадия		Лист
								П		2
Общие данные								000 "Герасимов-Проект.К"		

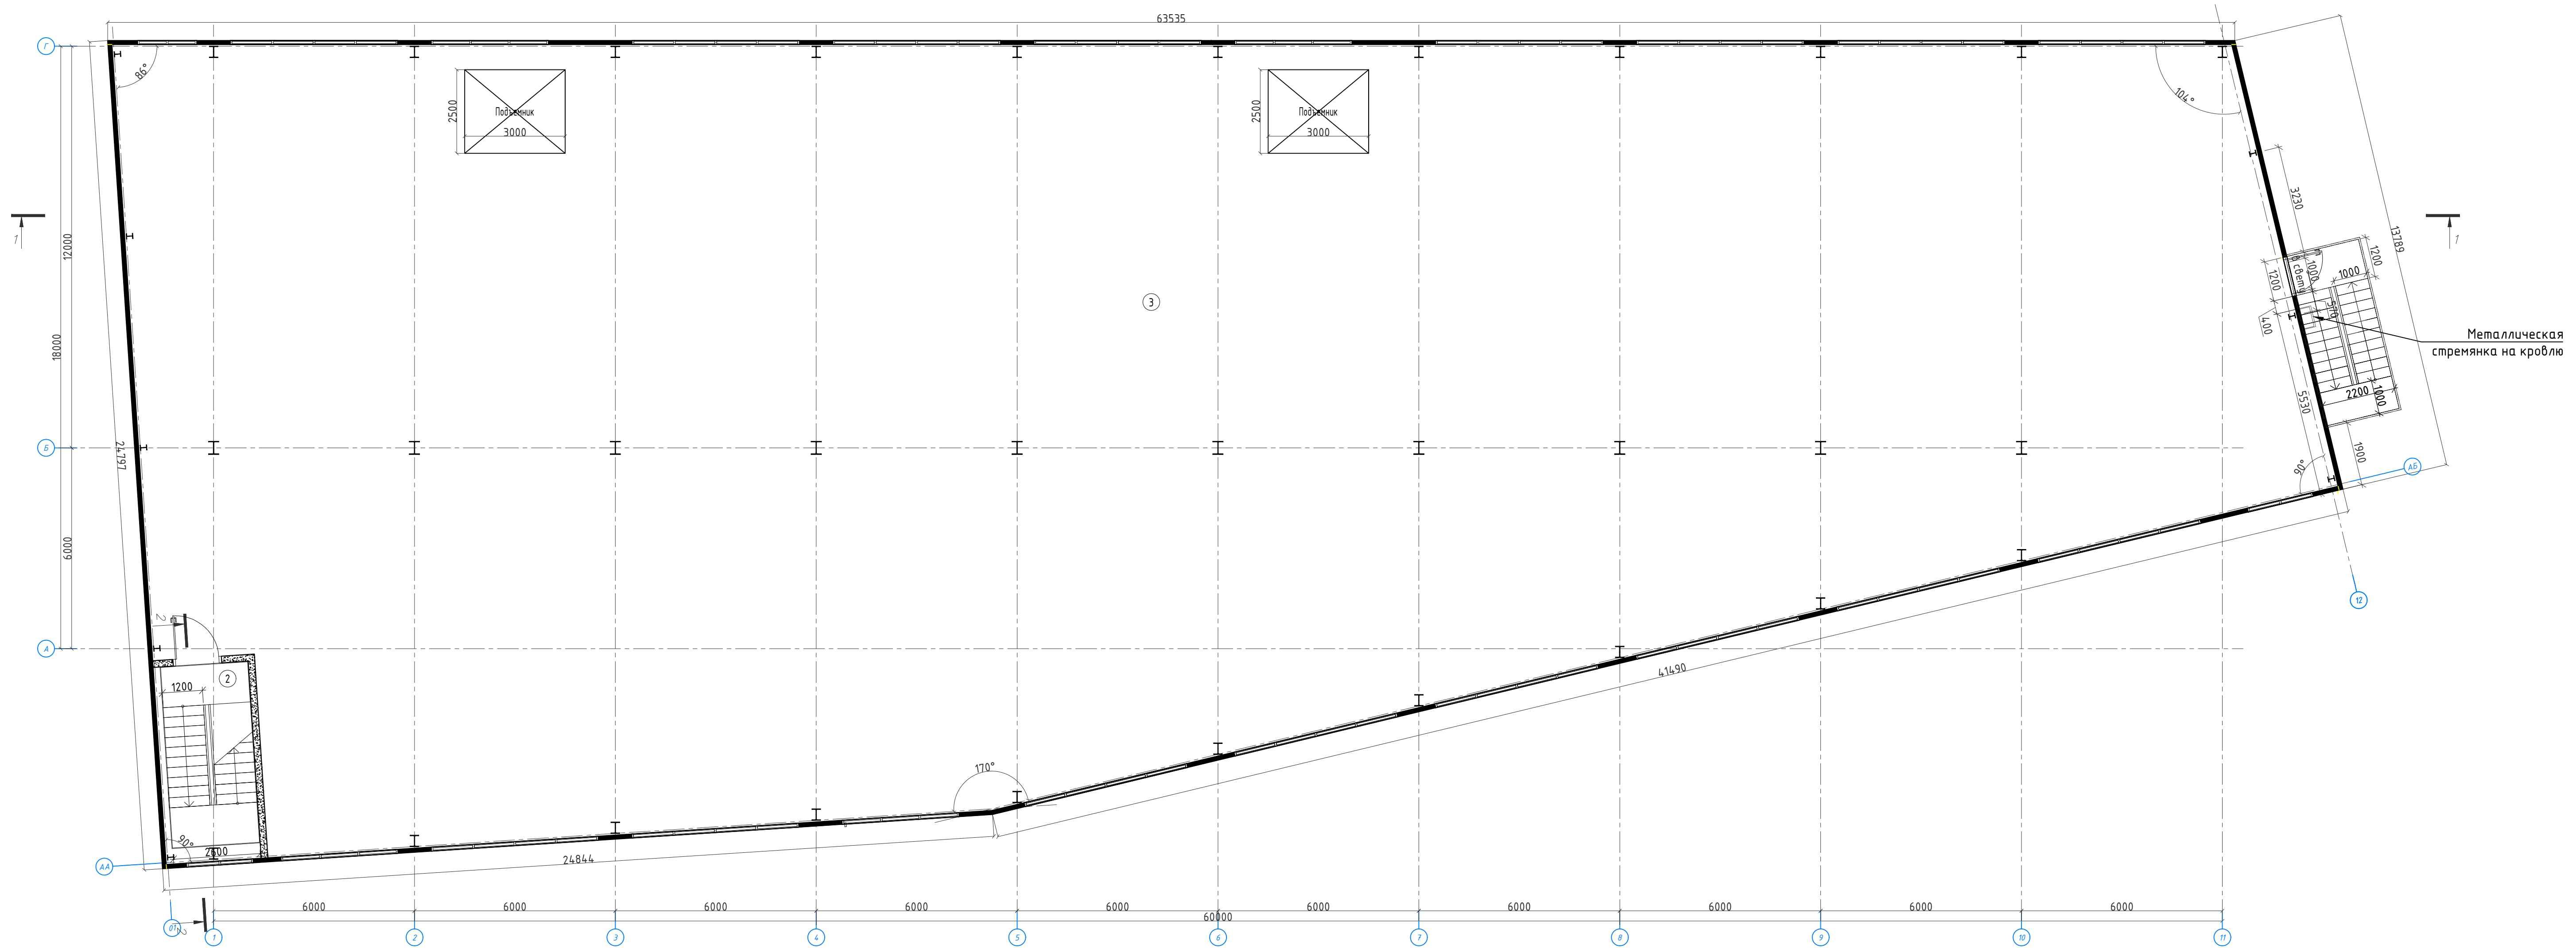
Согласовано

Взам. инв. №

Подп. и дата

Инв. № подл.

План 2 этажа, М 1:100




Экспликация помещений 2 этажа		
№	Состав помещений	Площадь, м ²
3	Склад	1281.60
4	Лестница №1	14.00
Итого		1295.60

						03.04.23-AP			
						Здание склада по адресу: Московская область, д. Глубки, д. 62			
Изм.	Коп.уч.	Лист	№ док.	Подп.	Дата	Архитектурные решения	Стадия	Лист	Листов
ГИП		Герасимов		Евг			П	3	
Исполн.		Танайлов		Евг					
Н. контр.		Герасимов		Евг		План 2 этажа, М 1:100	000 "Герасимов-Проект.К"		

ОПРЕДЕЛЕНИЕ


1418 B. Li et al.

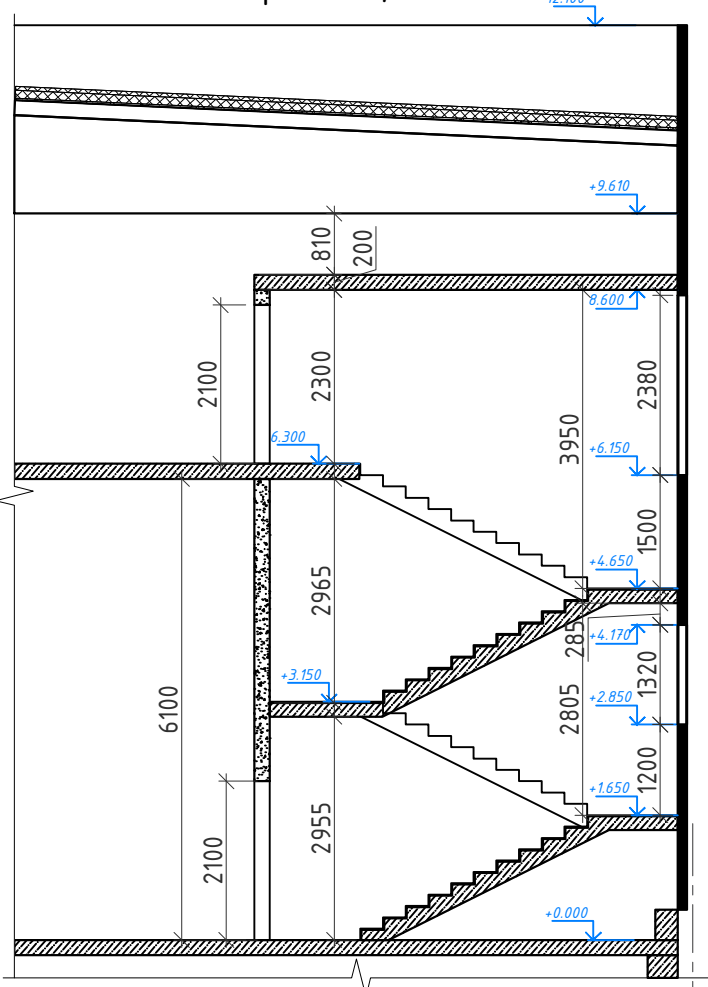Кровельная ПВХ-мембрана PLASTFO/L -1,5мм
Плиты из каменной ваты baswool Р4Ф В -50мм
Уклонообразующий слой из каменной ваты XPS
Плиты из каменной ваты BASWOOL Р4Ф Н -100 мм
Пароизоляционный слой - 4 мм
Профлист




Утеплитель

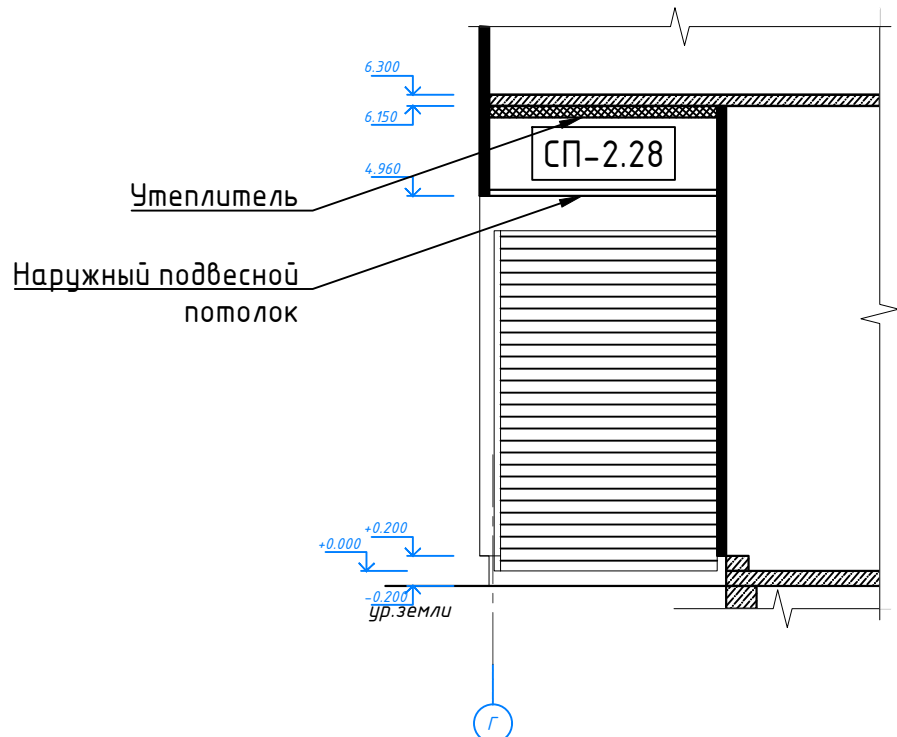Наружный подвесной



ООО "Герасимов-Проект.К"

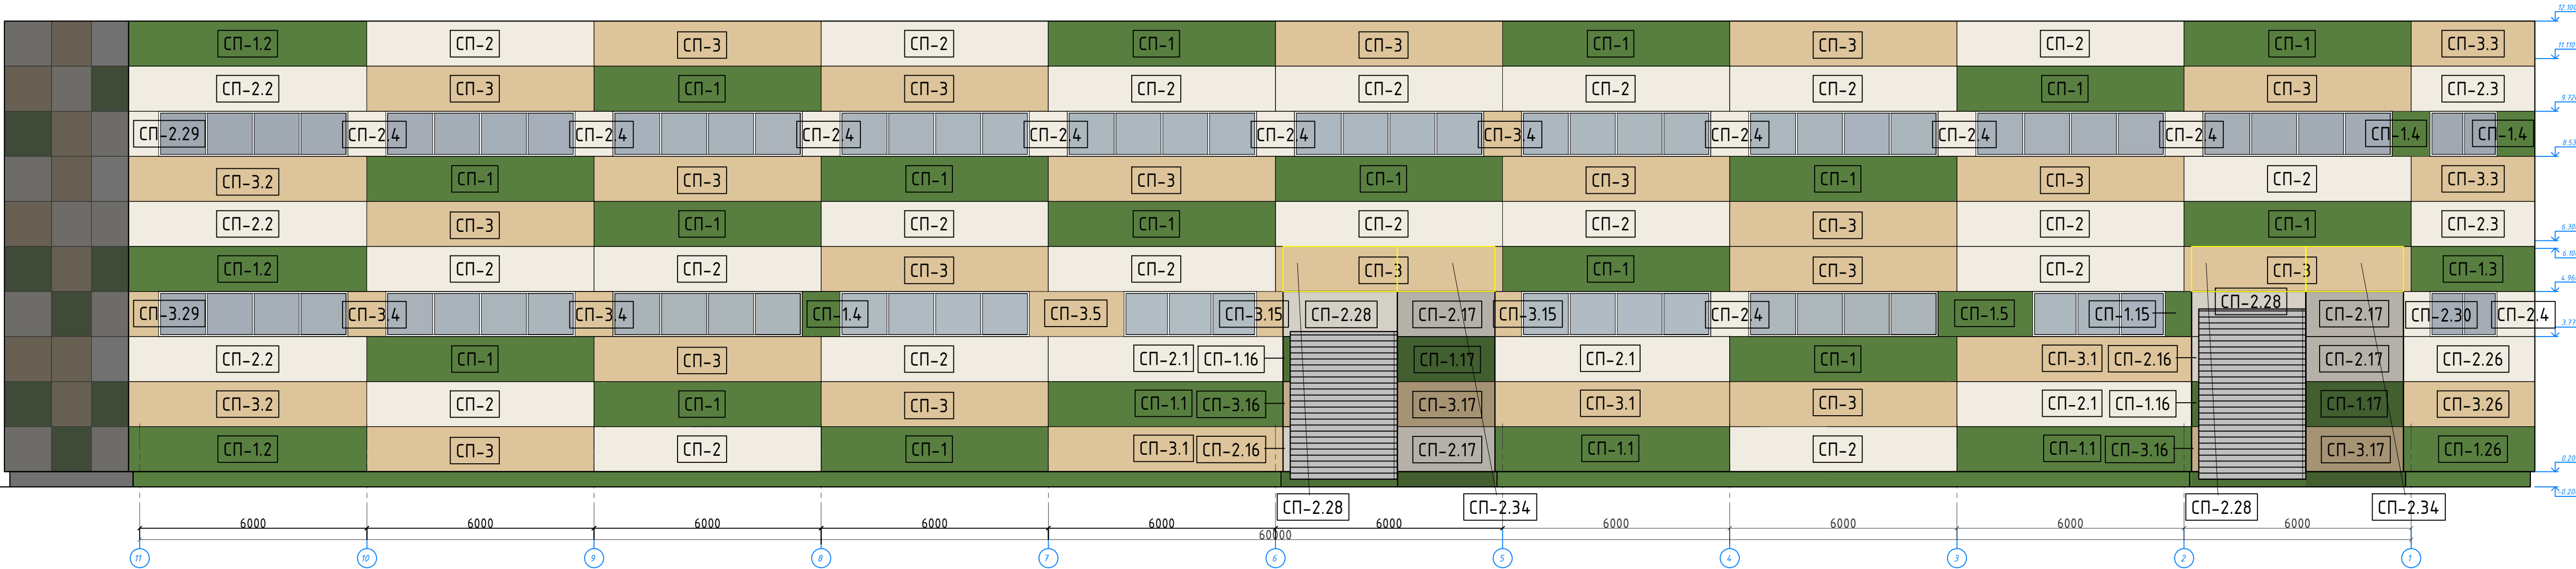Фасад 11-1, М 1:100




Фасад Г-А, М 1:10







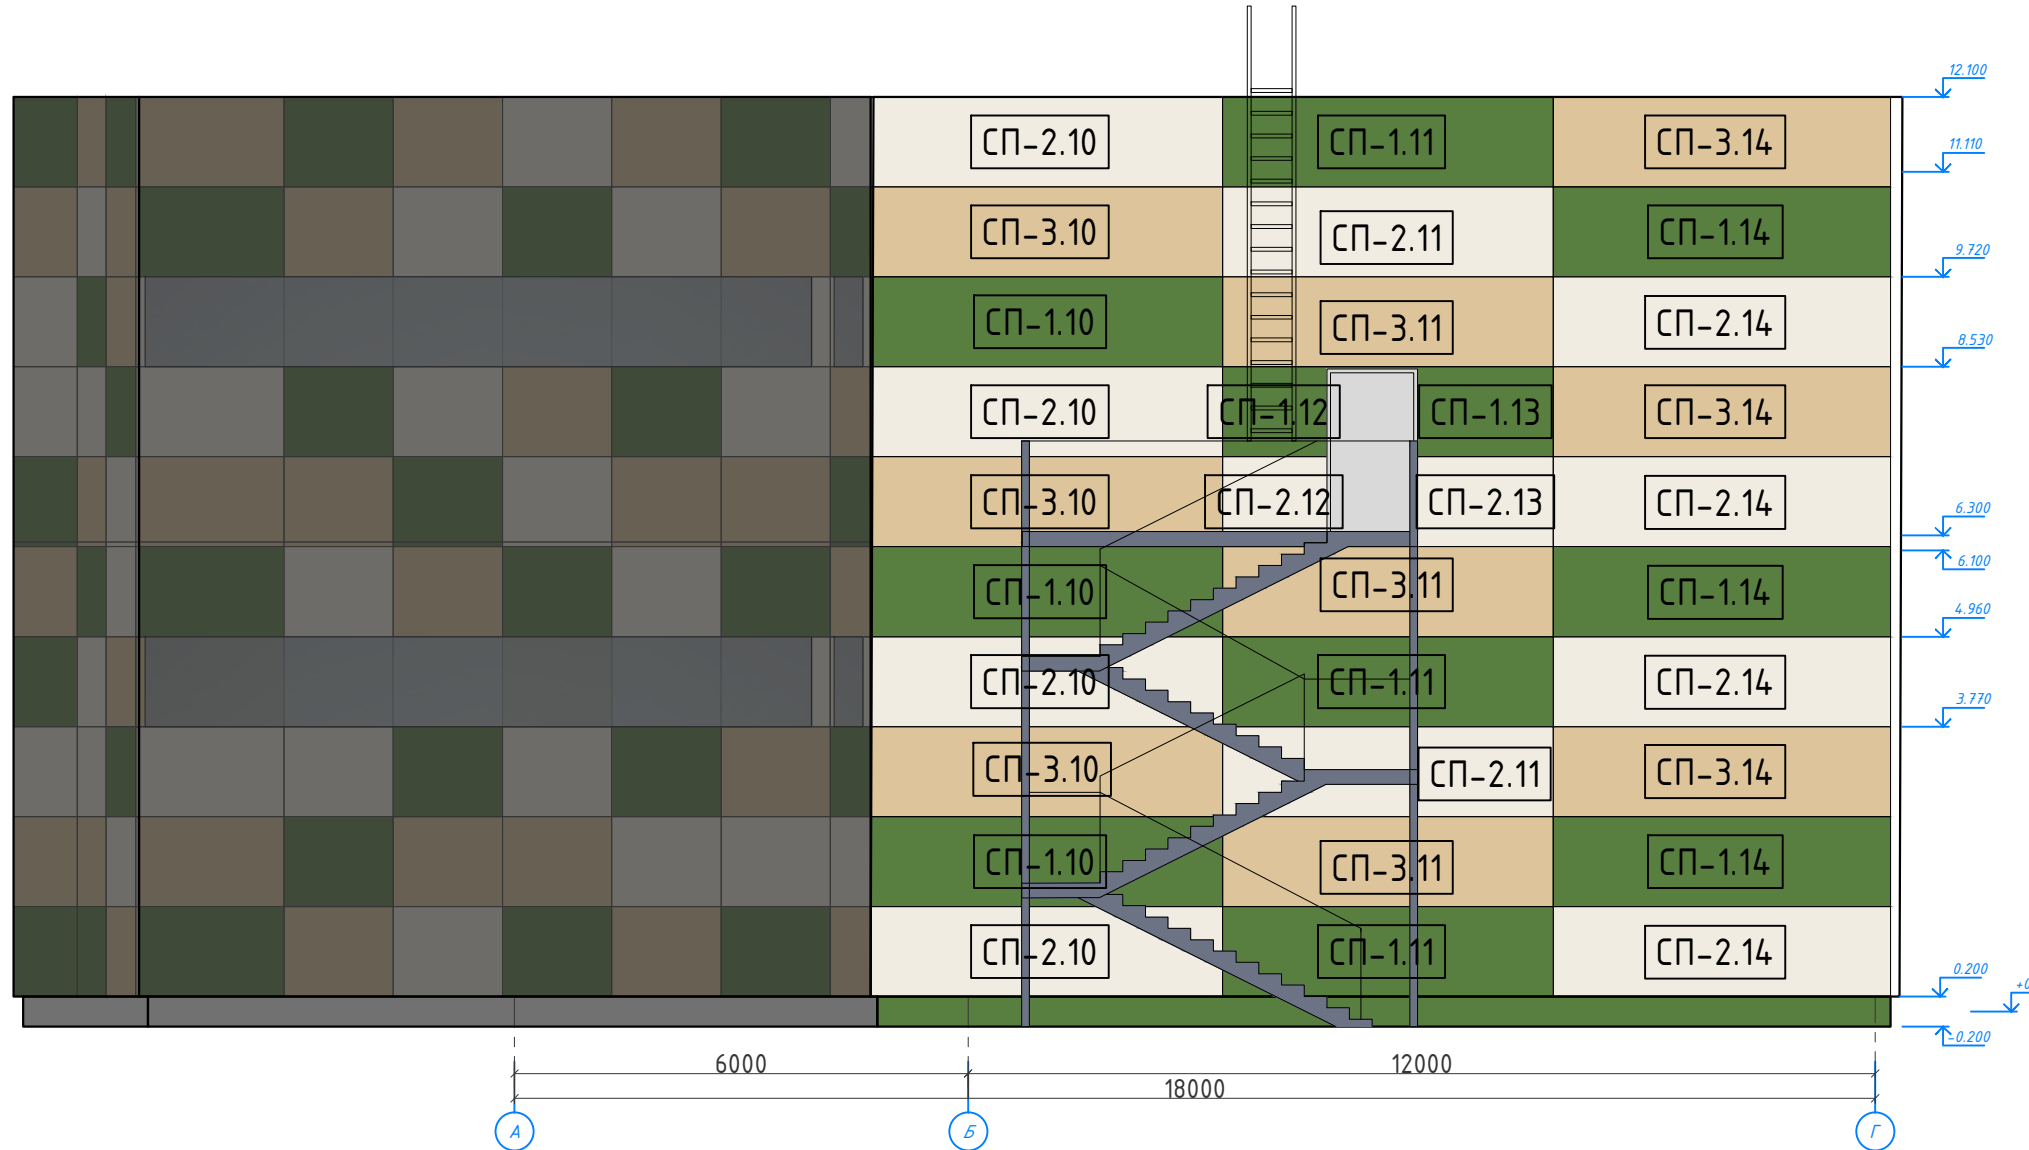
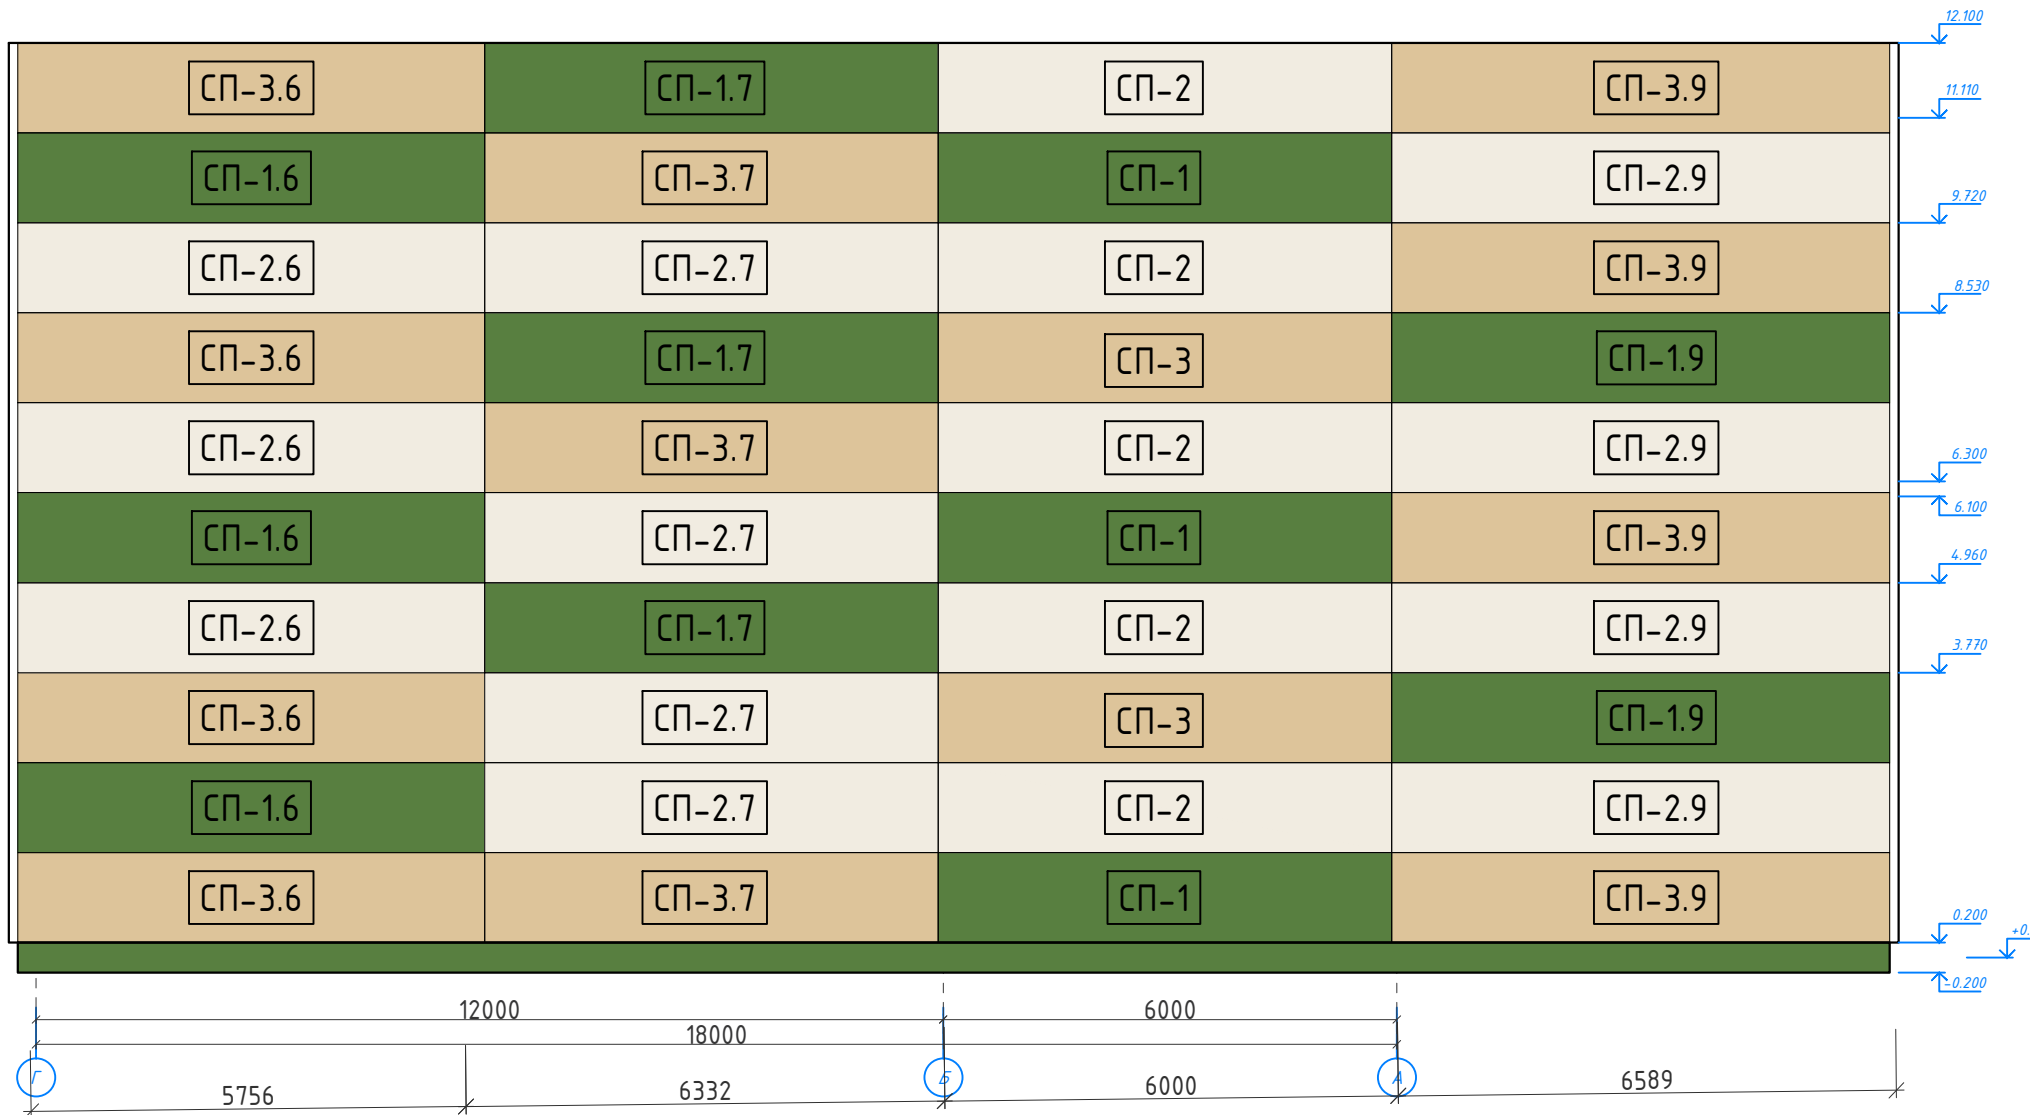
Фасад А-Г, М 1:10




Фасад 1-11, М 1:100

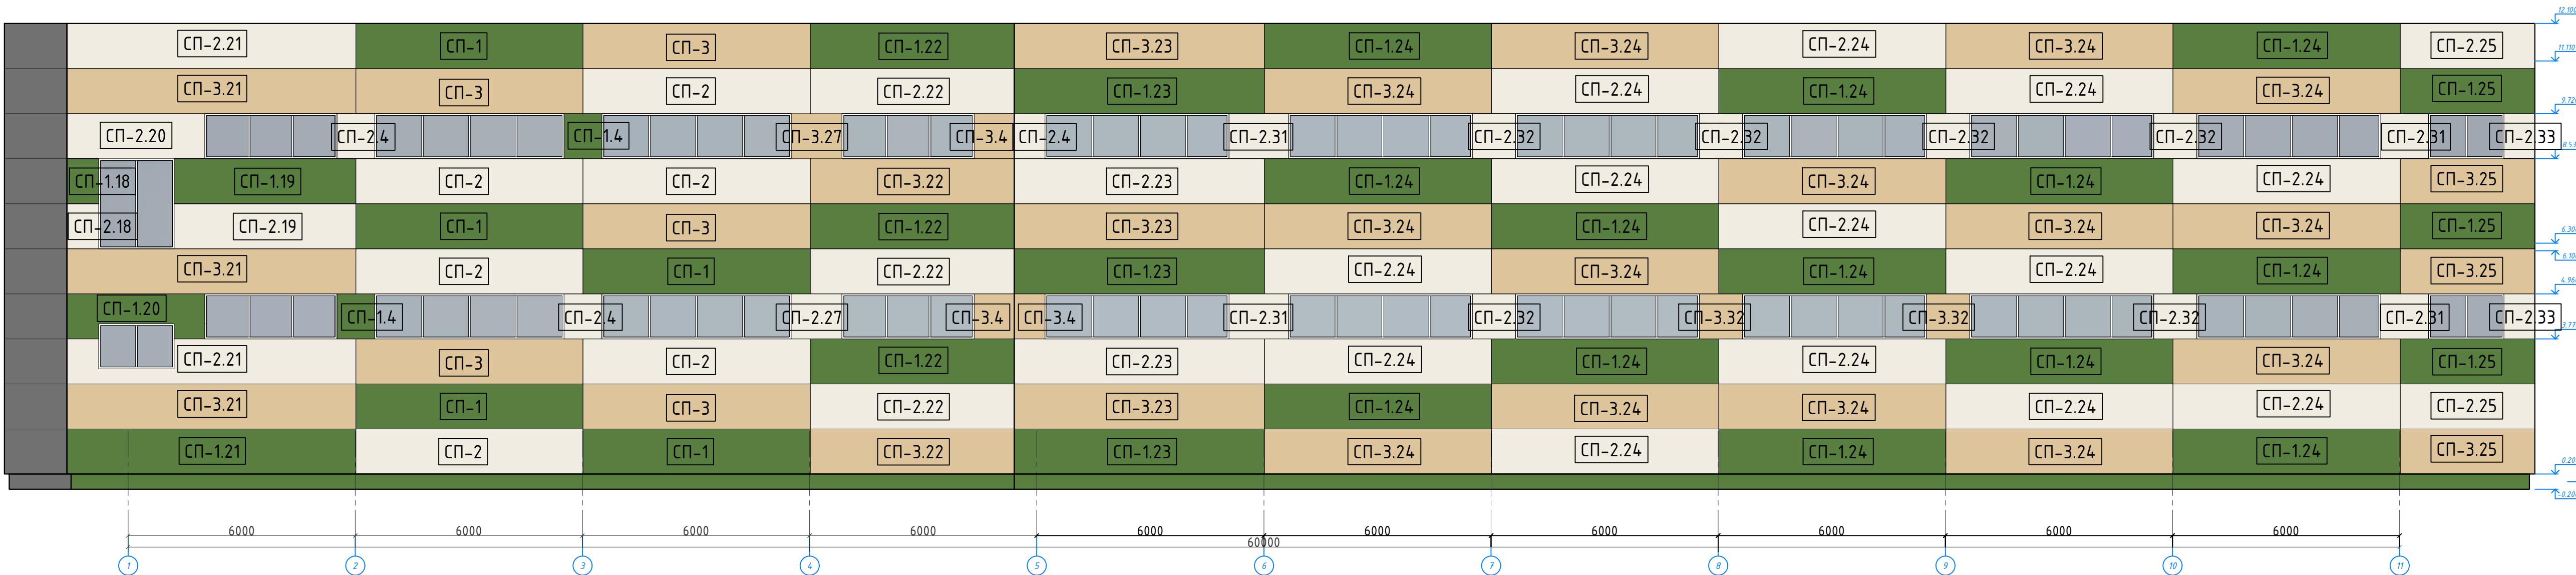

						03.04.23-AP			
						Здание склада по адресу: Московская область, д. Грибки, д. 62			
Изм.	Кол. изм.	Лист	№ док.	Подп.	Дата	Архитектурные решения	Стандия	Лист	Листов
ГИП		Герасимов		Бер			П	5	
Исполн.		Танайлов		Бер		Фасады, М 1:100	000 "Герасимов-Проект.К"		
Н. контр.		Герасимов		Бер					

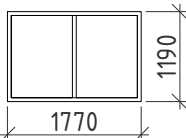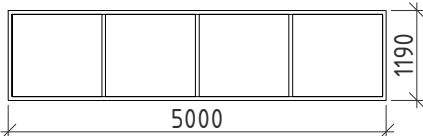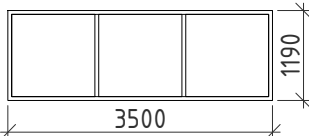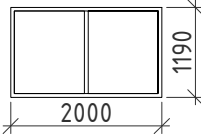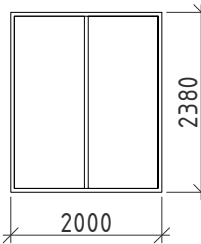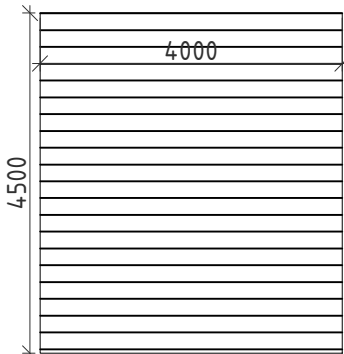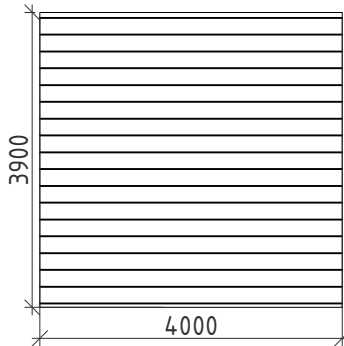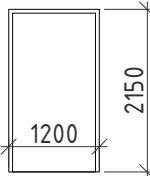				Элементы заполнения наружных проемов															
Марка	Наименование	Эскиз	Размеры проёма, мм		Кол-во, шт.														
			ширина	высота															
ОК1	Оконный блок ПВХ		1770	1190	2														
ОК2	Оконный блок ПВХ		5000	1190	32														
ОК3	Оконный блок ПВХ		3500	1190	6														
ОК4	Оконный блок ПВХ		2000	1190	3														
ОК5	Оконный блок ПВХ		2000	2380	1														
В1	Ворота		4000	4500	1														
В2	Ворота		4000	3900	1														
ДН1	Дверной блок		1200	2150	1														
Согласовано																			
Инв. № подл.																			
Взам. инв. №																			
Подп. и дата																			
Изм.																			
						03.04.23-АР													
						Здание склада по адресу: Московская область, д. Грибки, д. 62													
Изм.		Кол. уч.		Лист		№ док.		Подп.		Дата		Архитектурные решения			Стадия	Лист	Листов		
Исполн.		Танайлов		Подп.		Дата		Н. контр.		Герасимов					7				
Исполн.		Танайлов		Подп.		Дата		Н. контр.		Герасимов		7		Элементы заполнения наружных проемов			ООО "Герасимов-Проект.К"		
Исполн.		Танайлов		Подп.		Дата		Н. контр.		Герасимов		7							

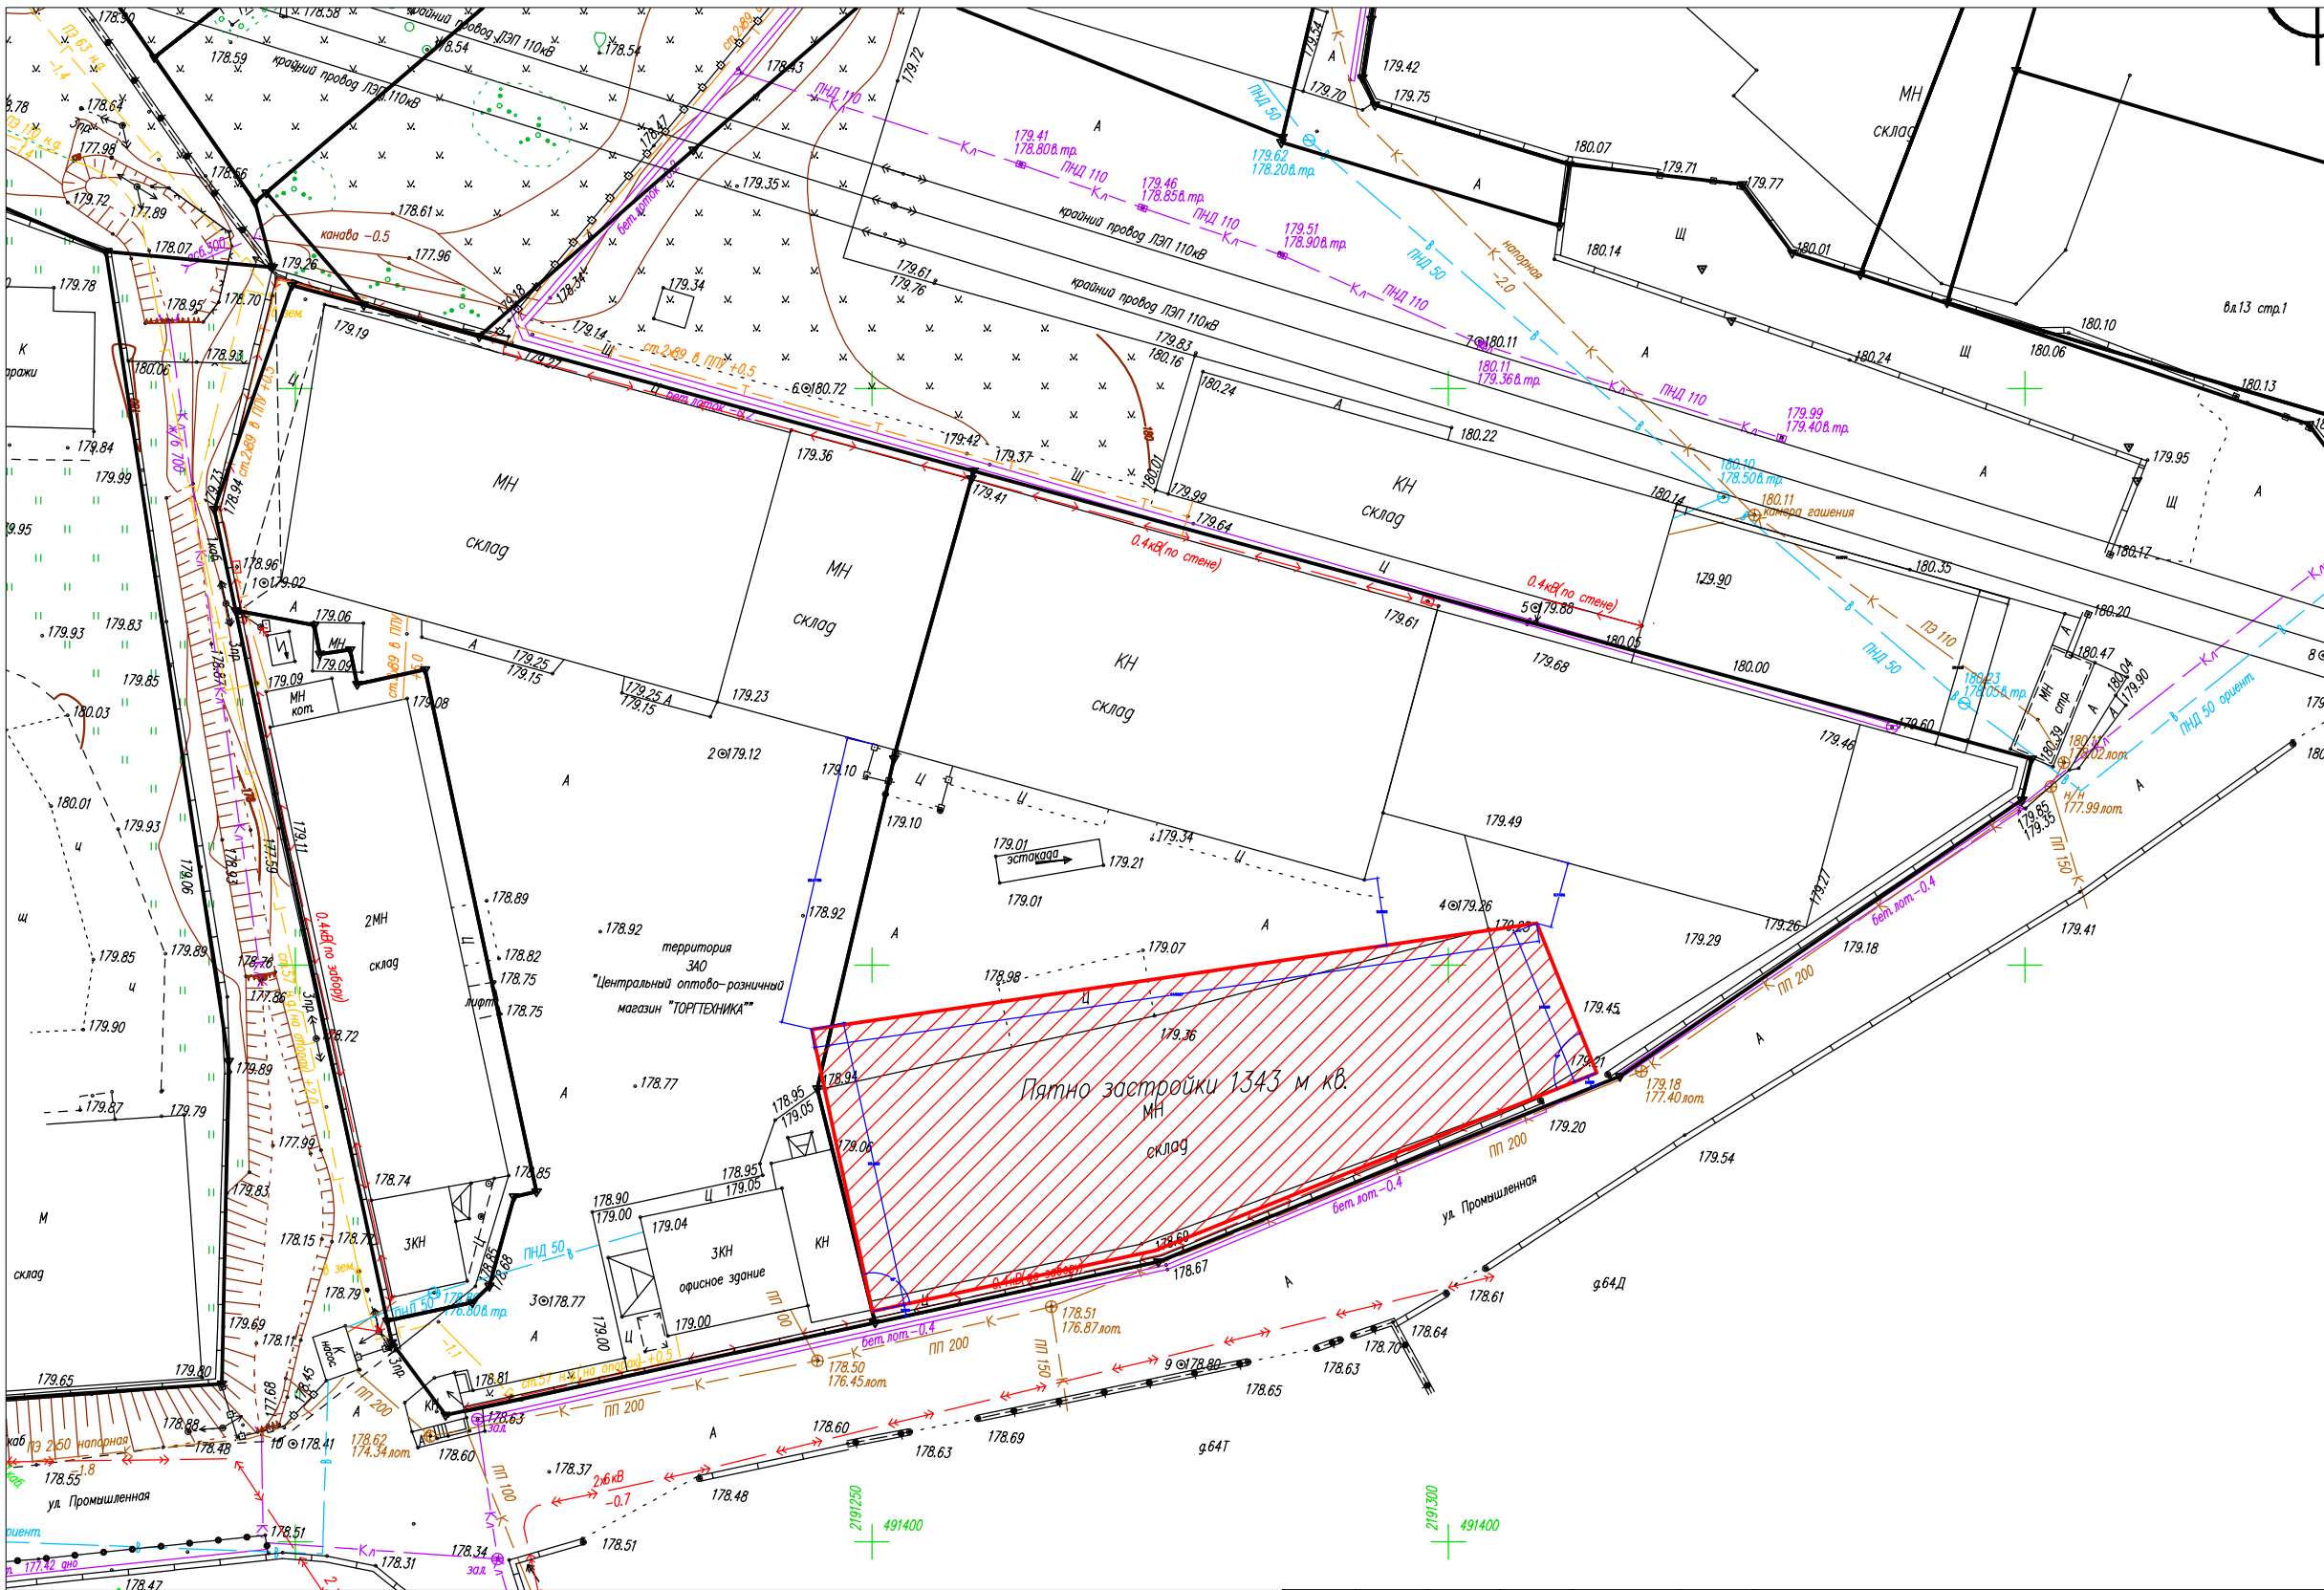

Согласовано	
Взам. инв. №	
Подп. и дата	
Инв. № подл.	

						03.04.23-AP		
						Здание склада по адресу: Московская область, д. Грибки, д. 62		
Изм.	Кол. уч.	Лист	№ док.	Подп.	Дата	Архитектурные решения	Стадия	Лист
ГИП		Герасимов		Евг			П	8
Исполн.		Танайлов		Евг		Схема посадки на участок, М 1:100	ООО "Герасимов-Проект.К"	
Н. контр.		Герасимов		Евг				