

Филиал публично-правовой компании "Роскадастр" по Москве

полное наименование органа регистрации прав

Выписка из Единого государственного реестра недвижимости об объекте недвижимости

Сведения о характеристиках объекта недвижимости

На основании запроса от 09.07.2025, поступившего на рассмотрение 09.07.2025, сообщаем, что согласно записям Единого государственного реестра недвижимости:

Раздел 1 Лист 1

Здание			
вид объекта недвижимости			
Лист № 1 раздела 1	Всего листов раздела 1: 2	Всего разделов: 6	Всего листов выписки: 22
10.07.2025г. № КУВИ-001/2025-137187868			
Кадастровый номер:	77:07:0005009:1051		
Номер кадастрового квартала:	77:07:0005009		
Дата присвоения кадастрового номера:	27.05.2012		
Ранее присвоенный государственный учетный номер:	Инвентарный номер 774/1; Условный номер 141752; Условный номер 2128102 14.02.1992 ГУП МосгорБТИ		
Адрес:	Российская Федерация, город Москва, вн.тер.г. муниципальный округ Филевский парк, проезд Промышленный, дом 3, строение 2		
Площадь:	1571.8		
Назначение:	Нежилое		
Наименование:	Здание		
Количество этажей, в том числе подземных этажей:	2, в том числе подземных 0		
Материал наружных стен:	Кирпичные		
Год ввода в эксплуатацию по завершении строительства:	1970		
Год завершения строительства:	1970		
Кадастровая стоимость, руб.:	61987815.35		
Кадастровые номера иных объектов недвижимости, в пределах которых расположен объект недвижимости:	данные отсутствуют		
Кадастровые номера помещений, машино-мест, расположенных в здании или сооружении:	77:07:0005009:2275, 77:07:0005009:2276, 77:07:0005009:2277, 77:07:0005009:2278, 77:07:0005009:2279, 77:07:0005009:2280, 77:07:0005009:2281, 77:07:0005009:2282, 77:07:0005009:2283, 77:07:0005009:2284, 77:07:0005009:2285, 77:07:0005009:2286, 77:07:0005009:2287, 77:07:0005009:2288		
Кадастровые номера объектов недвижимости, из которых образован объект недвижимости:	данные отсутствуют		
Кадастровые номера образованных объектов недвижимости:	данные отсутствуют		
Сведения о включении объекта недвижимости в состав предприятия как имущественного комплекса:	данные отсутствуют		
Сведения о включении объекта недвижимости в состав единого недвижимого комплекса:	данные отсутствуют		



ДОКУМЕНТ ПОДПИСАН
ЭЛЕКТРОННОЙ ПОДПИСЬЮ

Сертификат: 009F0BDC181A023B64597F1E2579BEFB50

Владелец: ФЕДЕРАЛЬНАЯ СЛУЖБА ГОСУДАРСТВЕННОЙ
РЕГИСТРАЦИИ, КАДАСТРА И КАРТОГРАФИИ
Действителен: с 02.08.2024 по 26.10.2025

полное наименование должности

инициалы, фамилия

Здание			
вид объекта недвижимости			
Лист № 2 раздела 1	Всего листов раздела 1: 2	Всего разделов: 6	Всего листов выписки: 22
10.07.2025г. № КУВИ-001/2025-137187868			
Кадастровый номер:		77:07:0005009:1051	
Виды разрешенного использования:		данные отсутствуют	
Сведения о включении объекта недвижимости в реестр объектов культурного наследия:		данные отсутствуют	
Сведения о кадастровом инженере:		дата завершения кадастровых работ: 14.02.2003	
Сведения о признании многоквартирного дома аварийным и подлежащим сносу или реконструкции и (или) о признании жилого помещения, в том числе жилого дома, непригодным для проживания:		данные отсутствуют	
Статус записи об объекте недвижимости:		Сведения об объекте недвижимости имеют статус "актуальные, ранее учтенные"	
Особые отметки:		Сведения, необходимые для заполнения раздела: 6 - Сведения о частях объекта недвижимости, отсутствуют.	
Получатель выписки:		Киор Юрий Анатольевич	

полное наименование должности	 ДОКУМЕНТ ПОДПИСАН ЭЛЕКТРОННОЙ ПОДПИСЬЮ Сертификат: 009F0BDC181A023B64597F1E2579BEFB50 Владелец: ФЕДЕРАЛЬНАЯ СЛУЖБА ГОСУДАРСТВЕННОЙ РЕГИСТРАЦИИ, КАДАСТРА И КАРТОГРАФИИ Действителен: с 02.08.2024 по 26.10.2025	инициалы, фамилия

Выписка из Единого государственного реестра недвижимости об объекте недвижимости
Сведения о зарегистрированных правах

Здание			
вид объекта недвижимости			
Лист № 1 раздела 2		Всего листов раздела 2: 2	Всего разделов: 6
Всего листов выписки: 22			
10.07.2025г. № КУВИ-001/2025-137187868			
Кадастровый номер:		77:07:0005009:1051	
1	Правообладатель (правообладатели):	1.1	Федеральное государственное бюджетное учреждение "Дирекция по обеспечению деятельности федерального агентства по управлению государственным имуществом", ИНН: 7722467407
	Сведения о возможности предоставления третьим лицам персональных данных физического лица:	1.1.1	данные отсутствуют
2	Вид, номер, дата и время государственной регистрации права:	2.1	Оперативное управление 77:07:0005009:1051-77/051/2021-1 26.03.2021 17:43:20
3	Сведения об осуществлении государственной регистрации сделки, права без необходимого в силу закона согласия третьего лица, органа:	3.1	данные отсутствуют
4	Ограничение прав и обременение объекта недвижимости: не зарегистрировано		
1	Правообладатель (правообладатели):	1.2	Российская Федерация
	Сведения о возможности предоставления третьим лицам персональных данных физического лица:	1.2.1	данные отсутствуют
2	Вид, номер, дата и время государственной регистрации права:	2.2	Собственность 77-77-13/005/2008-649 25.03.2008 00:00:00
3	Сведения об осуществлении государственной регистрации сделки, права без необходимого в силу закона согласия третьего лица, органа:	3.2	данные отсутствуют
4	Ограничение прав и обременение объекта недвижимости: не зарегистрировано		
5	Договоры участия в долевом строительстве: не зарегистрировано		
6	Заявленные в судебном порядке права требования: данные отсутствуют		
7	Сведения о возможности предоставления третьим лицам персональных данных физического лица: данные отсутствуют		
8	Сведения о возражении в отношении зарегистрированного права: данные отсутствуют		
9	Сведения о наличии решения об изъятии объекта недвижимости для государственных и муниципальных нужд: данные отсутствуют		


полное наименование должности	 ДОКУМЕНТ ПОДПИСАН ЭЛЕКТРОННОЙ ПОДПИСЬЮ Сертификат: 009F0BDC181A023B64597F1E2579BEFB50 Владелец: ФЕДЕРАЛЬНАЯ СЛУЖБА ГОСУДАРСТВЕННОЙ РЕГИСТРАЦИИ, КАДАСТРА И КАРТОГРАФИИ Действителен: с 02.08.2024 по 26.10.2025	инициалы, фамилия

Здание			
вид объекта недвижимости			
Лист № 2 раздела 2	Всего листов раздела 2: 2	Всего разделов: 6	Всего листов выписки: 22
10.07.2025г. № КУВИ-001/2025-137187868			
Кадастровый номер:		77:07:0005009:1051	
10	Сведения о невозможности государственной регистрации без личного участия правообладателя или его законного представителя:	данные отсутствуют	
11	Правопритязания и сведения о наличии поступивших, но не рассмотренных заявлений о проведении государственной регистрации права (перехода, прекращения права), ограничения права или обременения объекта недвижимости, сделки в отношении объекта недвижимости:	отсутствуют	

полное наименование должности	 ДОКУМЕНТ ПОДПИСАН ЭЛЕКТРОННОЙ ПОДПИСЬЮ Сертификат: 009F0BDC181A023B64597F1E2579BEFB50 Владелец: ФЕДЕРАЛЬНАЯ СЛУЖБА ГОСУДАРСТВЕННОЙ РЕГИСТРАЦИИ, КАДАСТРА И КАРТОГРАФИИ Действителен: с 02.08.2024 по 26.10.2025	инициалы, фамилия

Выписка из Единого государственного реестра недвижимости об объекте недвижимости
Описание местоположения объекта недвижимости

Здание			
вид объекта недвижимости			
Лист № 1 раздела 5	Всего листов раздела 5: 1	Всего разделов: 6	Всего листов выписки: 22
10.07.2025г. № КУВИ-001/2025-137187868			
Кадастровый номер:		77:07:0005009:1051	

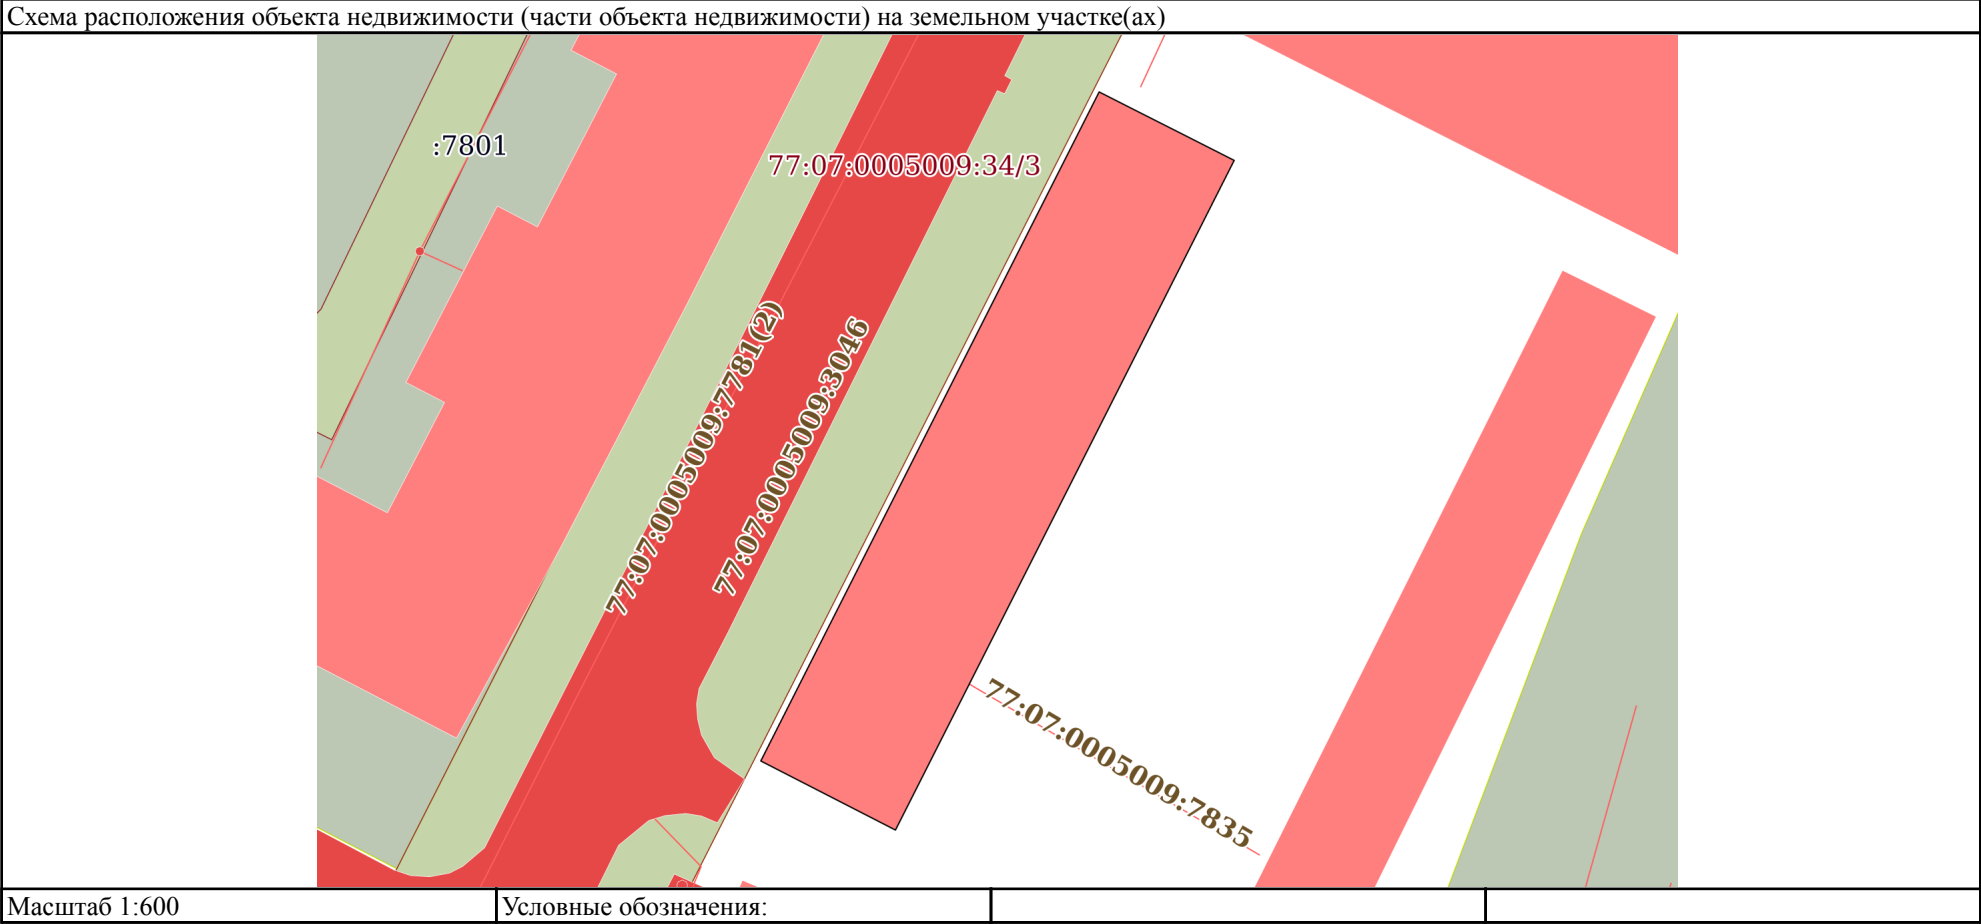

полное наименование должности	 ДОКУМЕНТ ПОДПИСАН ЭЛЕКТРОННОЙ ПОДПИСЬЮ Сертификат: 009F0BDC181A023B64597F1E2579BEFB50 Владелец: ФЕДЕРАЛЬНАЯ СЛУЖБА ГОСУДАРСТВЕННОЙ РЕГИСТРАЦИИ, КАДАСТРА И КАРТОГРАФИИ Действителен: с 02.08.2024 по 26.10.2025	инициалы, фамилия

Выписка из Единого государственного реестра недвижимости об объекте недвижимости
Описание местоположения объекта недвижимости

Здание			
вид объекта недвижимости			
Лист № 1 раздела 5.1	Всего листов раздела 5.1: 2	Всего разделов: 6	Всего листов выписки: 22
10.07.2025г. № КУВИ-001/2025-137187868			
Кадастровый номер:		77:07:0005009:1051	

1. Сведения о координатах характерных точек контура объекта недвижимости						
Система координат ПМСК Москвы						
Номер точки	Координаты, м		Радиус, м	Средняя квадратическая погрешность определения координат характерных точек контура, м	Глубина, высота, м	
	X	Y			H1	H2
1	2	3	4	5	6	7
1	8595.23	882.84	-	-	данные отсутствуют	данные отсутствуют
2	8589.68	893.67	-	-	данные отсутствуют	данные отсутствуют
3	8643.49	920.91	-	-	данные отсутствуют	данные отсутствуют
4	8645.66	916.63	-	-	данные отсутствуют	данные отсутствуют
5	8647.51	912.97	-	-	данные отсутствуют	данные отсутствуют
6	8648.99	910.05	-	-	данные отсутствуют	данные отсутствуют
1	8595.23	882.84	-	-	данные отсутствуют	данные отсутствуют
2. Сведения о предельных высоте и глубине конструктивных элементов объекта недвижимости						
Предельная глубина конструктивных элементов объекта недвижимости, м				данные отсутствуют		
Предельная высота конструктивных элементов объекта недвижимости, м				данные отсутствуют		

полное наименование должности	 ДОКУМЕНТ ПОДПИСАН ЭЛЕКТРОННОЙ ПОДПИСЬЮ Сертификат: 009F0BDC181A023B64597F1E2579BEFB50 Владелец: ФЕДЕРАЛЬНАЯ СЛУЖБА ГОСУДАРСТВЕННОЙ РЕГИСТРАЦИИ, КАДАСТРА И КАРТОГРАФИИ Действителен: с 02.08.2024 по 26.10.2025	инициалы, фамилия

Здание							
вид объекта недвижимости							
Лист № 2 раздела 5.1		Всего листов раздела 5.1: 2		Всего разделов: 6		Всего листов выписки: 22	
10.07.2025г. № КУВИ-001/2025-137187868							
Кадастровый номер:				77:07:0005009:1051			
3. Сведения о характерных точках пересечения контура объекта недвижимости с контуром (контурами) иных зданий, сооружений, объектов незавершенного строительства							
Система координат ПМСК Москвы							
Номера характерных точек контура	Координаты, м		Средняя квадратическая погрешность определения координат характерных точек контура, м	Глубина, высота, м		Кадастровые номера иных объектов недвижимости, с контурами которых пересекается контур данного объекта недвижимости	
	X	Y		N1	N2		
1	2	3	4	5	6	7	
данные отсутствуют	данные отсутствуют	данные отсутствуют	данные отсутствуют	данные отсутствуют	данные отсутствуют	данные отсутствуют	

полное наименование должности	 ДОКУМЕНТ ПОДПИСАН ЭЛЕКТРОННОЙ ПОДПИСЬЮ Сертификат: 009F0BDC181A023B64597F1E2579BEFB50 Владелец: ФЕДЕРАЛЬНАЯ СЛУЖБА ГОСУДАРСТВЕННОЙ РЕГИСТРАЦИИ, КАДАСТРА И КАРТОГРАФИИ Действителен: с 02.08.2024 по 26.10.2025	инициалы, фамилия

Выписка из Единого государственного реестра недвижимости об объекте недвижимости
Перечень помещений, машино-мест, расположенных в здании, сооружении

Здание			
вид объекта недвижимости			
Лист № 1 раздела 7	Всего листов раздела 7: 1	Всего разделов: 6	Всего листов выписки: 22
10.07.2025г. № КУВИ-001/2025-137187868			
Кадастровый номер:		77:07:0005009:1051	

N п/п	Кадастровый номер помещения, машино-места	Номер этажа (этажей)	Обозначение (номер) помещения, машино-места на поэтажном плане	Назначение помещения	Вид разрешенного использования	Площадь, м2
1	77:07:0005009:2275	1	2128102/0001	Нежилое	данные отсутствуют	182.9
2	77:07:0005009:2276	1	2128102/0002	Нежилое	данные отсутствуют	26.5
3	77:07:0005009:2277	1	2128102/0003	Нежилое	данные отсутствуют	54.2
4	77:07:0005009:2278	1	2128102/0004	Нежилое	данные отсутствуют	16.3
5	77:07:0005009:2279	1	2128102/0005	Нежилое	данные отсутствуют	12.2
6	77:07:0005009:2280	1	2128102/0006	Нежилое	данные отсутствуют	3.8
7	77:07:0005009:2281	1	2128102/0007	Нежилое	данные отсутствуют	45.5
8	77:07:0005009:2282	1	2128102/0008	Нежилое	данные отсутствуют	193.9
9	77:07:0005009:2283	1	2128102/0009	Нежилое	данные отсутствуют	154.6
10	77:07:0005009:2284	1	2128102/0010	Нежилое	данные отсутствуют	42.1
11	77:07:0005009:2285	1	2128102/0011	Нежилое	данные отсутствуют	43.2
12	77:07:0005009:2286	2	2128102/0012	Нежилое	данные отсутствуют	670.3
13	77:07:0005009:2287	0	2128102/0013	Нежилое	данные отсутствуют	64.8
14	77:07:0005009:2288	0	2128102/0014	Нежилое	данные отсутствуют	61.5

полное наименование должности		инициалы, фамилия
	ДОКУМЕНТ ПОДПИСАН ЭЛЕКТРОННОЙ ПОДПИСЬЮ	
	Сертификат: 009F0BDC181A023B64597F1E2579BEFB50 Владелец: ФЕДЕРАЛЬНАЯ СЛУЖБА ГОСУДАРСТВЕННОЙ РЕГИСТРАЦИИ, КАДАСТРА И КАРТОГРАФИИ Действителен: с 02.08.2024 по 26.10.2025	

Здание			
вид объекта недвижимости			
Лист № 3 раздела 8	Всего листов раздела 8: 14	Всего разделов: 6	Всего листов выписки: 22
10.07.2025г. № КУВИ-001/2025-137187868			
Кадастровый номер: 77:07:0005009:1051		Номер этажа (этажей): 1	

ПОЭТАЖНЫЙ ПЛАН


по адресу: Промышленный проезд

домовл.(вл.) дом 3

корпус строения (сооружение) 2

квартал № 774 Западного АО г.Москвы

1 этаж

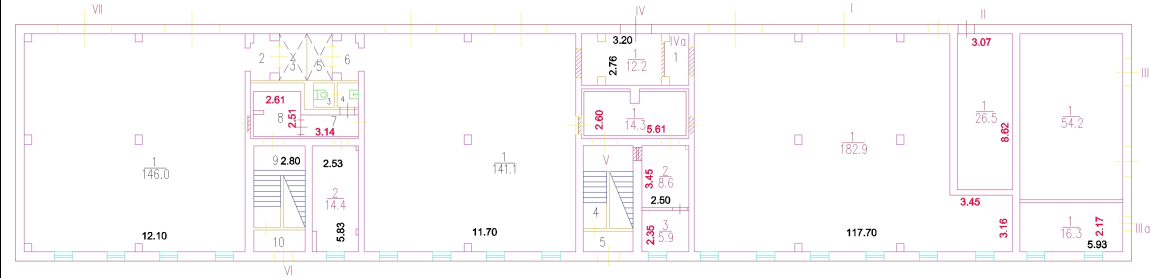

Масштаб 1:200

Разрешение на произведенное переоборудование

В лок. № 11(111) №(1) №(1) №(1)

Территориальному бюро технической инвентаризации не представлено

14 февраля 2003г.

Исполнитель

Проверил

Масштаб 1

полное наименование должности	ДОКУМЕНТ ПОДПИСАН ЭЛЕКТРОННОЙ ПОДПИСЬЮ Сертификат: 009F0BDC181A023B64597F1E2579BEFB50 Владелец: ФЕДЕРАЛЬНАЯ СЛУЖБА ГОСУДАРСТВЕННОЙ РЕГИСТРАЦИИ, КАДАСТРА И КАРТОГРАФИИ Действителен: с 02.08.2024 по 26.10.2025	инициалы, фамилия

Здание			
вид объекта недвижимости			
Лист № 5 раздела 8	Всего листов раздела 8: 14	Всего разделов: 6	Всего листов выписки: 22
10.07.2025г. № КУВИ-001/2025-137187868			
Кадастровый номер: 77:07:0005009:1051		Номер этажа (этажей): 1	

ПОЭТАЖНЫЙ ПЛАН


по адресу: Промышленный проезд

домовл.(вл.) дом 3

корпус строения (сооружение) 2

квартал № 774 Западного АО г.Москвы

1 этаж

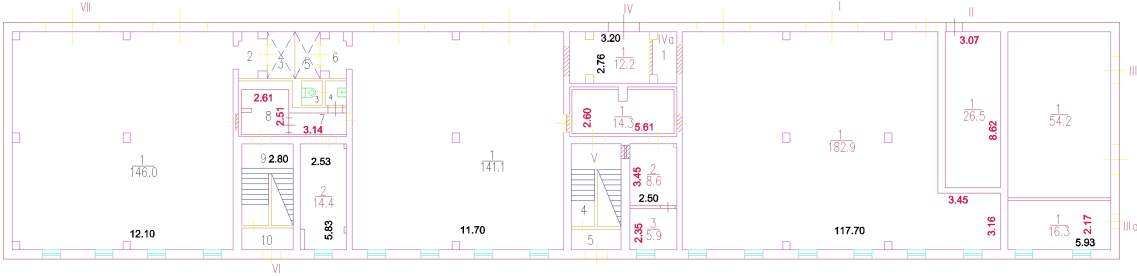

Масштаб 1:200

Разрешение на произведенное переоборудование

В лок. № 11(111) №(1) №(1) №(1)

Территориальному бюро технической инвентаризации не представлено

14 февраля 2003г.

Исполнитель

Проверил

Масштаб 1

полное наименование должности	ДОКУМЕНТ ПОДПИСАН ЭЛЕКТРОННОЙ ПОДПИСЬЮ Сертификат: 009F0BDC181A023B64597F1E2579BEFB50 Владелец: ФЕДЕРАЛЬНАЯ СЛУЖБА ГОСУДАРСТВЕННОЙ РЕГИСТРАЦИИ, КАДАСТРА И КАРТОГРАФИИ Действителен: с 02.08.2024 по 26.10.2025	инициалы, фамилия

Здание			
вид объекта недвижимости			
Лист № 7 раздела 8	Всего листов раздела 8: 14	Всего разделов: 6	Всего листов выписки: 22
10.07.2025г. № КУВИ-001/2025-137187868			
Кадастровый номер: 77:07:0005009:1051		Номер этажа (этажей): 1	

ПОЭТАЖНЫЙ ПЛАН


по адресу: Промышленный проезд

домовл.(вл.) дом 3

корпус строения (сооружение) 2

квартал № 774 Западного АО г.Москвы

1 этаж

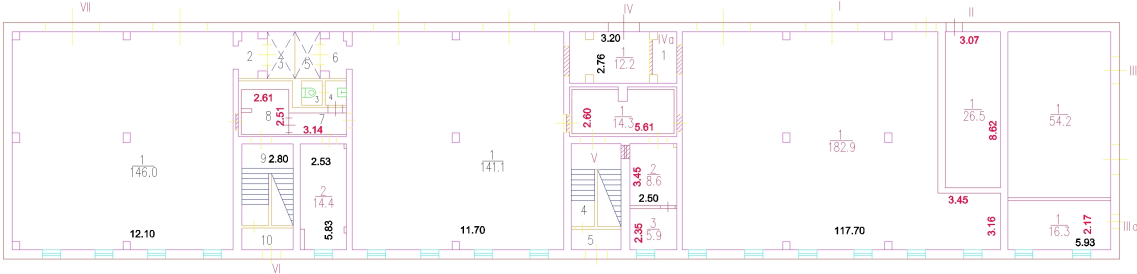

Масштаб 1:200

Разрешение на произведенное переоборудование

В лок. № 11(111) №(1) №(1) №(1)

Территориальному бюро технической инвентаризации не представлено

14 февраля 2003г.

Исполнитель

Проверил

Масштаб 1

полное наименование должности	ДОКУМЕНТ ПОДПИСАН ЭЛЕКТРОННОЙ ПОДПИСЬЮ Сертификат: 009F0BDC181A023B64597F1E2579BEFB50 Владелец: ФЕДЕРАЛЬНАЯ СЛУЖБА ГОСУДАРСТВЕННОЙ РЕГИСТРАЦИИ, КАДАСТРА И КАРТОГРАФИИ Действителен: с 02.08.2024 по 26.10.2025	инициалы, фамилия

Здание			
вид объекта недвижимости			
Лист № 8 раздела 8	Всего листов раздела 8: 14	Всего разделов: 6	Всего листов выписки: 22
10.07.2025г. № КУВИ-001/2025-137187868			
Кадастровый номер: 77:07:0005009:1051		Номер этажа (этажей): 1	

ПОЭТАЖНЫЙ ПЛАН


по адресу: Промышленный проезд

домовл.(вл.) дом 3

корпус строения (сооружение) 2

квартал № 774 Западного АО г.Москвы

1 этаж

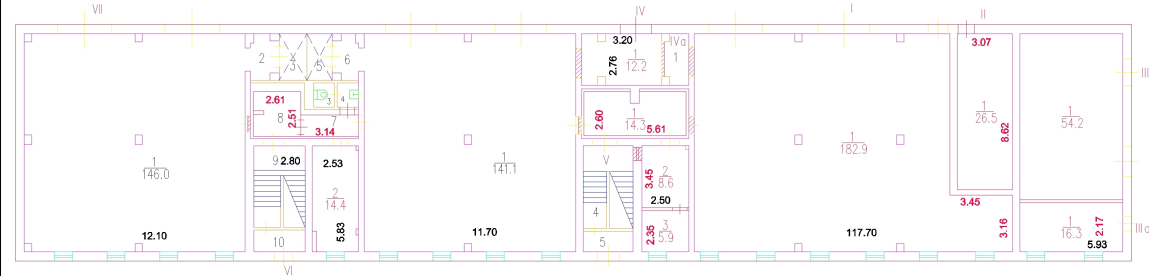

Масштаб 1:200

Разрешение на произведенное переоборудование

В лок. № 11(111) №(1) №(1) №(1)

Территориальному бюро технической инвентаризации не представлено

14 февраля 2003г.

Исполнитель


Проверил

Масштаб 1

полное наименование должности	ДОКУМЕНТ ПОДПИСАН ЭЛЕКТРОННОЙ ПОДПИСЬЮ Сертификат: 009F0BDC181A023B64597F1E2579BEFB50 Владелец: ФЕДЕРАЛЬНАЯ СЛУЖБА ГОСУДАРСТВЕННОЙ РЕГИСТРАЦИИ, КАДАСТРА И КАРТОГРАФИИ Действителен: с 02.08.2024 по 26.10.2025	инициалы, фамилия

Здание			
вид объекта недвижимости			
Лист № 10 раздела 8	Всего листов раздела 8: 14	Всего разделов: 6	Всего листов выписки: 22
10.07.2025г. № КУВИ-001/2025-137187868			
Кадастровый номер: 77:07:0005009:1051		Номер этажа (этажей): 1	

антресоль 1 этажа
Промышленный проезд д.3 стр.2

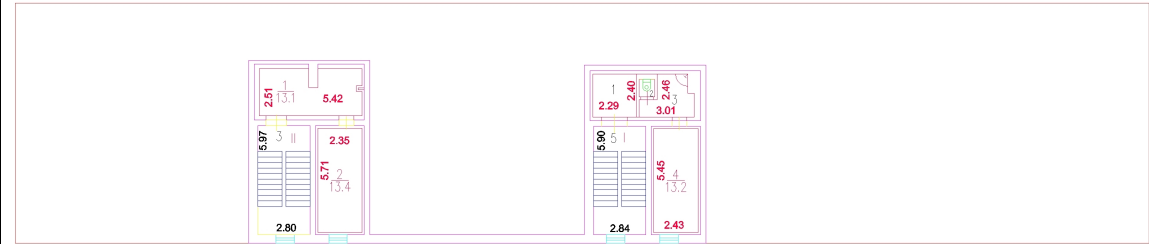

Масштаб 1:200


Разрешение на произве-
денное переоборудование
В ^{кадр.} № ^{пол.} 1/234/112
Территориальному бюро
технической инвентариза-
ции не представлено
" 14 " февраля 2003г.
Исполнитель _____
Проверил _____

Масштаб 1

полное наименование должности	 ДОКУМЕНТ ПОДПИСАН ЭЛЕКТРОННОЙ ПОДПИСЬЮ Сертификат: 009F0BDC181A023B64597F1E2579BEFB50 Владелец: ФЕДЕРАЛЬНАЯ СЛУЖБА ГОСУДАРСТВЕННОЙ РЕГИСТРАЦИИ, КАДАСТРА И КАРТОГРАФИИ Действителен: с 02.08.2024 по 26.10.2025	инициалы, фамилия

Здание			
вид объекта недвижимости			
Лист № 11 раздела 8	Всего листов раздела 8: 14	Всего разделов: 6	Всего листов выписки: 22
10.07.2025г. № КУВИ-001/2025-137187868			
Кадастровый номер: 77:07:0005009:1051		Номер этажа (этажей): 1	

антресоль 1 этажа
Промышленный проезд д.3 стр.2

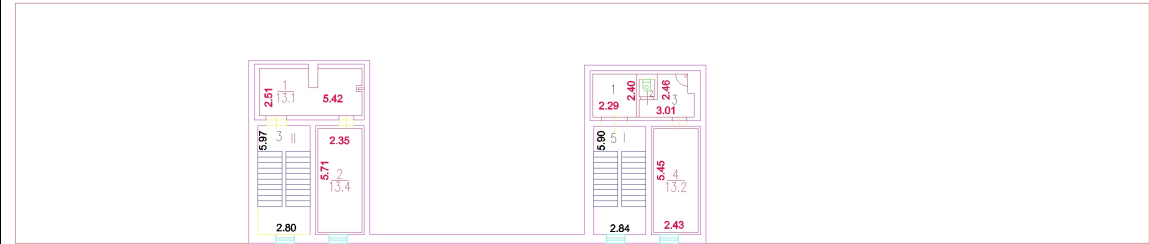


Масштаб 1:200

Разрешение на произве-
денное переоборудование
В ^{кадр.} № ^{пол.} 1/234/112
Территориальному бюро
технической инвентариза-
ции не представлено
" 14 " февраля 2003г.
Исполнитель _____
Проверил _____

Масштаб 1

		ДОКУМЕНТ ПОДПИСАН ЭЛЕКТРОННОЙ ПОДПИСЬЮ	
полное наименование должности		Сертификат: 009F0BDC181A023B64597F1E2579BEFB50 Владелец: ФЕДЕРАЛЬНАЯ СЛУЖБА ГОСУДАРСТВЕННОЙ РЕГИСТРАЦИИ, КАДАСТРА И КАРТОГРАФИИ Действителен: с 02.08.2024 по 26.10.2025	инициалы, фамилия


Здание			
вид объекта недвижимости			
Лист № 12 раздела 8	Всего листов раздела 8: 14	Всего разделов: 6	Всего листов выписки: 22
10.07.2025г. № КУВИ-001/2025-137187868			
Кадастровый номер: 77:07:0005009:1051		Номер этажа (этажей): 2	

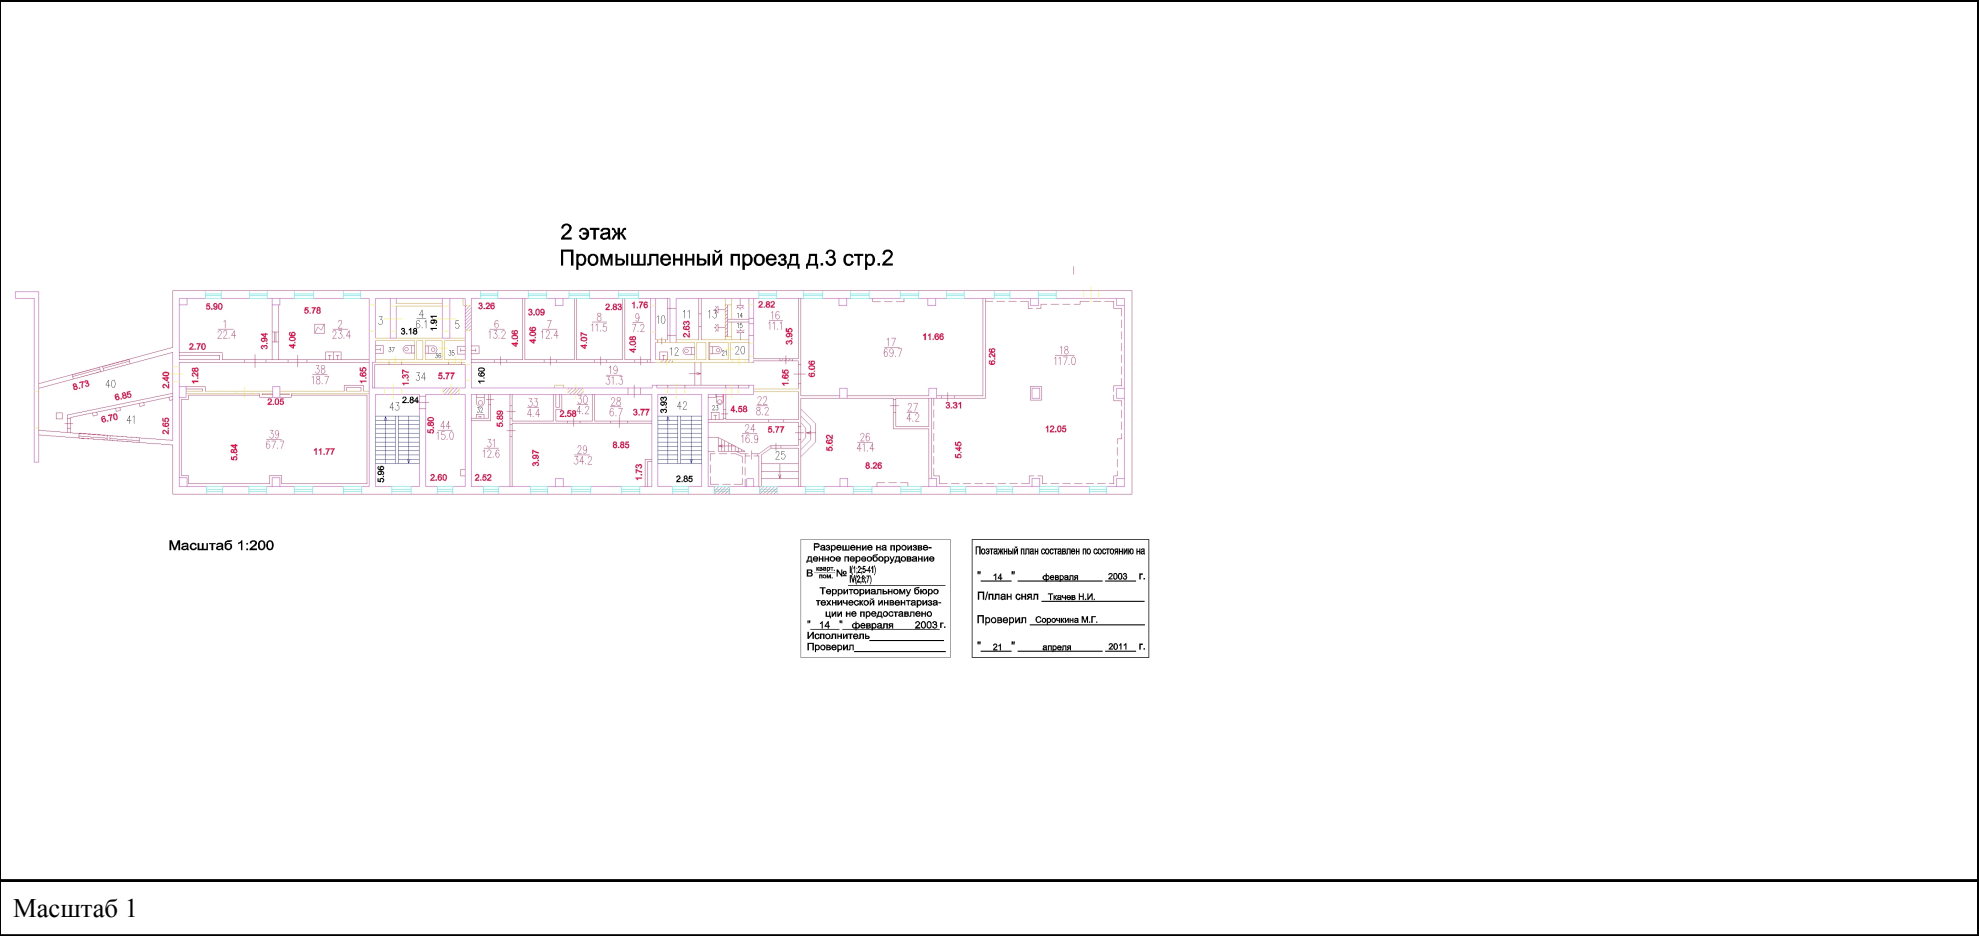

полное наименование должности	 ДОКУМЕНТ ПОДПИСАН ЭЛЕКТРОННОЙ ПОДПИСЬЮ Сертификат: 009F0BDC181A023B64597F1E2579BEFB50 Владелец: ФЕДЕРАЛЬНАЯ СЛУЖБА ГОСУДАРСТВЕННОЙ РЕГИСТРАЦИИ, КАДАСТРА И КАРТОГРАФИИ Действителен: с 02.08.2024 по 26.10.2025	инициалы, фамилия

Здание			
вид объекта недвижимости			
Лист № 13 раздела 8	Всего листов раздела 8: 14	Всего разделов: 6	Всего листов выписки: 22
10.07.2025г. № КУВИ-001/2025-137187868			
Кадастровый номер: 77:07:0005009:1051		Номер этажа (этажей): 0	

надстройка
Промышленный проезд д.3 стр.2

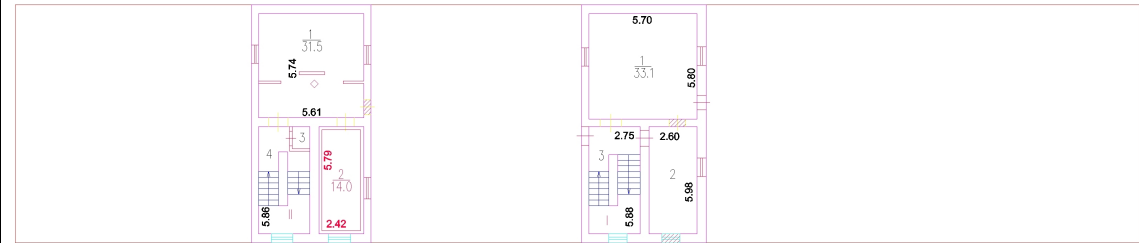

Масштаб 1:200

Разрешение на произве-
денное переоборудование
В "квар." № 1(234) и(12)
Территориальному бюро
технической инвента-
ризации не предоставлено
" 14 " февраля 2003г.
Исполнитель _____
Проверил _____

Переналожен камерально
Потажный план составлен по состоянию на
" 14 " февраля 2003 г.
П/план снял Ткачев Н.И.
Проверил Сорочанна М.Г.
" 19 " апреля 2011 г.

Масштаб 1



ДОКУМЕНТ ПОДПИСАН
ЭЛЕКТРОННОЙ ПОДПИСЬЮ


Сертификат: 009F0BDC181A023B64597F1E2579BEFB50
Владелец: ФЕДЕРАЛЬНАЯ СЛУЖБА ГОСУДАРСТВЕННОЙ
РЕГИСТРАЦИИ, КАДАСТРА И КАРТОГРАФИИ
Действителен: с 02.08.2024 по 26.10.2025

полное наименование должности

инициалы, фамилия

Здание			
вид объекта недвижимости			
Лист № 14 раздела 8	Всего листов раздела 8: 14	Всего разделов: 6	Всего листов выписки: 22
10.07.2025г. № КУВИ-001/2025-137187868			
Кадастровый номер: 77:07:0005009:1051		Номер этажа (этажей): 0	

надстройка
Промышленный проезд д.3 стр.2

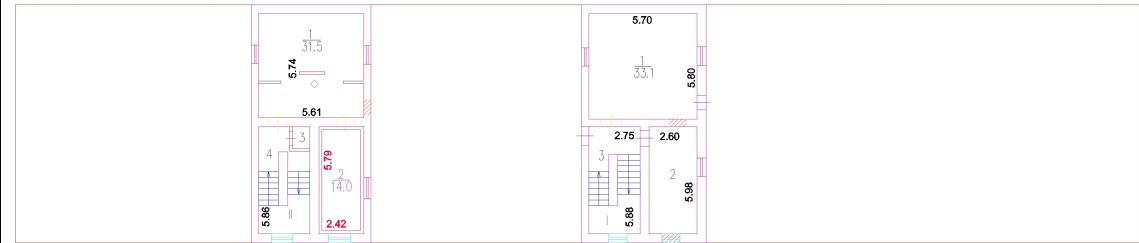

Масштаб 1:200

Разрешение на произве-
денное переоборудование
В "квар." № 1(234) и(12)
Территориальному бюро
технической инвента-
ризации не предоставлено
" 14 " февраля 2003г.
Исполнитель _____
Проверил _____

Переналожен камерально
Потажный план составлен по состоянию на
" 14 " февраля 2003 г.
П/план снял Ткачев Н.И.
Проверил Сорочанна М.Г.
" 19 " апреля 2011 г.

Масштаб 1



ДОКУМЕНТ ПОДПИСАН
ЭЛЕКТРОННОЙ ПОДПИСЬЮ

Сертификат: 009F0BDC181A023B64597F1E2579BEFB50
Владелец: ФЕДЕРАЛЬНАЯ СЛУЖБА ГОСУДАРСТВЕННОЙ
РЕГИСТРАЦИИ, КАДАСТРА И КАРТОГРАФИИ
Действителен: с 02.08.2024 по 26.10.2025

полное наименование должности	инициалы, фамилия
-------------------------------	-------------------