



Акционерное общество

«Российский государственный центр инвентаризации и учета объектов недвижимости -
Федеральное БТИ»

(полное наименование ОТИ - организации технического учета и технической инвентаризации объектов капитального строительства)

Производственный участок "Ейский" Южного филиала АО "Ростехинвентаризация-Федеральное БТИ"
(наименование обособленного подразделения ОТИ)

ТЕХНИЧЕСКИЙ ПАСПОРТ

На _____ здание
(вид объекта учета)

Складской корпус. 4 этап строительства
(наименование объекта учета)

Адрес (местоположение) объекта учета:

Субъект Российской Федерации	Краснодарский край	
Район	Ейский	
Муниципальное образование	тип	
	наименование	
Населенный пункт	тип	город
	наименование	Ейск
Улица (проспект, переулок и т.д.)	тип	улица
	наименование	Щорса
Номер дома	53/4	
Номер корпуса		
Номер строения		
Литера	Д	
Иное описание местоположения		

Инв. №4123

Штамп органа государственного технического учета о внесении сведений
в Единый государственный реестр объектов капитального строительства (ЕГРОКС)

Наименование учетного органа	
Инвентарный номер	
Кадастровый номер	
Дата внесения сведений в ЕГРОКС	

Паспорт составлен по состоянию на « 01 » _____ марта 20 19 _____ года


Руководитель (уполномоченное лицо) ОТИ _____

М.П.

(подпись)

Мокшина И.Б.

(Фамилия И.О.)

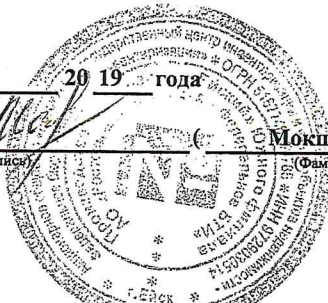

I. РЕГИСТРАЦИЯ ПРАВА СОБСТВЕННОСТИ

[illegible]


II. ЭКСПЛИКАЦИЯ ЗЕМЕЛЬНОГО УЧАСТКА - КВ. М

Площадь участка			Незастроенная площадь					
по документам	фактически	застроенная	замошенная	озелененная	прочая	грунт		
20000	20000	4381.6	-	-	-	-		

II. Благоустройство полезной площади (кв. м)

[illegible]

СИТУАЦИОННЫЙ ПЛАН

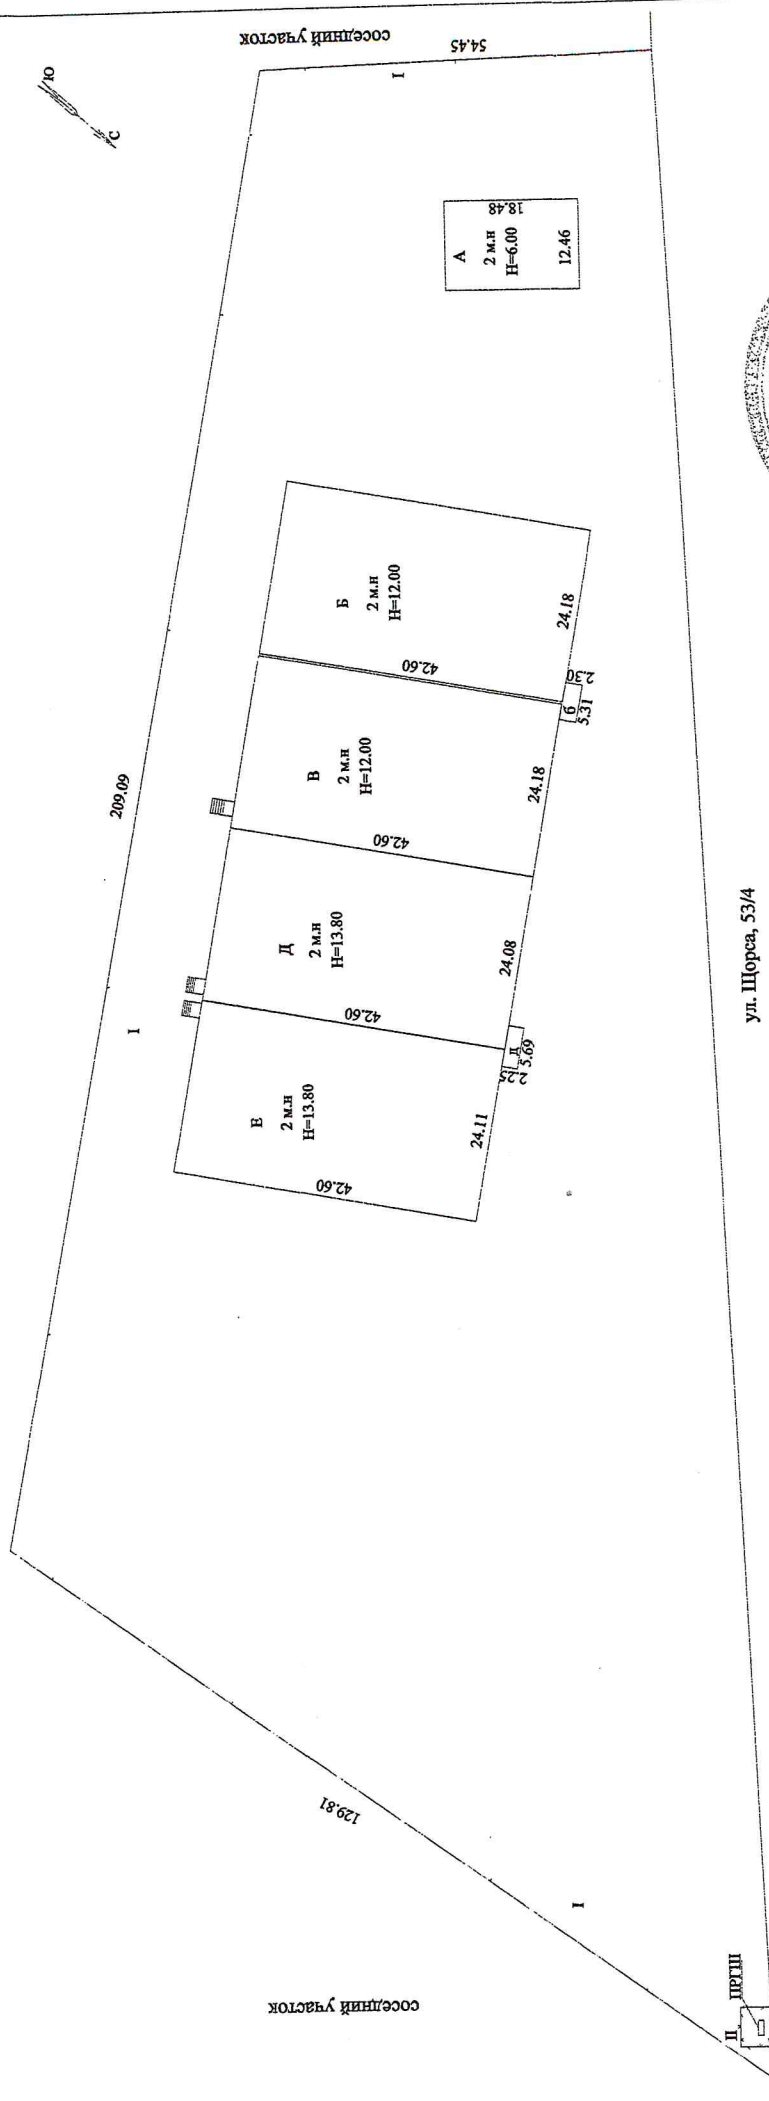

ул. Щорса, 53/4



Производственный участок "БТИ" Южного филиала
АО "Ростехинвентаризация - Федеральное БТИ"

Начальник отделения: 01.03.2019г.	Мокшина И.Б.	Лист 1
Проверил: 01.03.2019г.	Мокшина И.Б.	Листов 1
Исполнитель: 01.03.2019г.	Бутенко А.В.	Масштаб 1:1000

Краснодарский край,
г. Ейск, ул. Щорса, 53/4

IV. Общие сведения

Назначение	Нежилое
Использование	по назначению
Количество (мощность)	1159.5 м2


Примечание:

Примечание:
Площадь здания в пределах внутренних поверхностей наружных стен -1177,6 м2

V. Исчисление площадей и объемов зданий и его частей (подвалов, полуподвалов и пристроек)


[illegible]

Поэтажный план
1 этаж

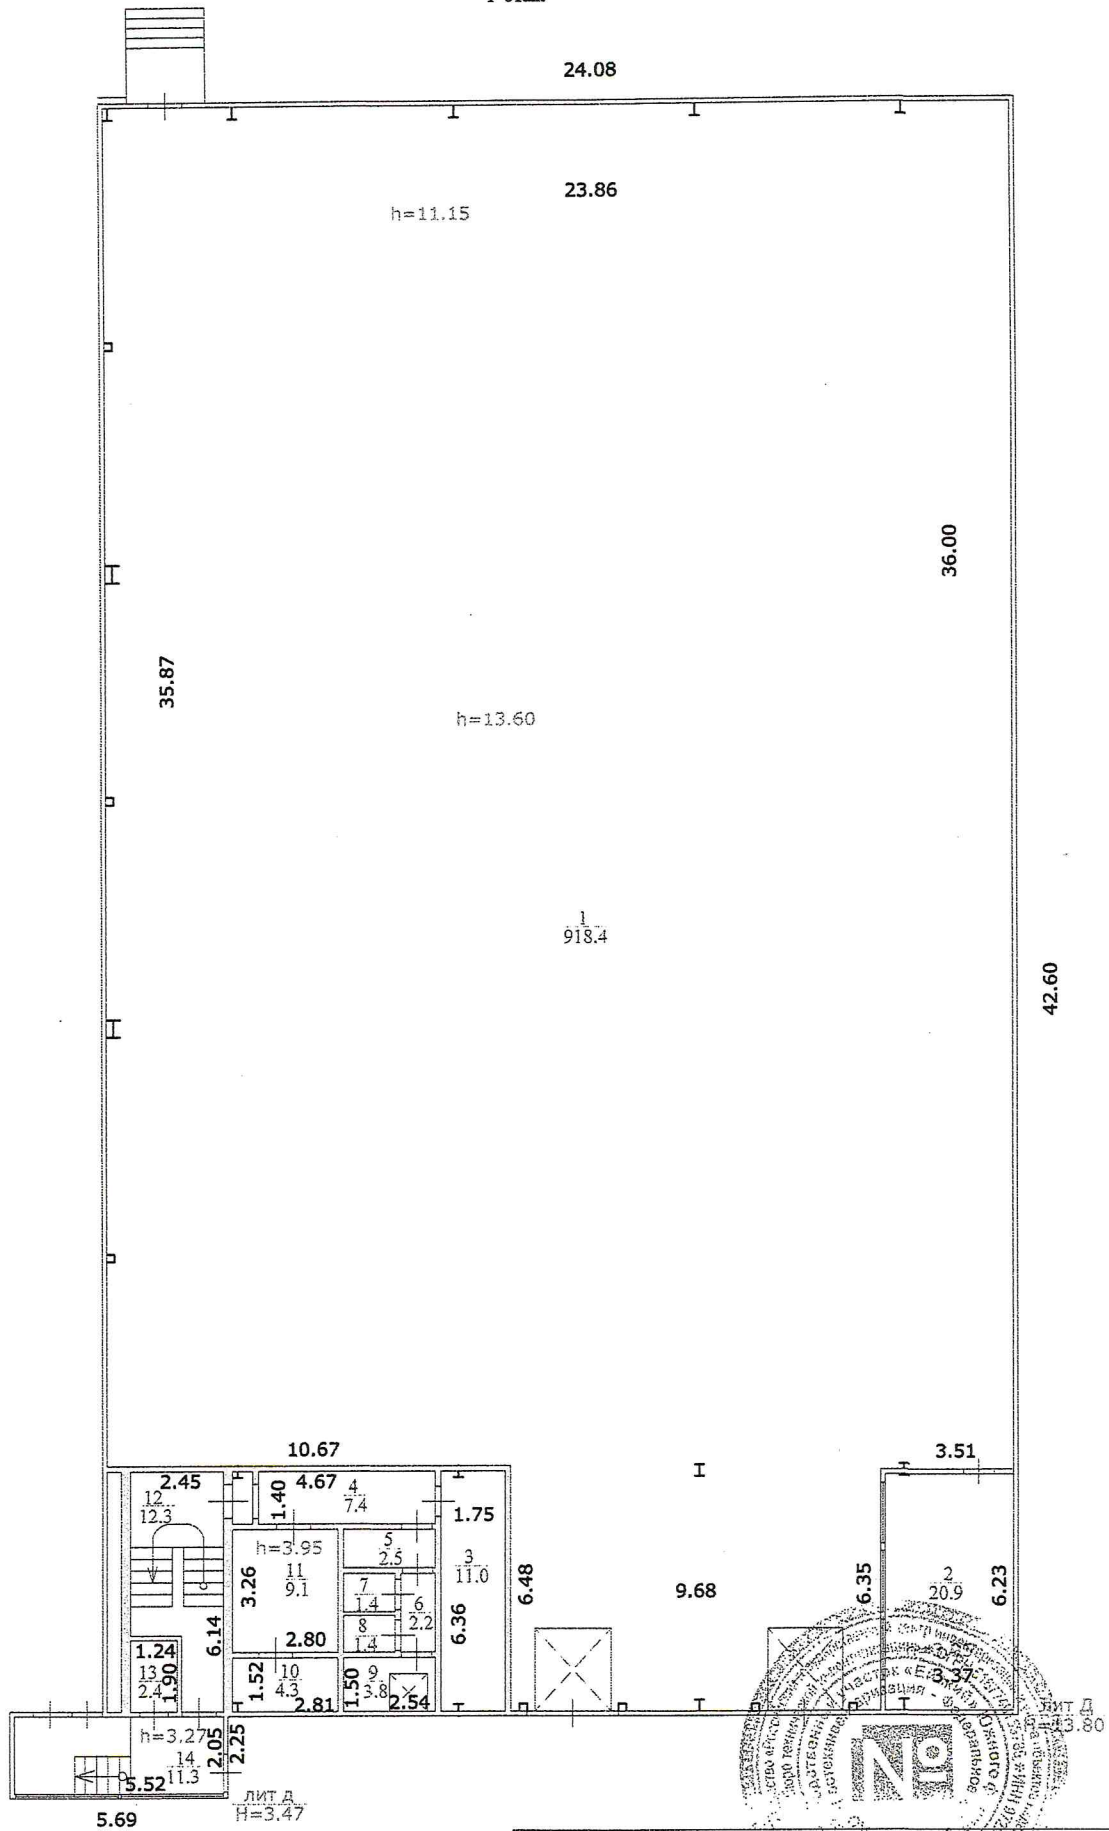

Производственный участок "Виский" Южного филиала АО "Ростехинвентаризация-Федеральное БТИ"					
Начальник отделения:	Мокшина И.Б.	Поэтажный план лит Д-1 этаж			
Проверил:	Мокшина И.Б.	г. Ейск	Лист	1	
Исполнитель:	Бутенко А.В.	ул. Щорса, 53/4	Листов	2	
01.03.2019 г			Масштаб	1:200	

Поэтажный план
2 этаж

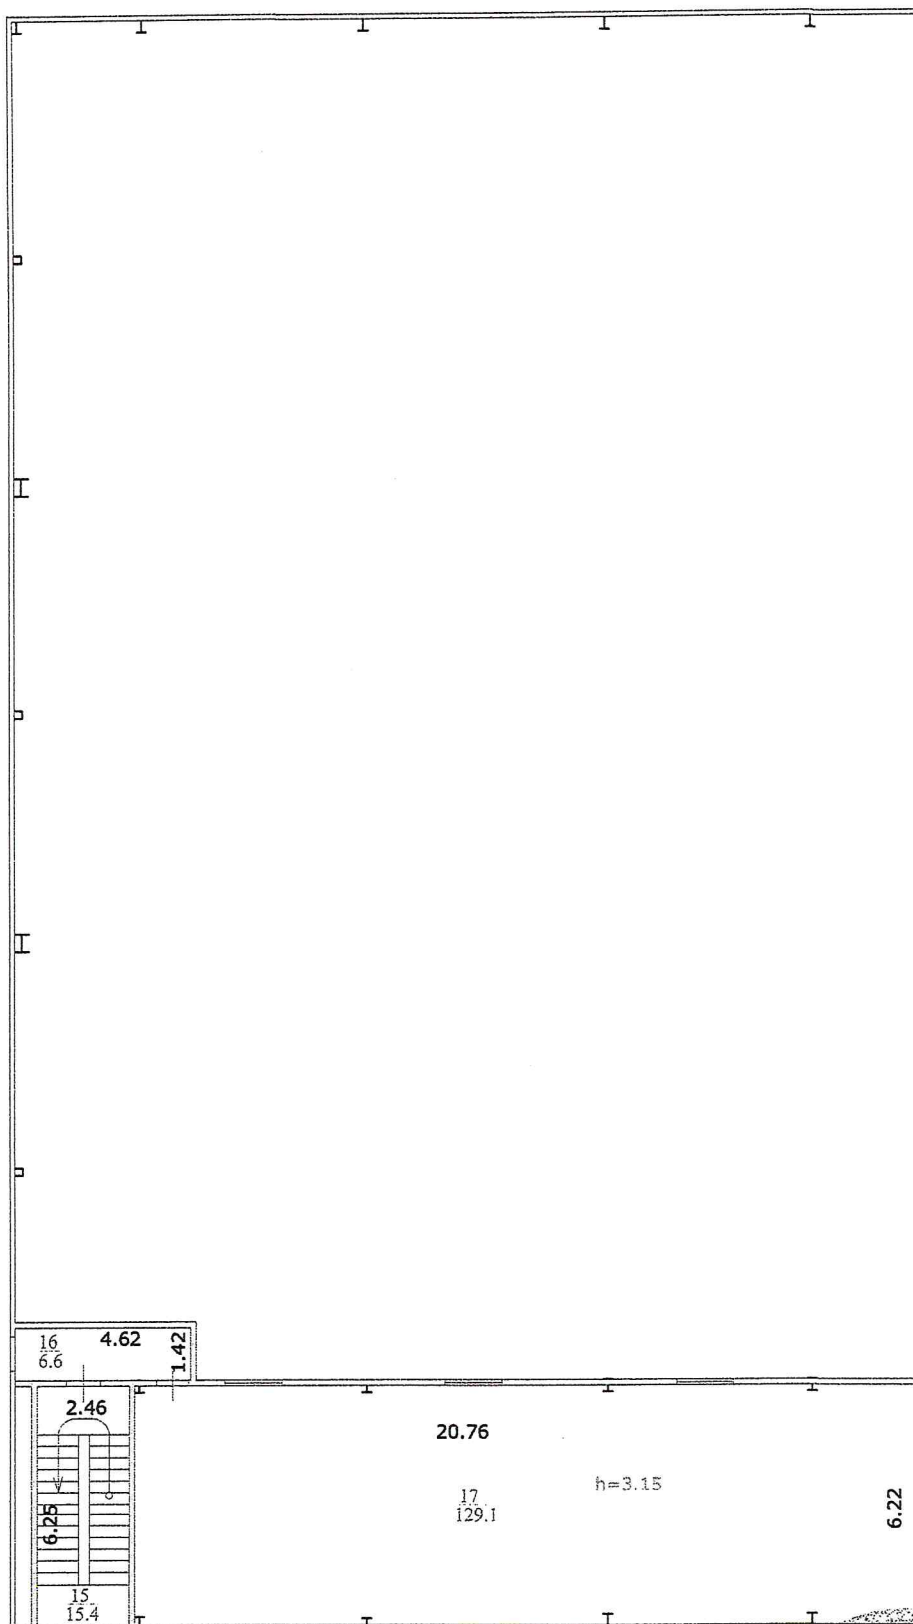

Производственный участок "Евский" Южного филиала АО "Ростехинвентаризация - Федеральное БТИ"			
Начальник отделения: 01.03.2019 г	Мокшина И.Б.	Поэтажный план лит Д-2 этаж г. Евск ул. Шорса, 53/4 Масштаб 1:200	2
Проверил: 01.03.2019 г	Мокшина И.Б.		2
Исполнитель: 01.03.2019 г	Бутенко А.В.		2

На нежилое и жилые строения, имеющие встроенные нежилые помещения
Экспликация № 1

г. Ейск по ул.(пер.) ул. Щорса д. 53/4

Площадь по внутреннему обмеру в кв.м., в том числе преднач. наченная под помещ. ения										Итого по квартире, этажу, строению	Высота помещений по внутреннему обмеру
Нежилая		Жилая		Жилая		Жилая		Жилая			
Основная		вспомогательная		Основная		вспомогательная		Основная		вспомогательная	
1	2	3	4	5	6	7	8	9	10	11	12
Назначение частей помещений: жилая комната, канцеляр- ское помещение, классная комната, кухня, коридор и т.п.											
формула подсчета площади по внутреннему обмеру											
Склад											
Техническое помещение											
подсобное помещение											
Коридор											
подсобное помещение											
Коридор											
подсобное помещение											
подсобное помещение											
душевая											
подсобное помещение											
подсобное помещение											
Лестничная клетка											
Электрощитовая											
Коридор											
Итого по помещению по : 1-му этажу											
Итого по помещению по : 2-му этажу											
Итого по помещению :											

Итого по этажам: 1, 2		918.4	241.1						1159.5	
Итого по зданию		918.4	241.1						1159.5	
Площадь здания в пределах внутренних поверхностей наружных стен		1177.6								

VI. Описание конструктивных элементов здания и определение износа

Литера Д Год постройки 2019 Число этажей 2
 Группа капитальности _____ Вид внутренней отделки _____

№№ п.п.	Наименование конструктивных элементов	Описание конструктивных элементов (материал, конструкция, отделка и пр.)	Техническое состояние (осадки, трещины, гниль и т.п.)	Удельный вес по таблице	Поправка к уд. весу в %	Удельный вес конст. элем. с поправкой	Износ %	Процент износа к строению	Тек. изм. Износ %	Процент износа к строению
1	2	3	4	5	6	7	8	9	10	11
1	Фундамент	железобетонный					0			
2	а. Стены и их наружная отделка	металлический каркас, сэндвич-панель					0			
	б. Перегородки	кирпичные, газоблоки					0			
3	Перекрытия чердачные	металлоконструкция					0			
	междуэтажные									
	подвальные									
4	Крыша	сэндвич панель кровельная					0			
5	Полы	бетонная стяжка					0			
6	Проемы Оконные	металлопластиковые					0			
	Дверные	металлопластиковые, металлические								
7	Внутренняя отделка						0			
8	Сан. и электротех. устройства	отопление	АГВ и др.				0			
		водопровод	центральный							
		канализация	местная							
		электроосвещение	да							
		радио								
		телефон								
		телевидение								
		ванны								
		горячее водоснабжение								
		лифты								
9	Разные работы						0			

Итого 100 х х

процент износа (гр. 9) x 100

% износа, приведенный к 100 по формуле: $\frac{\text{процент износа (гр. 9)} \times 100}{\text{удельный вес (гр. 7)}} =$

IX. Техническое описание пристроек и других частей здания

Наименование конструктивных элементов	литера	Удельный вес по таблице	Ценностный коэффициент	Уд. вес после применения	литера	Удельный вес по таблице	Ценностный коэффициент	Уд. вес после применения	литера	Удельный вес по таблице	Ценностный коэффициент	Уд. вес после применения
	—				—				—			
Фундамент												
Стены и перегородки												
Перекрытия												
Крыша												
Полы												
Проемы												
Отделочные работы												
Электроосвещение												
Прочие работы												
Итого		100	X		Итого	100	X		Итого	100	X	

Наименование конструктивных элементов	литера	Удельный вес по таблице	Ценностный коэффициент	Уд. вес после применения	литера	Удельный вес по таблице	Ценностный коэффициент	Уд. вес после применения	литера	Удельный вес по таблице	Ценностный коэффициент	Уд. вес после применения
Фундамент												
Стены и перегородки												
Перекрытия												
Крыша												
Полы												
Проемы												
Отделочные работы												
Электроосвещение												
Прочие работы												
Итого		100	X		Итого	100	X		Итого	100	X	

Х. Исчисление восстановительной и действительной стоимости здания и его частей

[illegible]

XI. Техническое описание служебных пристроек

Наименование конструктивных элементов	Пристро йка	Удельный вес по таблице	Ценностный коэффициент	Уд. вес после применения	Ступени	Удельный вес по таблице	Ценностный коэффициент	Уд. вес после применения		Удельный вес по таблице	Ценностный коэффициент	Уд. вес после применения
	литера д				литера д							
Фундамент	бетонно-ленточный											
Стены и перегородки	металлопластиковые				бетонные							
Перекрытия	металлические											
Крыша	металлопрофиль											
Полы	бетонные											
Проемы	Металлопластиковые											
Отделочные работы												
Электроосвещение	да											
Прочие работы												
	Итого	100	X	0	Итого	100	X	0	Итого	100	X	-

Наименование конструктивных элементов	литера _	Удельный вес по таблице	Ценностный коэффициент	Уд. вес после применения	литера _	Удельный вес по таблице	Ценностный коэффициент	Уд. вес после применения	литера _	Удельный вес по таблице	Ценностный коэффициент	Уд. вес после применения
Фундамент												
Стены и перегородки												
Перекрытия												
Крыша												
Полы												
Проемы												
Отделочные работы												
Электроосвещение												
Прочие работы												
	Итого	100	X		Итого	100	X		Итого	100	X	

XII. Исчисление стоимости служебных пристроек

[illegible]

[illegible][illegible]

Исполнили		(Бутенко А. В.)
Проверил		(Mokshina И. Б.)
Начальник бюро		(Mokshina И. Б.)

Работа выполнена	" " 200 г.	" " 200 г.	Обследовал	Ипроведил	Руководитель