



План на отм. 0,000 (1 этаж)

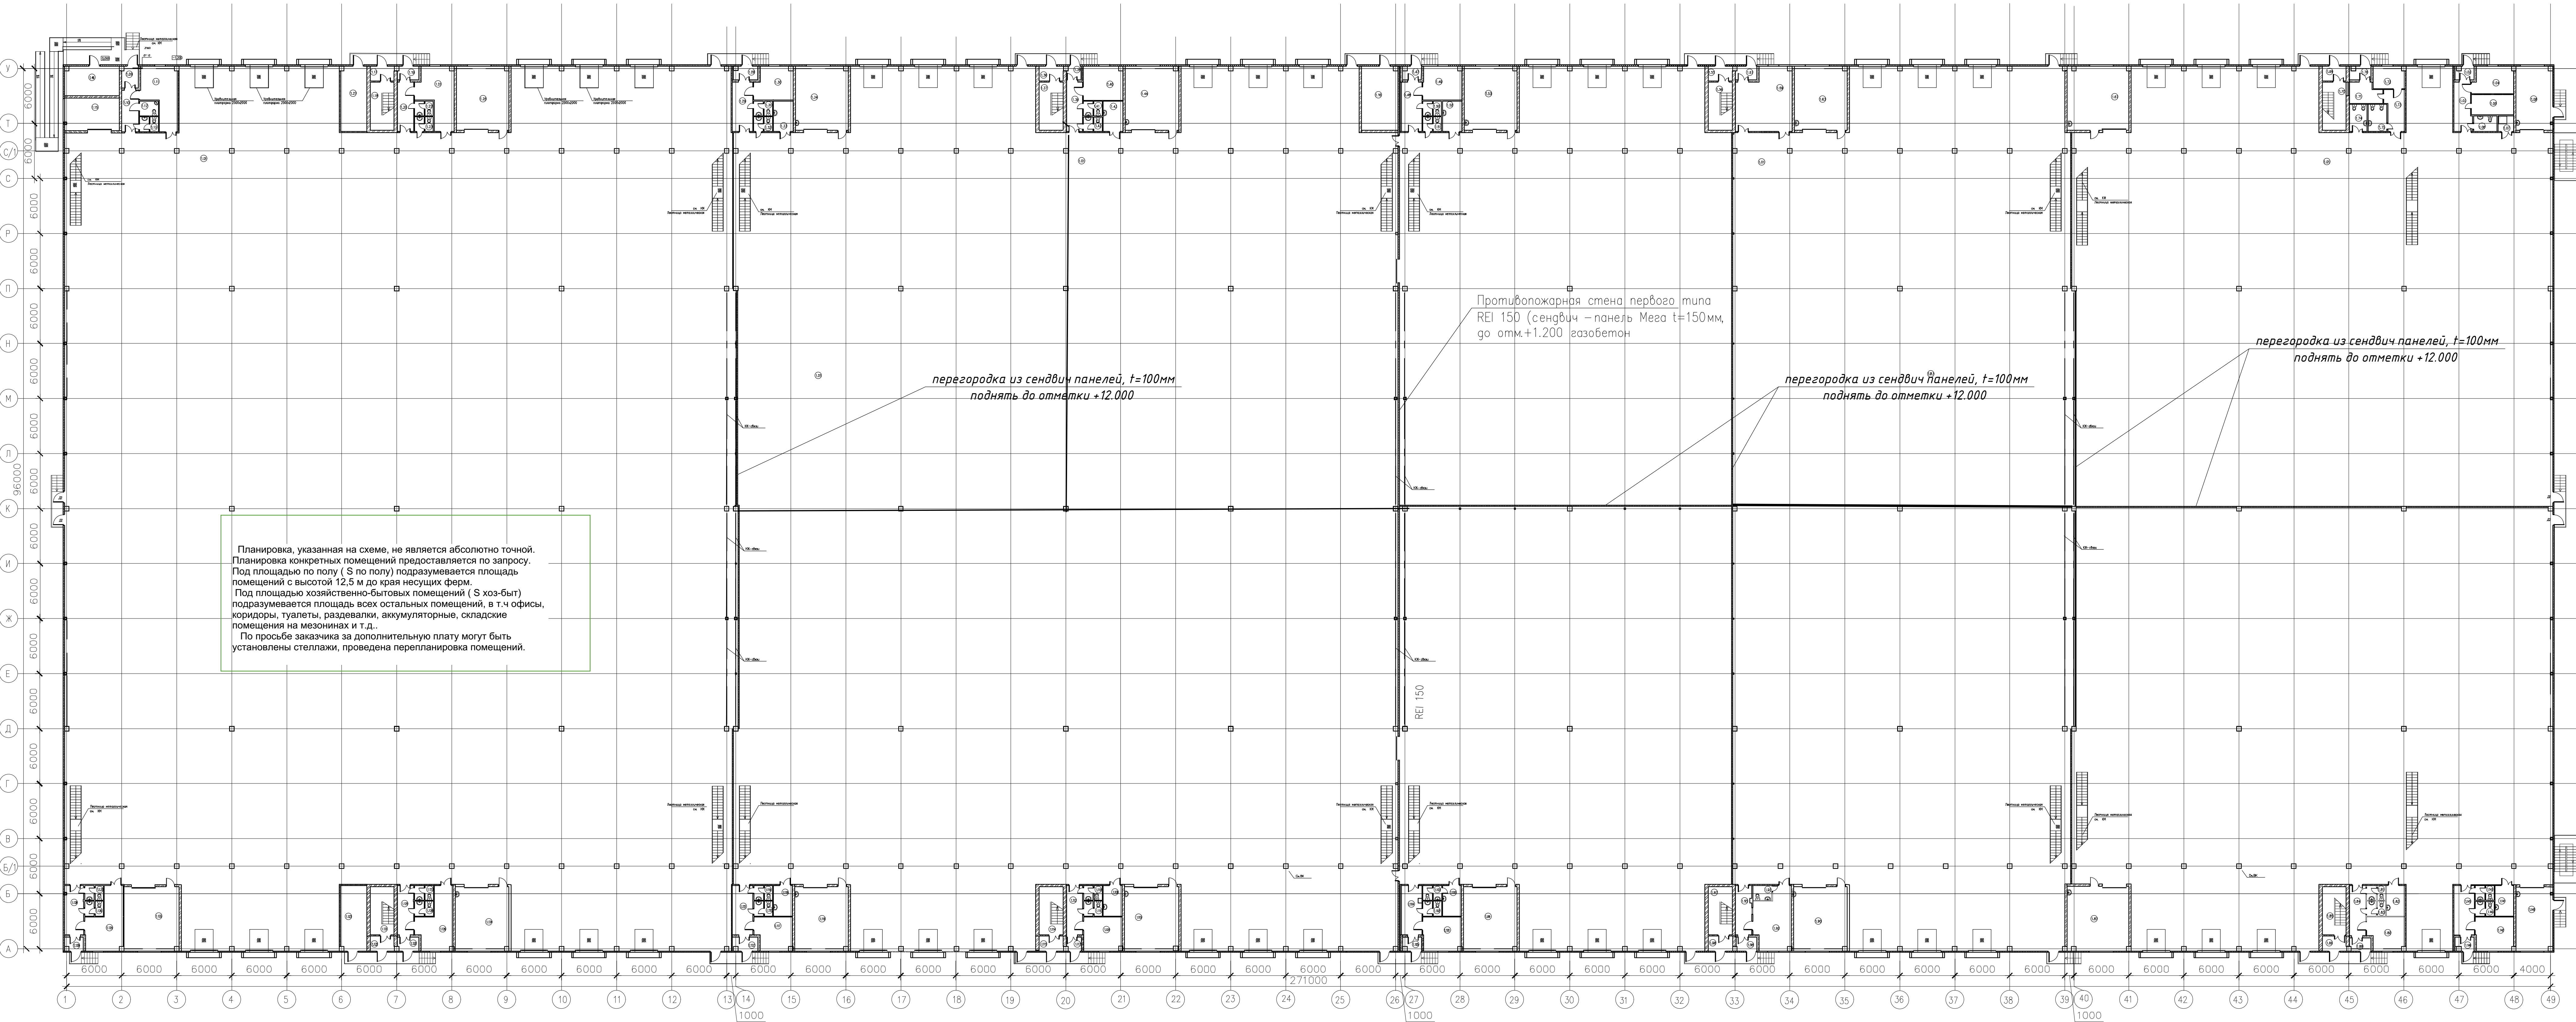

Экспликация помещений														
Номер помещения	Наименование	Площадь, м²	Кат. помещения											
1.01	Складское помещение	13123	В1	1.36	Тамбур	3,97		1.78	Тамбур	2,80		1.113	Тамбур	2,44
1.01.1	Складское помещение	11314	В1	1.37	Лестничная клетка	13,90		1.79	Коридор	17,63		1.114	Лестничная клетка	13,90
1.02	Тамбур	2,80		1.38	Тамбур	2,32		1.80	Офисное помещение	15,20		1.115	Тамбур	3,90
1.03	Коридор	9,8		1.39	Коридор	9,3		1.81	Санузел	3,15		1.116	Помещение для электроаппаратуры	41,70
1.04	Офисное помещение	13,2		1.40	Офисное помещение	15,20		1.82	Помещение для уборочного инвентаря	6,86	В4	1.117	Офисное помещение	15,20
1.05	Офисное помещение	11,0		1.41	Санузел	3,15		1.83	Санузел	3,15		1.118	Помещение для уборочного инвентаря	6,86
1.06	Санузел	4,1		1.42	Санузел	3,15		1.84	Коридор	17,63		1.119	Санузел	3,15
1.07	Помещение для уборочного инвентаря	2,9		1.43	Помещение для уборочного инвентаря	6,86	В4	1.85	Лестничная клетка	14,30		1.120	Санузел	3,15
1.08	Помещение для электроаппаратуры	27,43	В3	1.44	Помещение для электроаппаратуры	41,78	В3	1.86	Тамбур	3,65		1.121	Коридор	10,80
1.09	Тамбур	5,31		1.46	Водометный узел	11,74	Д	1.87	Помещение для электроаппаратуры	45,85	В3	1.122	Тамбур	3,60
1.10	Коридор	8,32		1.47	Тамбур	2,71		1.88	Тамбур	2,89		1.124	Помещение для электроаппаратуры	41,70
1.11	Офисное помещение	22,06		1.48	Коридор	10,80		1.90	Помещение для электроаппаратуры	43,31	В3	1.126	Офисное помещение	22,06
1.12	Санузел	3,15		1.49	Офисное помещение	15,20						1.127	Санузел	3,15
1.13	Санузел	3,15		1.50	Санузел	3,15		1.92	Офисное помещение	15,20		1.128	Санузел	3,15
1.15	Помещение для электроаппаратуры	28,40	В3	1.51	Санузел	3,15		1.93	Санузел	3,15		1.129	Коридор	10,80
1.16	ИТП 2	27,75	В3	1.52	Помещение для уборочного инвентаря	6,86	В4					1.130	Тамбур	3,90
1.17	Тамбур	3,62		1.53	Помещение для электроаппаратуры	41,73	В3	1.95	Коридор	9,28		1.131	Лестничная клетка	13,90
1.18	Лестничная клетка	13,90		1.55	Тамбур	4,35		1.96	Тамбур	3,33		1.132	Тамбур	3,90
1.19	Тамбур	3,46		1.56	Лестничная клетка	13,90		1.97	Лестничная клетка	13,90		1.133	Помещение для электроаппаратуры	41,70
1.20	Коридор	11,32		1.57	Тамбур	3,50		1.98	Тамбур	3,97		1.135	Офисное помещение	22,06
1.21	Офисное помещение	22,06		1.59	Офисное помещение	39,74		1.99	Помещение для электроаппаратуры	43,31	В3	1.136	Санузел	3,15
1.22	Санузел	3,15		1.63	Помещение для электроаппаратуры	41,78	В3	1.100	Помещение для уборочного инвентаря	6,86	В4	1.137	Санузел	3,15
1.23	Санузел	3,15		1.67	Помещение для электроаппаратуры	45,62	В3	1.101	Офисное помещение	15,20		1.138	Коридор	11,25
1.25	Помещение для электроаппаратуры	41,78	В3	1.69	Тамбур	3,65		1.102	Санузел	3,15		1.139	Тамбур	2,80
1.27	Электрощитовая, ГРЩ	20,40	В3	1.70	Лестничная клетка	13,90		1.103	Санузел	3,15		1.140	Помещение для электроаппаратуры	27,46
1.28	Тамбур	3,61		1.71	Коридор	7,42		1.104	Коридор	10,80		1.141	Помещение для уборочного инвентаря	6,86
1.29	Коридор	10,80		1.72	Офисное помещение	8,39		1.105	Тамбур	2,71		1.142	Офисное помещение	15,20
1.30	Офисное помещение	15,20		1.73	Коридор	9,48		1.107	Помещение для электроаппаратуры	43,31	В3	1.143	Санузел	3,15
1.31	Санузел	3,15		1.74	Санузел	5,9		1.108	Помещение для уборочного инвентаря	6,86	В4	1.144	Санузел	3,15
1.32	Санузел	3,15		1.75	Санузел	6,0		1.109	Офисное помещение	15,20		1.145	Коридор	11,25
1.33	Помещение для уборочного инвентаря	6,86	В4	1.76	Тамбур	2,80		1.110	Санузел	3,15		1.146	Тамбур	2,80
1.34	Помещение для электроаппаратуры	41,73	В3	1.77	Коридор	11,09		1.112	Коридор	9,3			ИТОГО 1 этаж	25 993,77

Примечания:
1. Данный лист смотреть совместно с листом 2.

01-01/19-III				
РФ, 196626, Санкт-Петербург, пос. Шушары, Московское ш., д.139, строение 1, кадастровый номер 78:02:15:15013521				
Иск. и констр.	Лист № 1	Подп.	Дата	Проект перепланировки части межкв. помещений складского здания
Гип. Разраб.	Григорьев	Григорьев	Григорьев	Студия Лист Листов
Н.контр.	Рубцова	Рубцова	Рубцова	Р 1
Архитектурно-строительная часть 1 этаж				

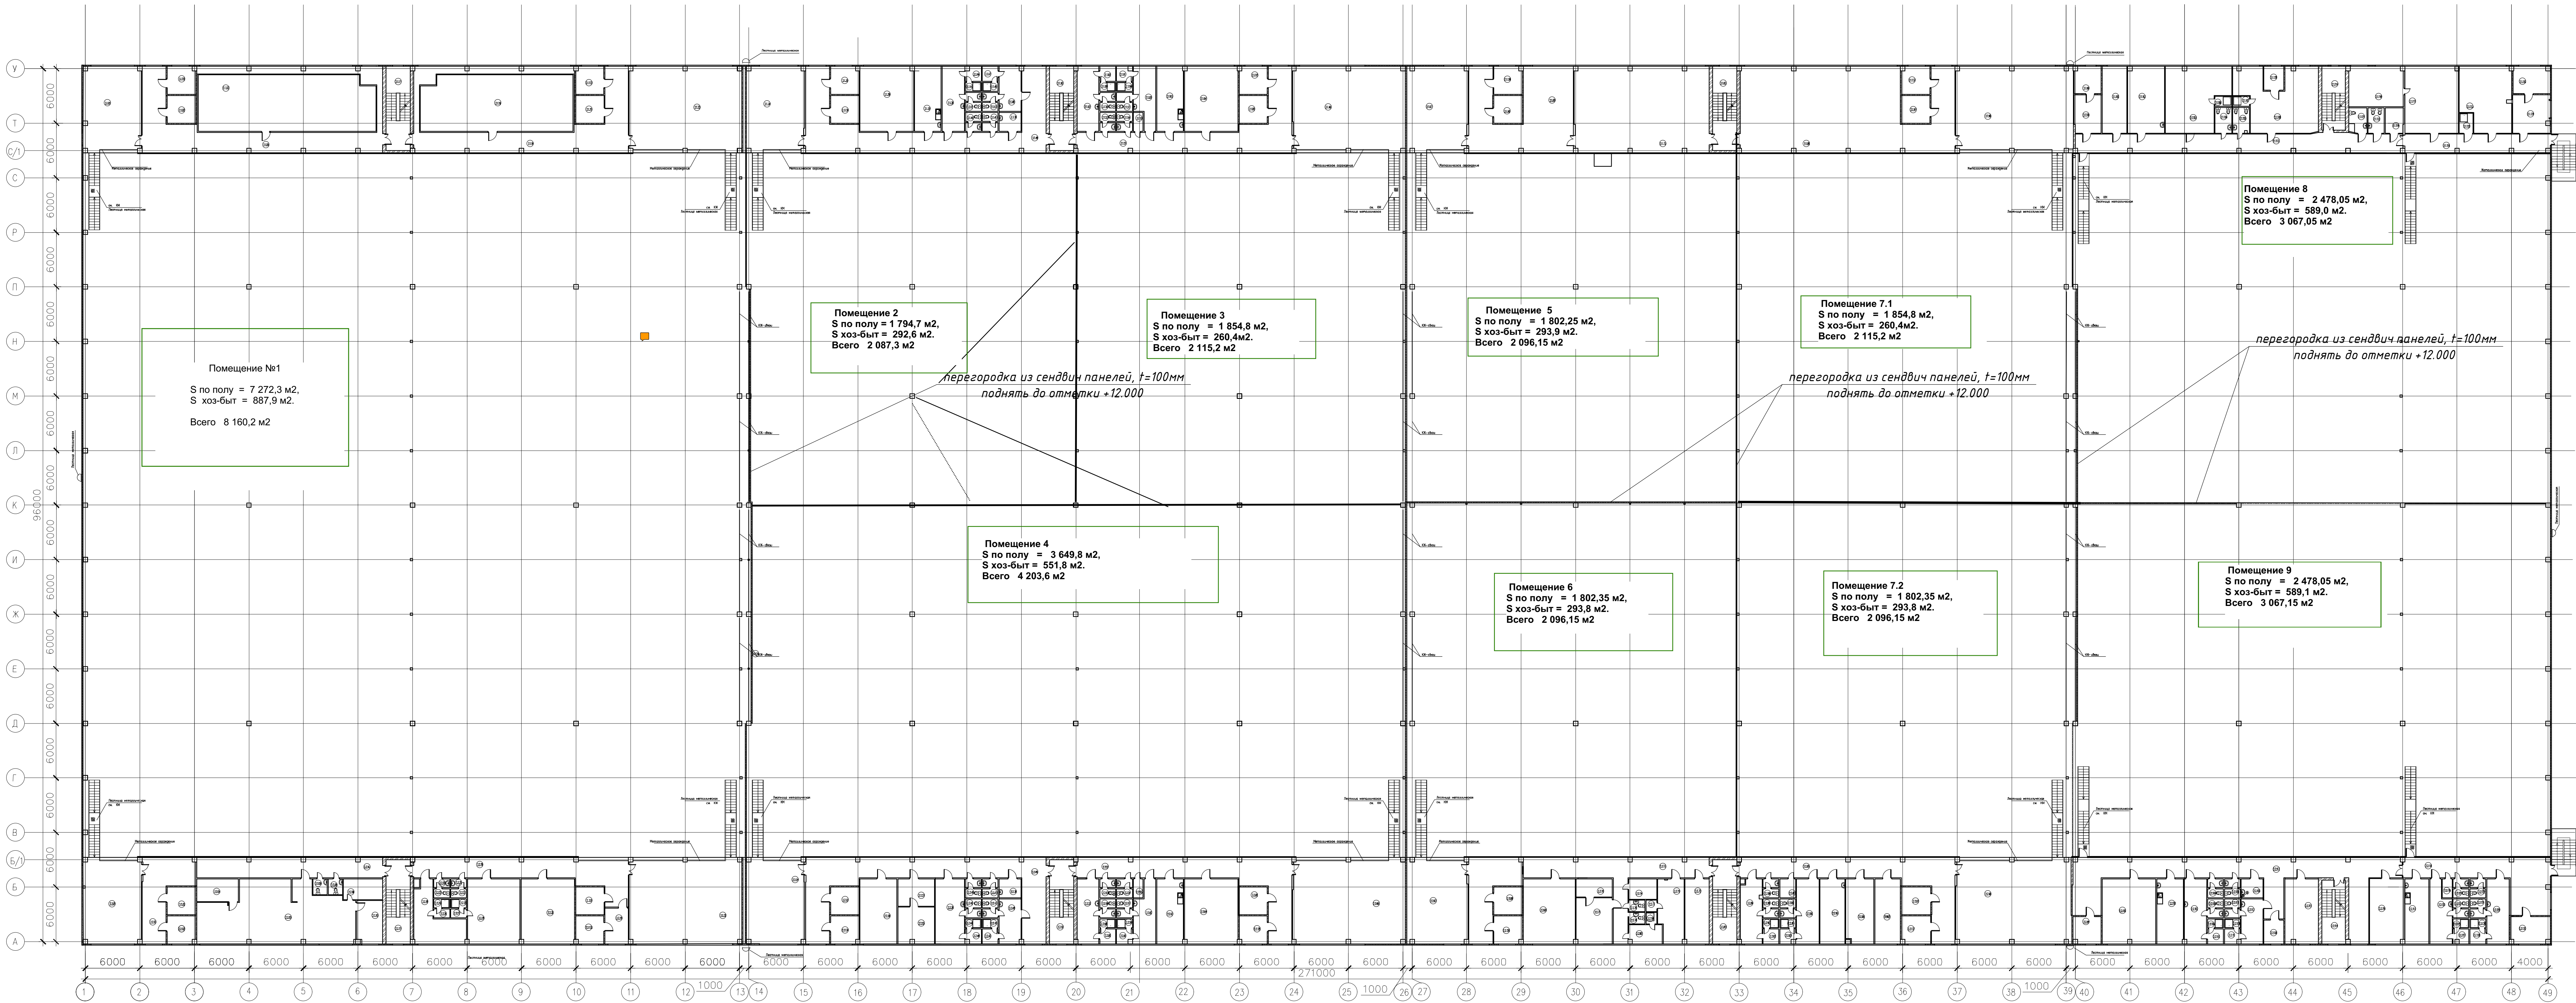

Экспликация помещений				Экспликация помещений				Экспликация помещений				Экспликация помещений				Экспликация помещений			
Номер помещения	Наименование	Площадь м²	Кат. помещения	Номер помещения	Наименование	Площадь м²	Кат. помещения	Номер помещения	Наименование	Площадь м²	Кат. помещения	Номер помещения	Наименование	Площадь м²	Кат. помещения	Номер помещения	Наименование	Площадь м²	Кат. помещения
2.1.01	Антресоли	58,00	2.1.61	Предузиель	2,85	2.1.132	Техническое помещение	8,61	2.2.35	Электрощитовая	9,55	2.2.71	Гардероб	19,30	2.2.108	Душевая	1,75		
2.1.02	Электрощитовая	9,38	2.1.62	Гардероб	15,10	2.1.133	Техническое помещение	9,42	2.2.36	Орильное помещение	29,00	2.2.72	Орильное помещение	20,00	2.2.109	Душевая	1,75		
2.1.03	Орильное помещение	111,50	2.1.63	Комната отдыха и приема пищи	21,00	2.1.134	Техническое помещение	9,42	2.2.37	Комната отдыха и приема пищи	12,00	2.2.73	Коридор	58,80	2.2.110	Предузиель	2,65		
2.1.04	Коридор	110,50	2.1.64	Орильное помещение	42,00	2.1.135	Техническое помещение	9,42	2.2.38	Гардероб	17,67	2.2.74	Кладовая	7,00	2.2.111	Предузиель	2,85		
2.1.17	Лестничная клетка	24,54	2.1.65	Электрощитовая	9,38	2.1.136	Техническое помещение	9,42	2.2.39	Помещение уборочного инвентаря	5,03	2.2.75	Орильное помещение	18,90	2.2.112	Гардероб	11,78		
2.1.18	Орильное помещение	97,00	2.1.66	Антресоли	116,34	2.1.137	Техническое помещение	9,42	2.2.40	Санузел	3,50	2.2.76	Санузел	2,00	2.2.113	Коридор	117,80		
2.1.19	Коридор	100,00	2.1.67	Антресоли	63,10	2.1.138	Электрощитовая	5,68	2.2.41	Санузел	3,50	2.2.77	Кладовая	1,50	2.2.114	Лестничная клетка	18,50		
2.1.31	Электрощитовая	8,65	2.1.68	Электрощитовая	9,55	2.2.01	Антресоли	60,00	2.2.42	Санузел	3,50	2.2.78	Санузел	2,00	2.2.115	Орильное помещение	26,06		
2.1.32	Антресоли	115,00	2.1.69	Коридор	90,00	2.2.02	Электрощитовая	9,38	2.2.43	Санузел	3,50	2.2.79	Душевая	1,50	2.2.116	Орильное помещение	26,76		
2.1.34	Антресоли	62,80	2.1.73	Коридор	141,50	2.2.03	Коридор	35,00	2.2.44	Душевая	1,75	2.2.80	Предузиель	7,50	2.2.117	Комната отдыха и приема пищи	20,80		
2.1.35	Электрощитовая	9,55	2.1.83	Лестничная клетка	24,54	2.2.04	Комната отдыха и приема пищи	11,50	2.2.45	Душевая	1,75	2.2.83	Лестничная клетка	24,54	2.2.118	Коридор	52,23		
2.1.36	Орильное помещение	29,00	2.1.85	Коридор	201,00	2.2.05	Орильное помещение	99,00	2.2.46	Предузиель	2,65	2.2.84	Гардероб	17,05	2.2.119	Паросное помещение	2,30		
2.1.37	Комната отдыха и приема пищи	12,00	2.1.97	Электрощитовая	9,38	2.2.06	Помещение уборочного инвентаря	5,03	2.2.47	Предузиель	2,85	2.2.85	Коридор	74,36	2.2.120	Гардероб	15,00		
2.1.38	Гардероб	17,67	2.1.98	Антресоли	118,00	2.2.08	Санузел	2,50	2.2.48	Гардероб	11,78	2.2.86	Санузел	3,50	2.2.121	Санузел	3,50		
2.1.39	Помещение уборочного инвентаря	5,03	2.1.99	Техническое помещение	8,65	2.2.09	Коридор	3,00	2.2.49	Коридор	99,78	2.2.87	Санузел	3,50	2.2.122	Санузел	3,50		
2.1.40	Санузел	3,50	2.1.100	Орильное помещение	21,30	2.2.10	Кладовая	14,00	2.2.50	Лестничная клетка	24,54	2.2.88	Санузел	3,50	2.2.123	Санузел	3,50		
2.1.41	Санузел	3,50	2.1.101	Техническое помещение	12,50	2.2.15	Комната отдыха и приема пищи	16,00	2.2.51	Коридор	73,93	2.2.89	Санузел	3,50	2.2.124	Санузел	3,50		
2.1.42	Санузел	3,50	2.1.102	Орильное помещение	17,67	2.2.16	Коридор	99,78	2.2.52	Гардероб	15,10	2.2.90	Душевая	1,75	2.2.125	Душевая	1,75		
2.1.43	Санузел	3,50	2.1.103	Гардероб	45,50	2.2.17	Лестничная клетка	24,54	2.2.53	Санузел	3,50	2.2.91	Душевая	1,75	2.2.126	Душевая	1,75		
2.1.44	Душевая	1,75	2.1.104	Санузел	5,30	2.2.18	Гардероб	23,30	2.2.54	Санузел	3,50	2.2.92	Предузиель	2,85	2.2.127	Предузиель	2,85		
2.1.45	Душевая	1,75	2.1.105	Санузел	5,30	2.2.19	Коридор	60,20	2.2.55	Паросное помещение	2,30	2.2.93	Предузиель	2,65	2.2.128	Предузиель	2,85		
2.1.46	Предузиель	2,65	2.1.106	Душевая	2,00	2.2.20	Санузел	2,50	2.2.56	Санузел	3,50	2.2.94	Гардероб	15,10	2.2.129	Гардероб	17,76		
2.1.47	Предузиель	2,85	2.1.107	Душевая	2,00	2.2.21	Санузел	2,50	2.2.57	Санузел	3,50	2.2.95	Комната отдыха и приема пищи	21,00	2.2.130	Техническое помещение	12,03		
2.1.48	Гардероб	11,78	2.1.108	Гардероб	55,00	2.2.22	Санузел	1,80	2.2.58	Душевая	1,75	2.2.96	Орильное помещение	20,40	2.2.132	Техническое помещение	8,61		
2.1.49	Коридор	99,78	2.1.113	Коридор	72,50	2.2.23	Санузел	1,80	2.2.59	Душевая	1,75	2.2.96/7	Орильное помещение	20,30	2.2.133	Техническое помещение	9,42		
2.1.50	Лестничная клетка	24,54	2.1.114	Лестничная клетка	18,50	2.2.24	Душевая	1,75	2.2.60	Предузиель	2,65	2.2.97	Электрощитовая	9,38	2.2.134	Техническое помещение	9,42		
2.1.51	Коридор	73,93	2.1.116	Орильное помещение	27,00	2.2.25	Душевая	1,75	2.2.61	Предузиель	2,85	2.2.98	Антресоли	121,19	2.2.135	Техническое помещение	9,42		
2.1.52	Гардероб	15,10	2.1.117	Орильное помещение	43,30	2.2.26	Предузиель	2,00	2.2.62	Гардероб	15,10	2.2.99	Техническое помещение	8,65	2.2.136	Техническое помещение	9,42		
2.1.53	Санузел	3,50	2.1.118	Коридор	32,00	2.2.27	Предузиель	2,00	2.2.63	Комната отдыха и приема пищи	21,00	2.2.100	Орильное помещение	42,00	2.2.137	Техническое помещение	9,42		
2.1.54	Санузел	3,50	2.1.119	Паросное помещение	6,20	2.2.28	Гардероб	40,00	2.2.64	Орильное помещение	42,00	2.2.101	Комната отдыха и приема пищи	21,00	2.2.138	Электрощитовая	5,68		
2.1.55	Паросное помещение	2,30	2.1.120	Паросное помещение	15,00	2.2.29	Орильное помещение	11,40	2.2.65	Электрощитовая	9,38	2.2.102	Гардероб	17,67	Итого:		4 870,05		
2.1.56	Санузел	3,50	2.1.121	Санузел	5,00	2.2.30	Комната отдыха и приема пищи	42,00	2.2.66	Антресоли	116,34	2.2.103	Помещение уборочного инвентаря	5,03					
2.1.57	Санузел	3,50	2.1.122	Санузел	5,10	2.2.31	Электрощитовая	8,65	2.2.67	Антресоли	63,10	2.2.104	Санузел	3,50					
2.1.58	Душевая	1,75	2.1.123	Орильное помещение	3,50	2.2.32	Антресоли	112,80	2.2.68	Электрощитовая	9,55	2.2.105	Санузел	3,50					
2.1.59	Душевая	1,75	2.1.124	Техническое помещение	3,50	2.2.33	Орильное помещение	9,40	2.2.69	Орильное помещение	42,00	2.2.106	Санузел	3,50					
2.1.60	Предузиель	2,65	2.1.130	Техническое помещение	12,03	2.2.34	Антресоли	62,80	2.2.70	Комната отдыха и приема пищи	7,70	2.2.107	Санузел	3,50					

Примечания:
1. Данный лист смотреть совместно с листом 1.

				01-01/19-ПП			
				РФ, 196626, Санкт-Петербург, пос. Шушары, Московское ш., д.139, строение 1, кадастровый номер 78:42:15115013521			
				Проект перепланировки части межкв. помещений складского здания			
				Архитектурно-строительная часть. 1 этаж			
				Формат А0			

Иск. Вкл. в	Лист №	Подп.	Дата
Гл. констр.	Григорьев		
Гип.	Григорьев		
Разраб.	Григорьев		
Н. контр.	Рубцова		

Студия	Лист	Листов
P	2	