

Согласовано			
Взам. инв. №			
Подл. и дата			
Инв. № подл.			

Ведомость рабочих чертежей основного комплекта		
Лист	Наименование	Примечание
1	Общие данные	
2	План на отм. 0.000 в осях А-Д/1-41	
3	План на отм. 0.000 в осях Е-К/1-21	
4	План на отм. 0.000 в осях Е-К/21-41	
5	План кровли	
6	Разрезы 1-1	
7	Схема расположения стен и колонн по оси 41 (демонтаж)	
8	Схема расположения плит покрытия в осях А-Д/1-41 (демонтаж)	
9	Схема расположения плит покрытия в осях Е-К/1-21 (демонтаж)	
10	Схема расположения плит покрытия в осях А-Д/1-41 (монтаж)	
11	Схема расположения плит покрытия в осях Е-К/1-21 (монтаж)	
12	Схема расположения плит покрытия в осях Е-К/21-41 (монтаж)	
13	Схема расположения плит перекрытия на отм. +5.350 в осях 1-41 (монтаж)	
14	Схема расположения плит покрытия в осях А-Д/1-41 (ремонт)	
15	Схема расположения плит покрытия в осях Е-К/1-21 (ремонт)	
16	Схема расположения плит покрытия в осях Е-К/21-41 (ремонт)	
17	Схема раскладки стеновых панелей в осях А-К / К-А	
18	Схема раскладки стеновых панелей в осях 1-41 / 41-1	
19	Спецификации и ведомости	
20	Узлы крепления сэндвич-панелей	

Технические решения, принятые в рабочих чертежах, соответствуют требованиям энергоэффективности и энергосбережения, экологических, санитарно - гигиенических, противопожарных и других норм, действующих на территории РФ и обеспечивают безопасную для жизни и здоровья людей эксплуатацию объекта при соблюдении предусмотренных рабочими чертежами мероприятий.

ГИП _____ Е.В. Огурцов

Расход материалов для восстановления плит покрытия:
КТпрон-праймер -133,3 кг.
КТпрон-2 - 18600 кг
КТпрон-3Т500 - 114410 кг
КТпрон-3/1600 - 4316 кг

Расход материалов для восстановления колонн:
КТпрон-праймер -55,2 кг.
КТпрон-2 - 6500 кг
КТпрон-3Т500 - 64800 кг
КТпрон-3/1600 - 23400 кг



Расход материалов для восстановления ферм:
КТпрон-праймер -51,8 кг.
КТпрон-2 - 5000 кг
КТпрон-3Т500 - 46440 кг
КТпрон-3/1600 - 18000 кг

Расход материалов для восстановления балок:
КТпрон-праймер -21 кг.
КТпрон-2 - 2000 кг
КТпрон-3Т500 - 11800 кг
КТпрон-3/1600 - 7260 кг

							20-08 - АС			
							ООО «Производственное оборудование»			
Изм.	Колуч.	Лист	№ док.	Подпись	Дата		Реканструкция здания цеха комплектации колес, по адресу: г. Липецк, ул. Чехова,12	Стадия	Лист	Листов
Разработал	Белокапытов							Р	1	
Проверил	Батухтин									
ГИП	Огурцов									
Н. Контр.	Захаров						Общие данные			

Составлено		
Изм. №	Взам. инв. №	
Изм. №	Полн. и дата	
	Изм. №	


Номер помеще-ния	Наименование	Площадь, м²	Кол. поме-ще-ний
1	Производственное помещение	26206,26 м²	Д
2	Помещение обзора	14,20 м²	
3	Помещение обзора	13,02 м²	
4	Помещение обзора	13,88 м²	
		26247,36 м²	

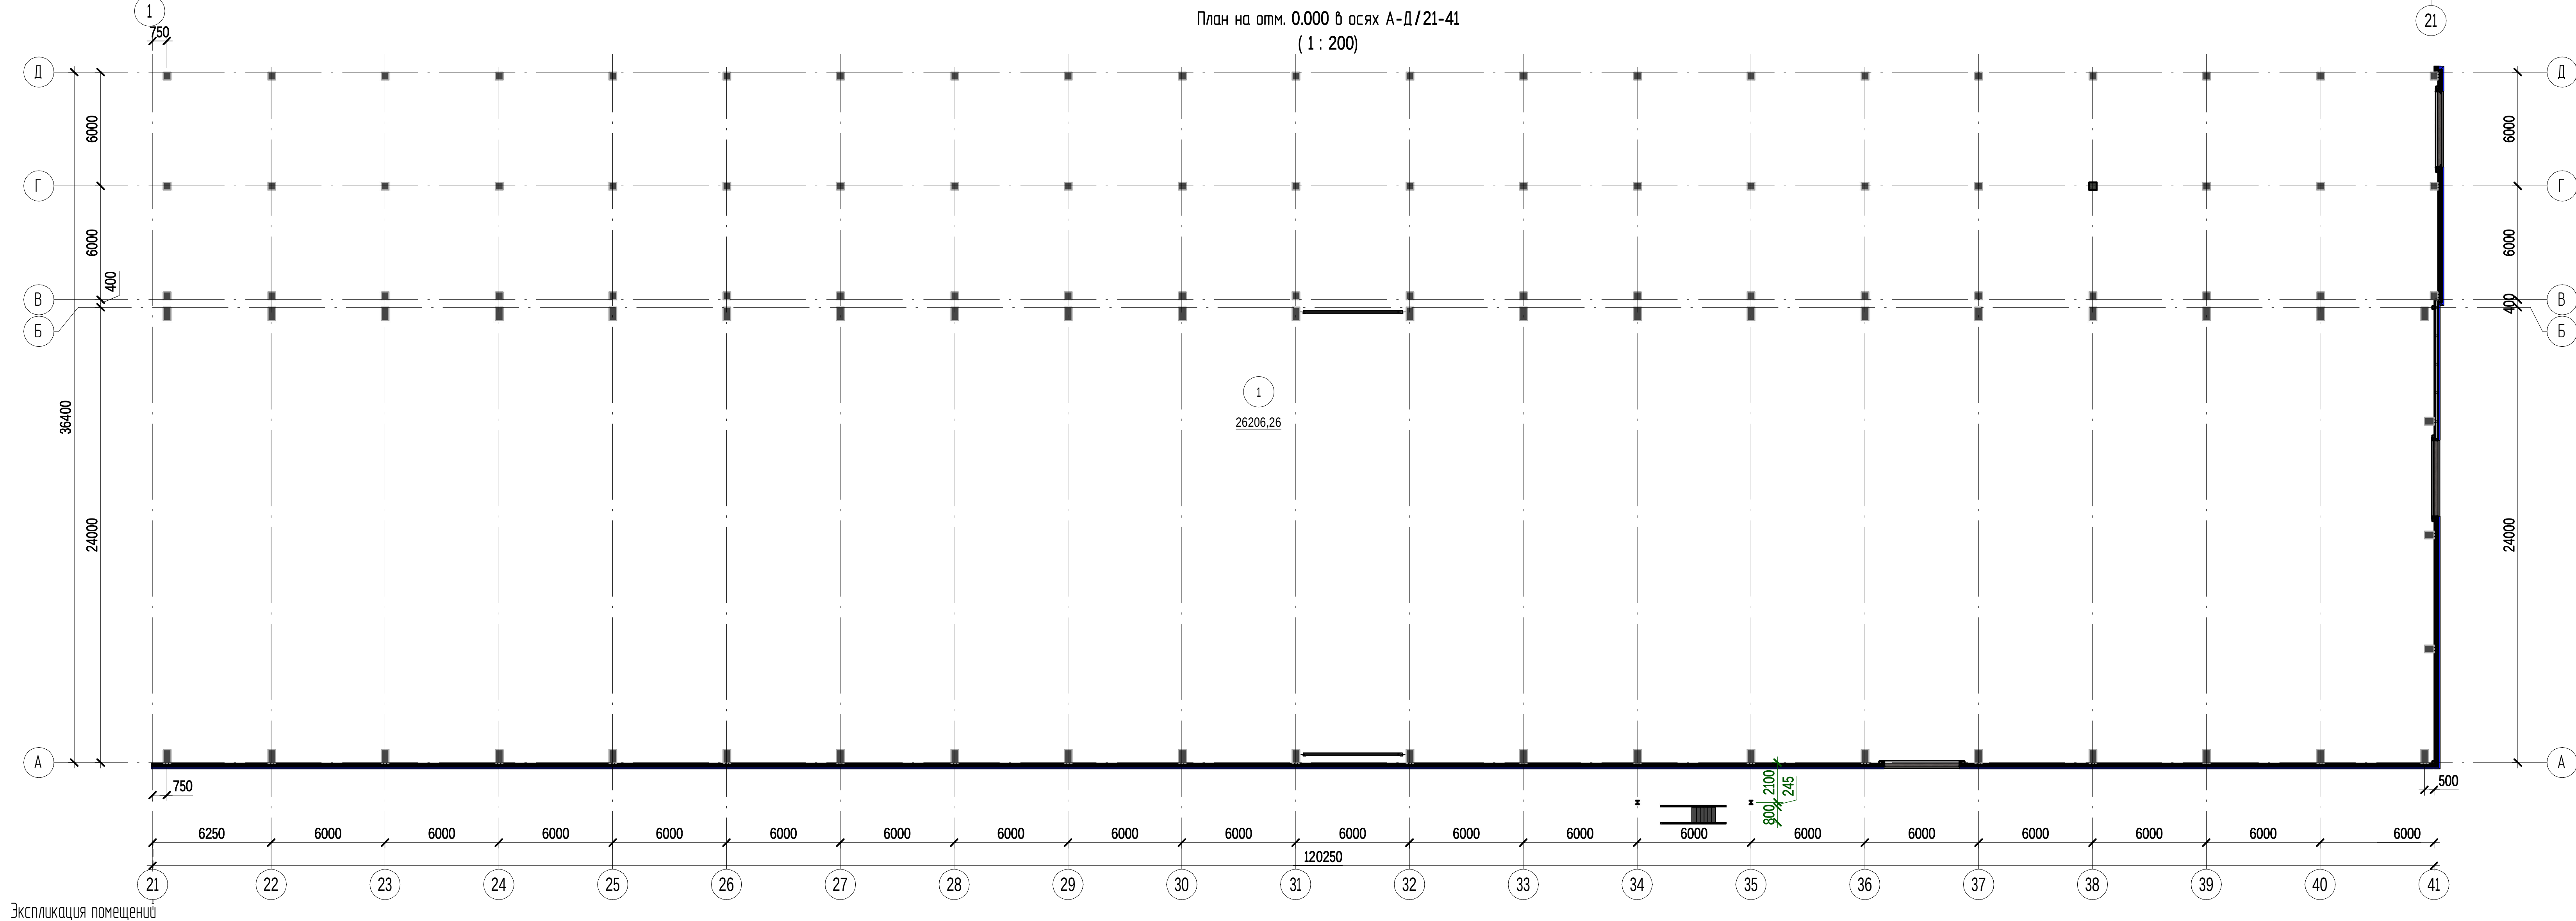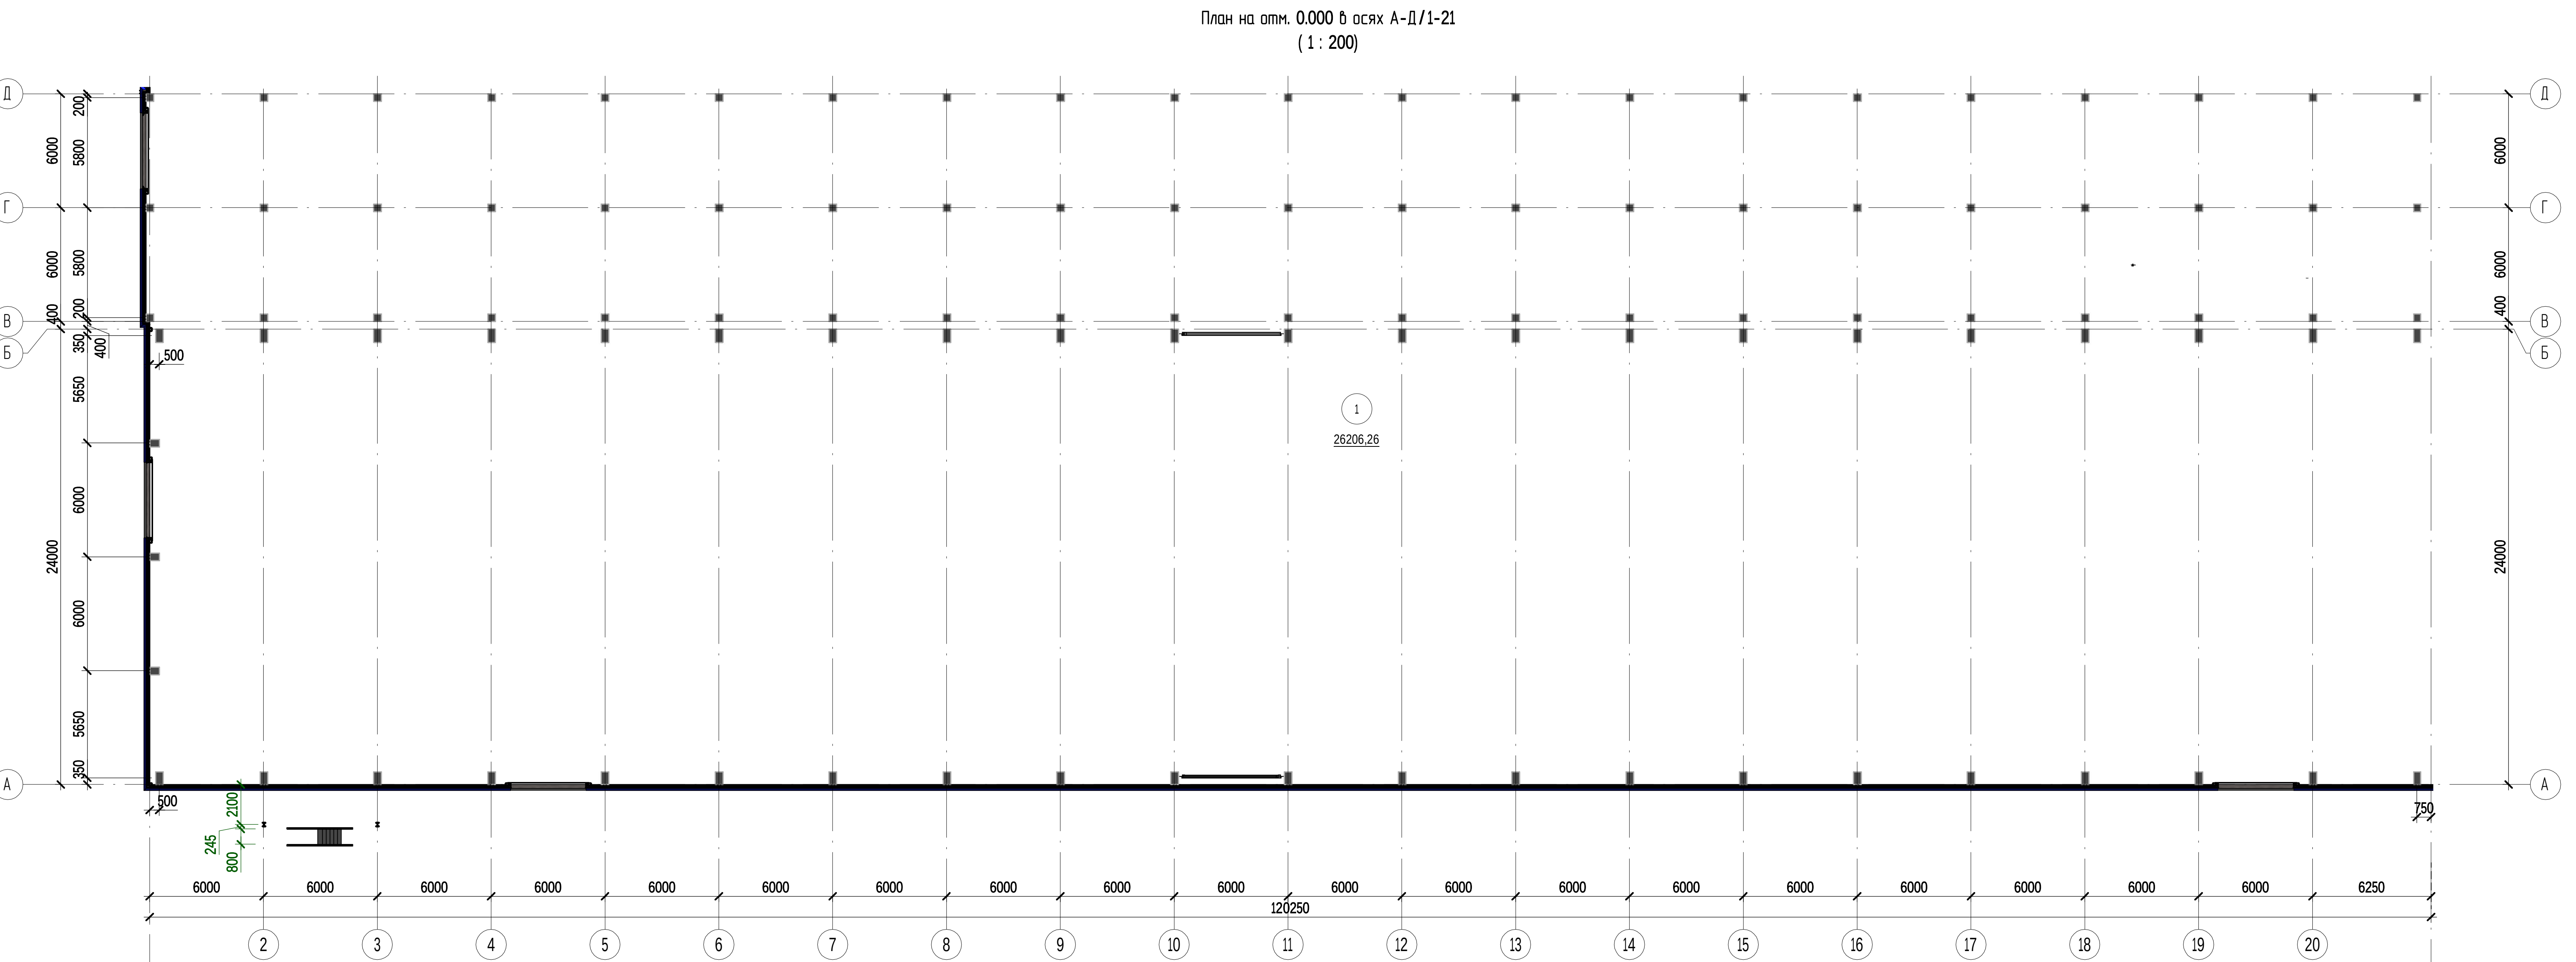

1. Гипсокартонные перегородки выполнить из гипсокартонных листов марки ГК/В по металлическому каркасу, со сплошным заполнением пустот утеплителем марки НГ.

						20-08 - АС		
						ООО «Производственное оборудование»		
Изм.	Колуч.	Лист	№ док.	Подпись	Дата	Реконструкция здания цеха комплектации колес, по адресу: г. Липецк, ул. Чехова,12	Стация	Лист
Разработал	Белоконьков						Р	2
Проверил	Батушкин							
Н. Контр.	Захаров					План на опм. 0.000 в осях А-Д/1-41		

Создано		Полн. и дата	Взам. инв. №
Инв. № подл.			

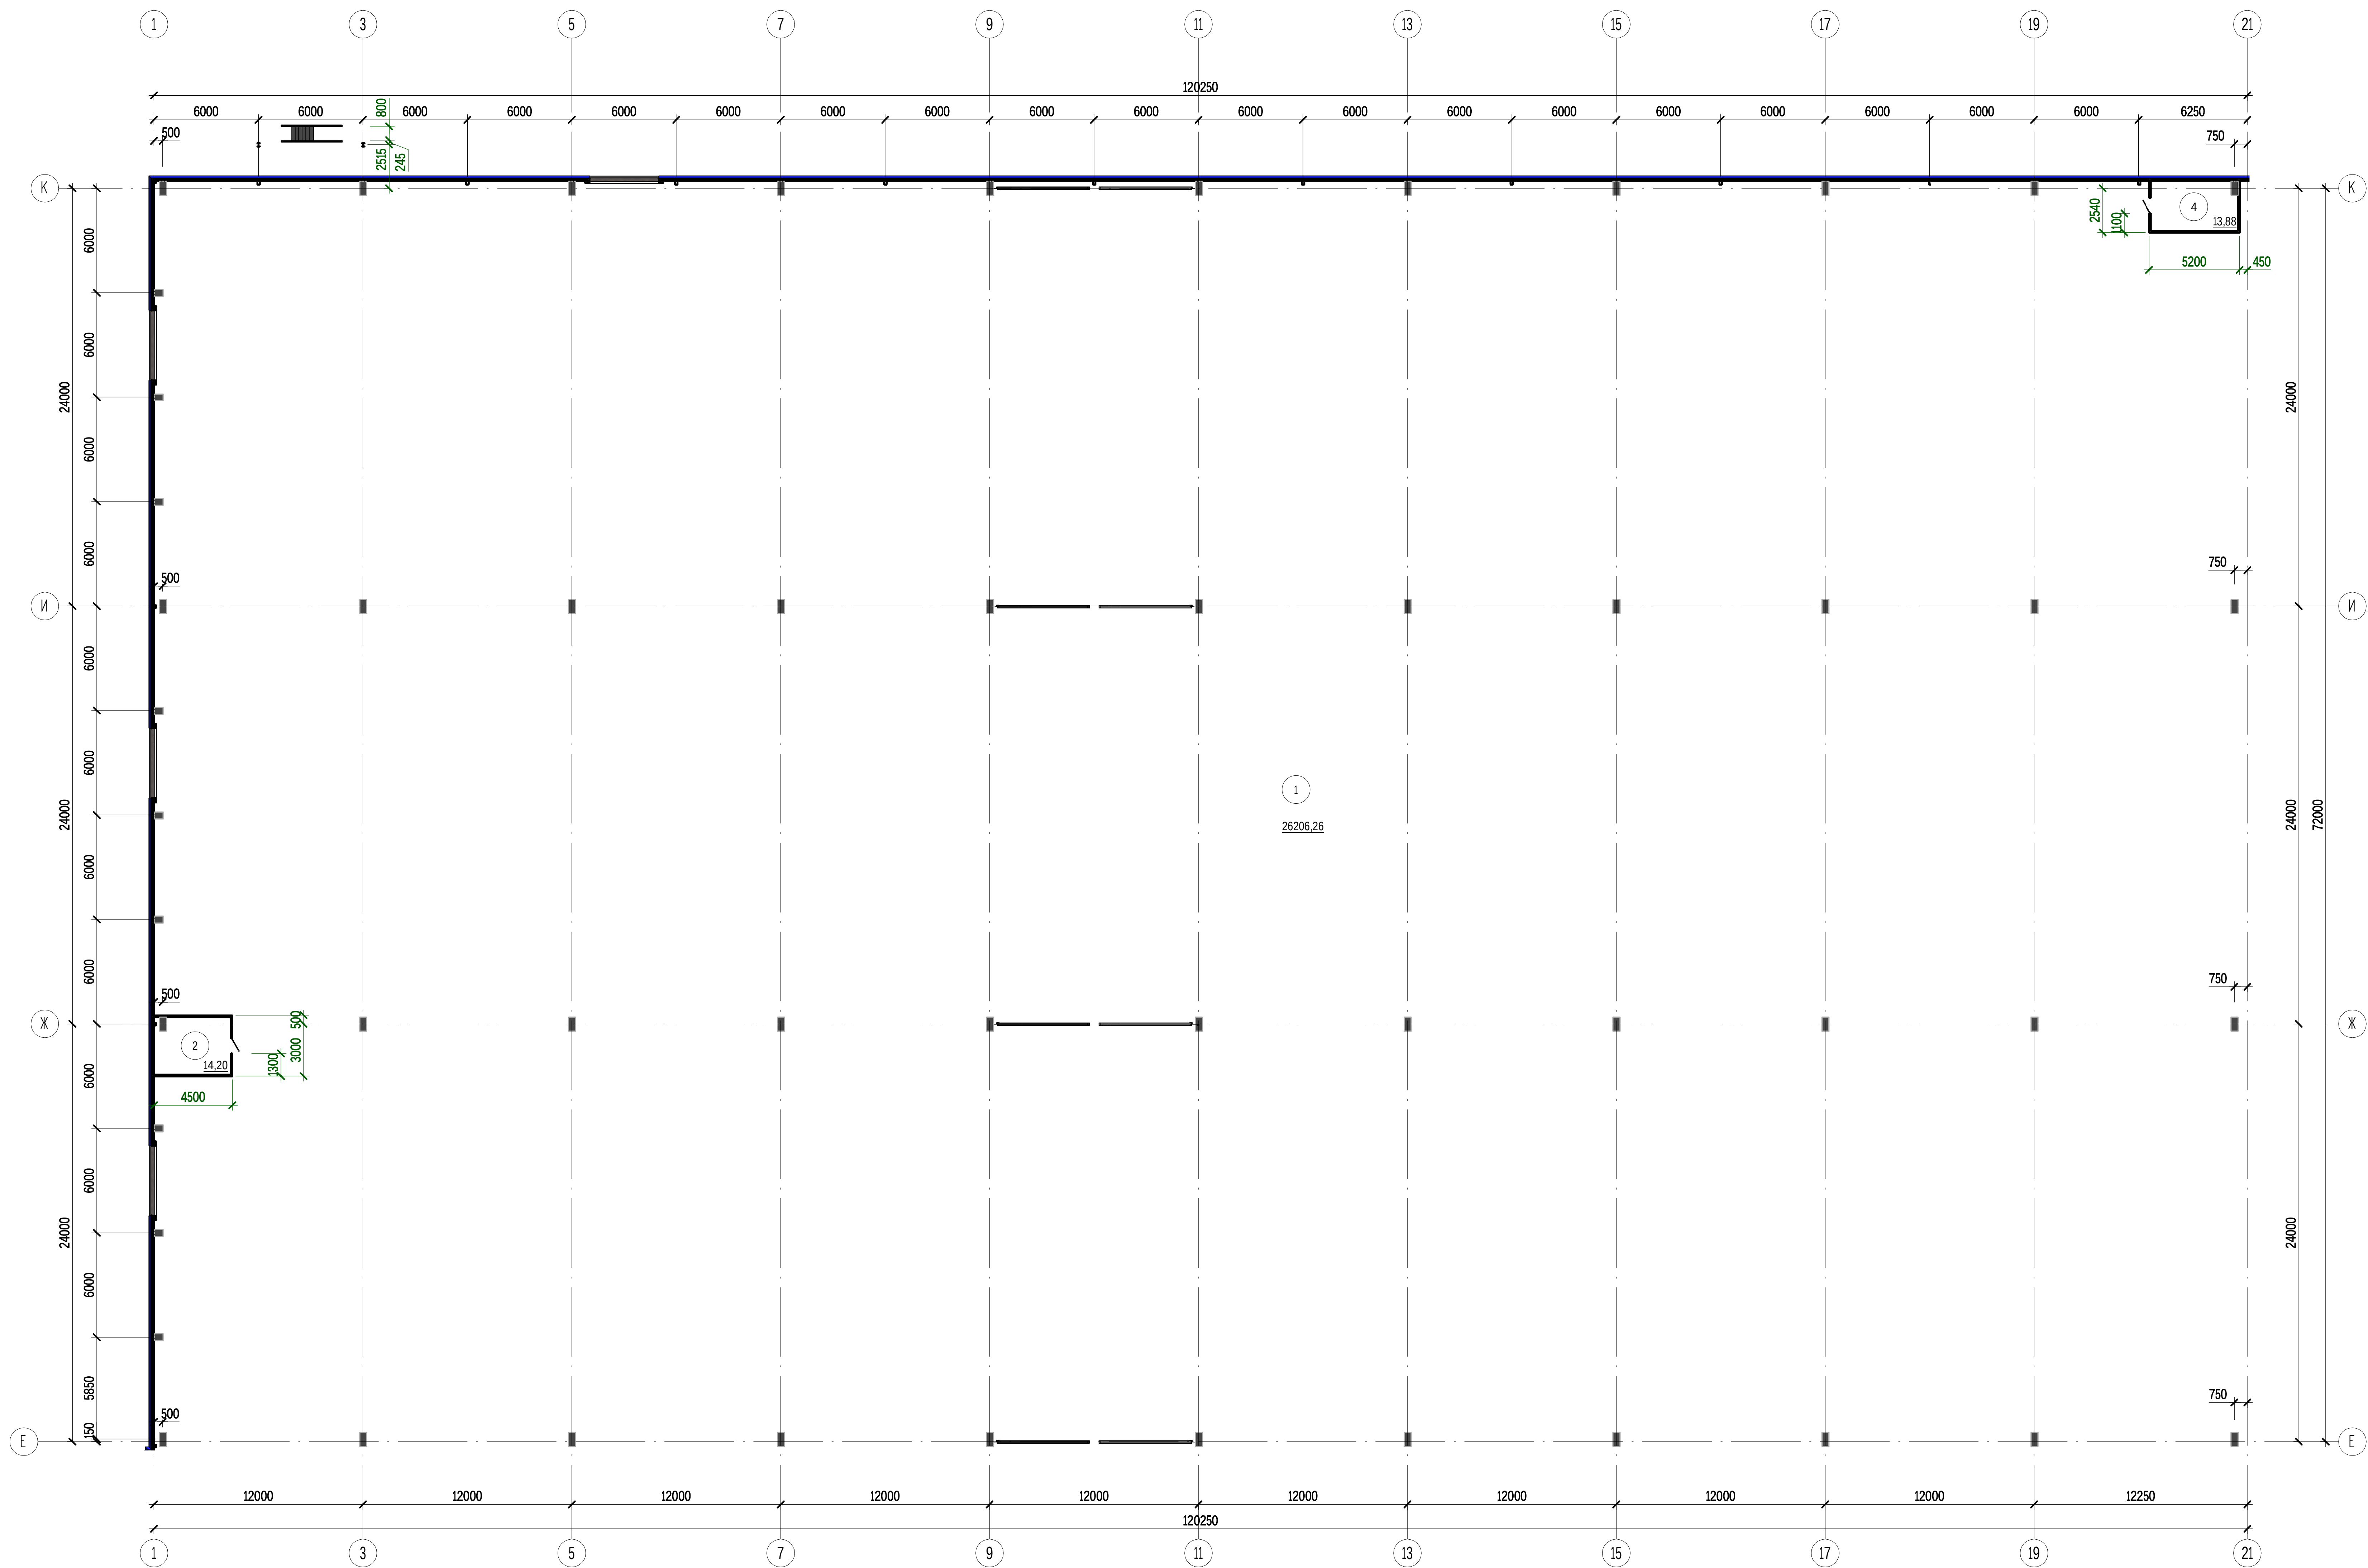

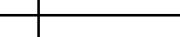
						20-08 - АС			
						ООО «Производственное оборудование»			
Изм.	Колуч.	Лист	№ док.	Подпись	Дата	Реконструкция здания цеха комплектации колес, по адресу: г. Липецк, ул. Чехова,12	Стация	Лист	Листов
Разработал		Белосаптов					Р	3	
Проверил		Батушкин							
Н. Контр.		Захаров							
						План на отм. 0.000 в осях Е-К/1-21			
						  ИМБЕСТ ПРОЕКТ			

Схема расположения колонн по оси 41 (демонтаж)
(1 : 100)



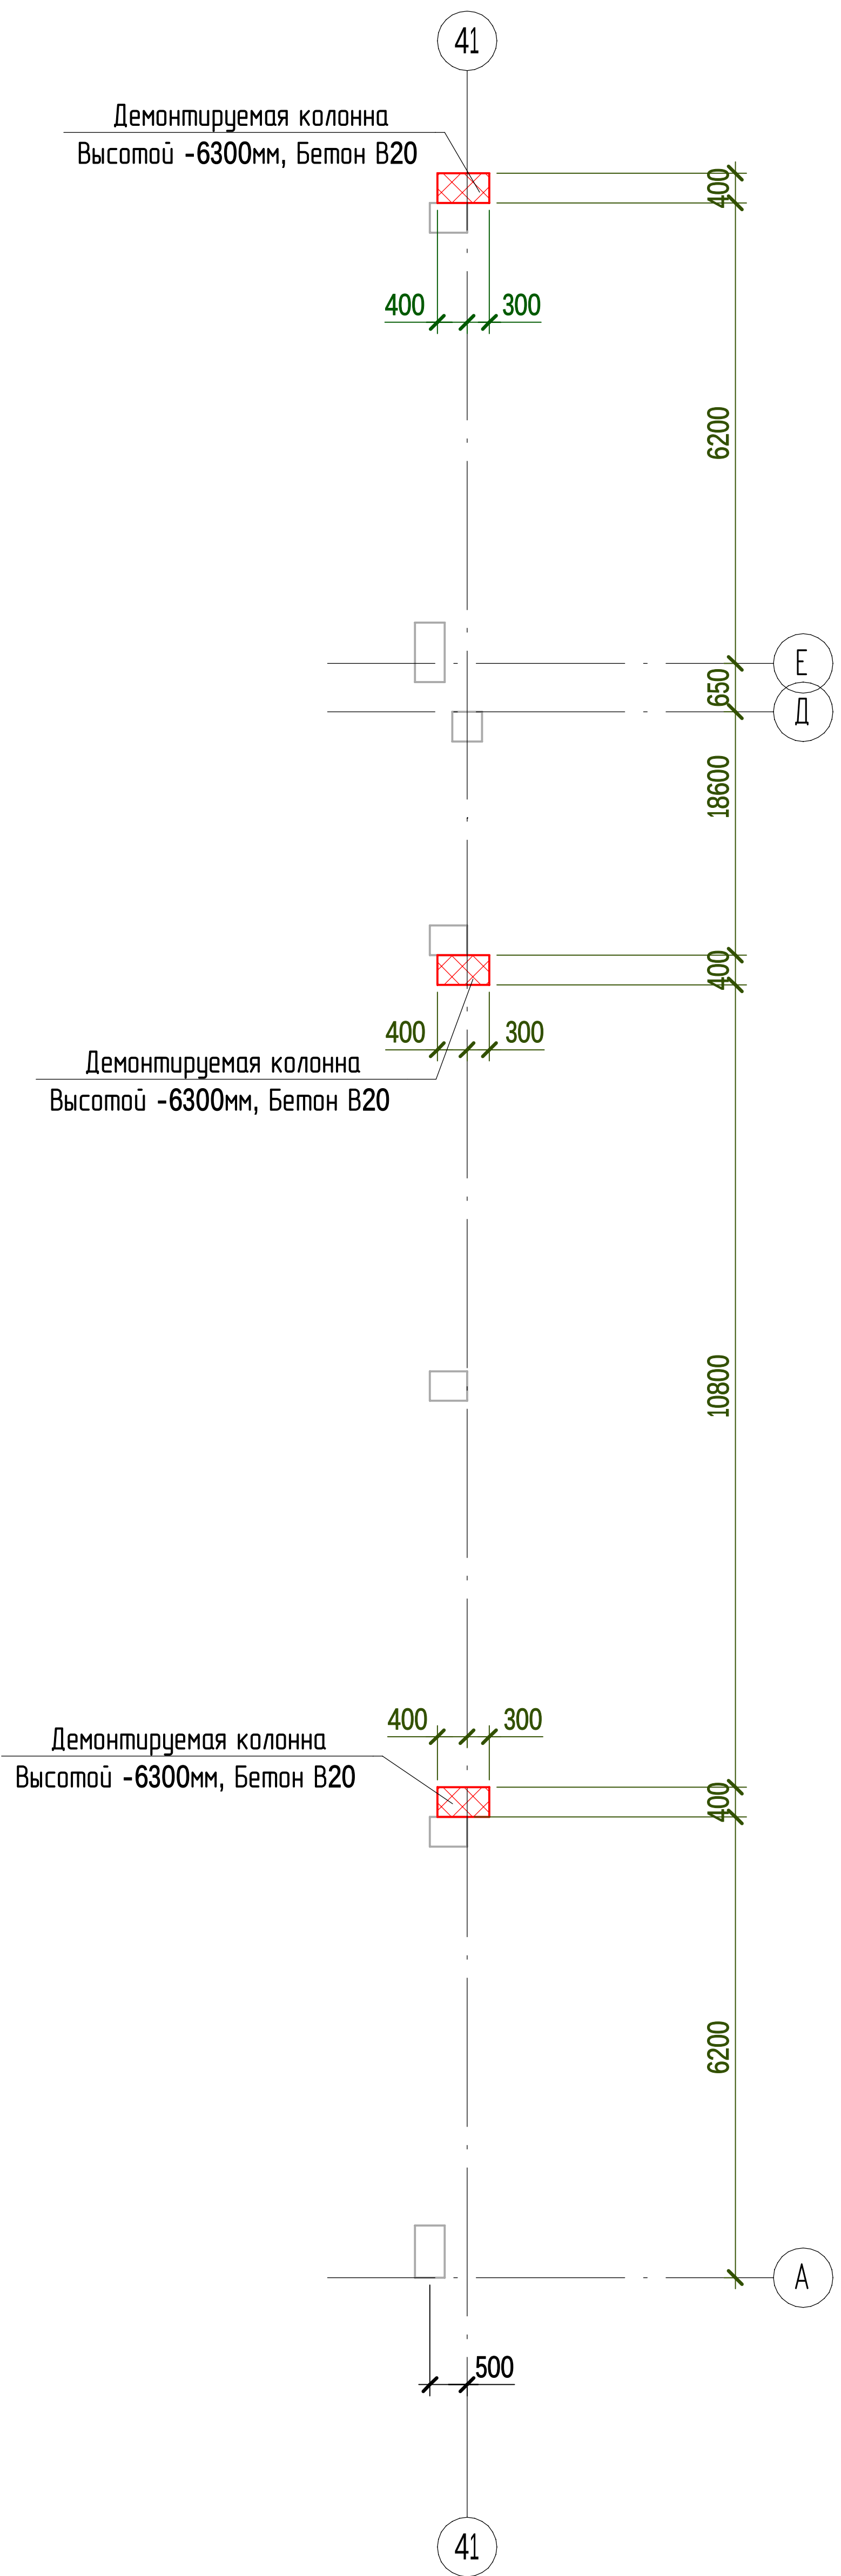


Схема расположения стен по оси 41 (демонтаж)
(1 : 100)

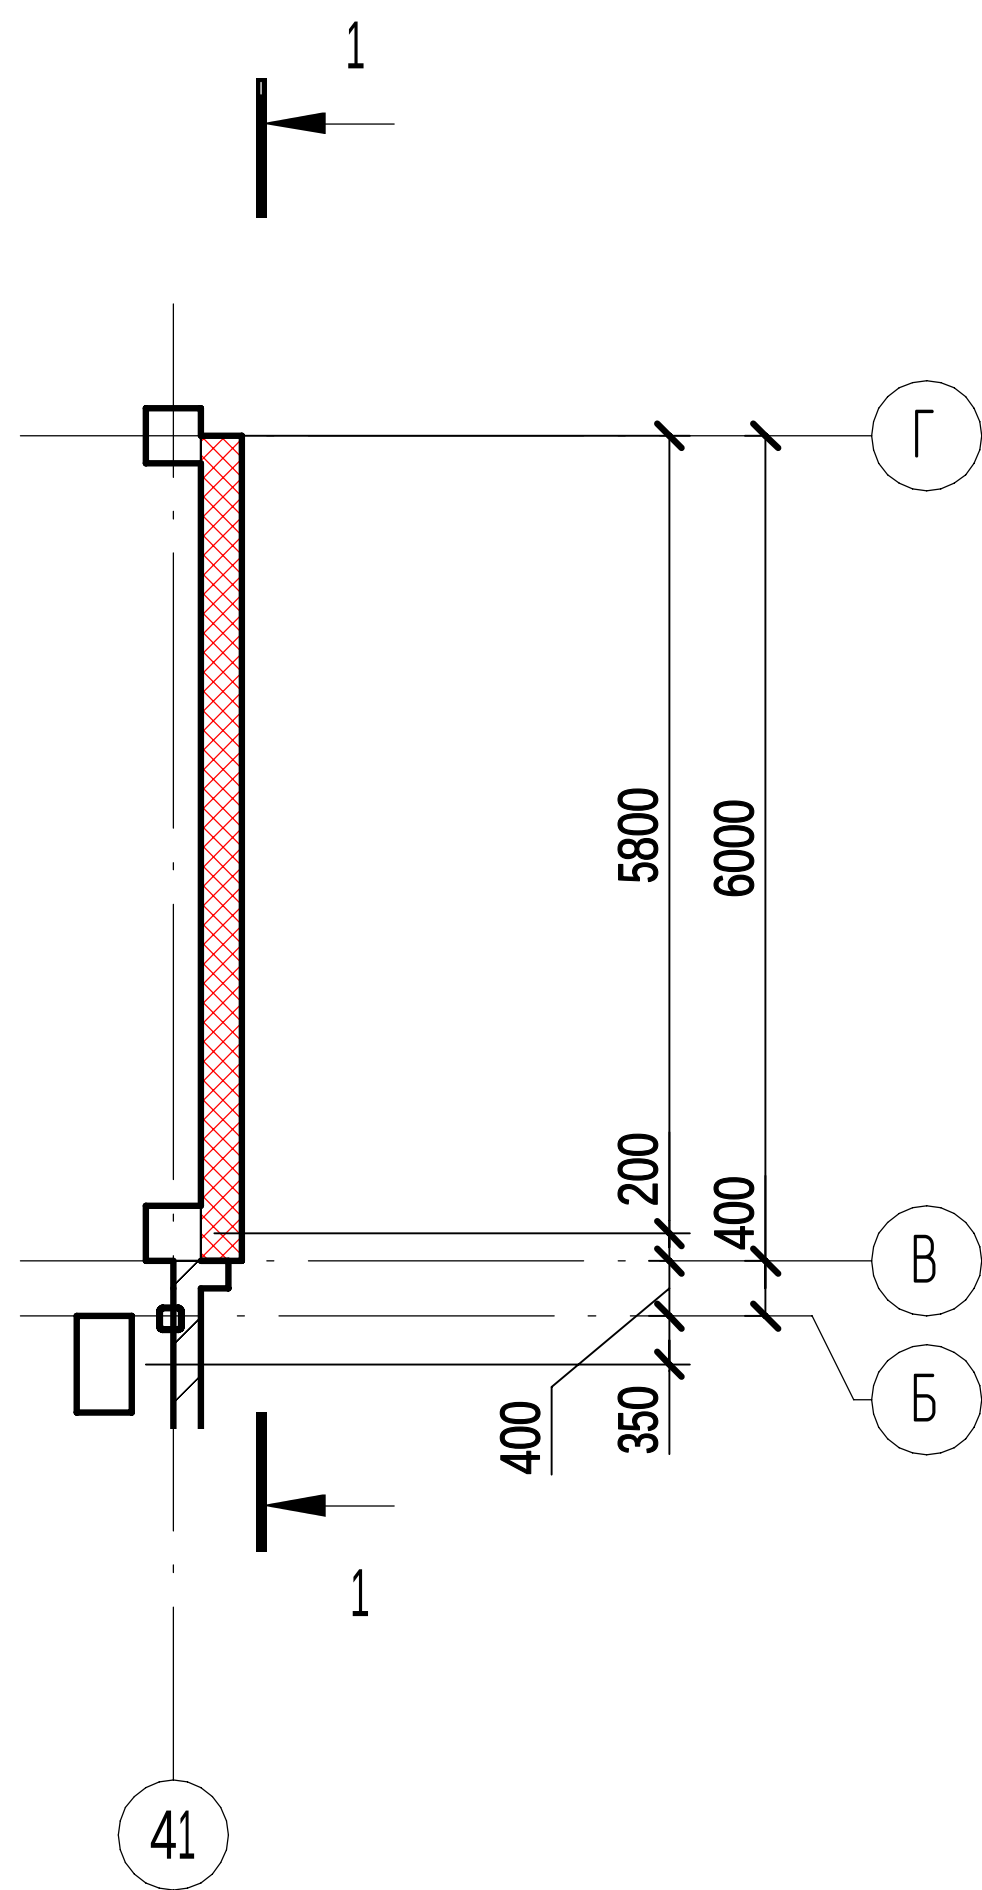


1 - 1
(1 : 100)

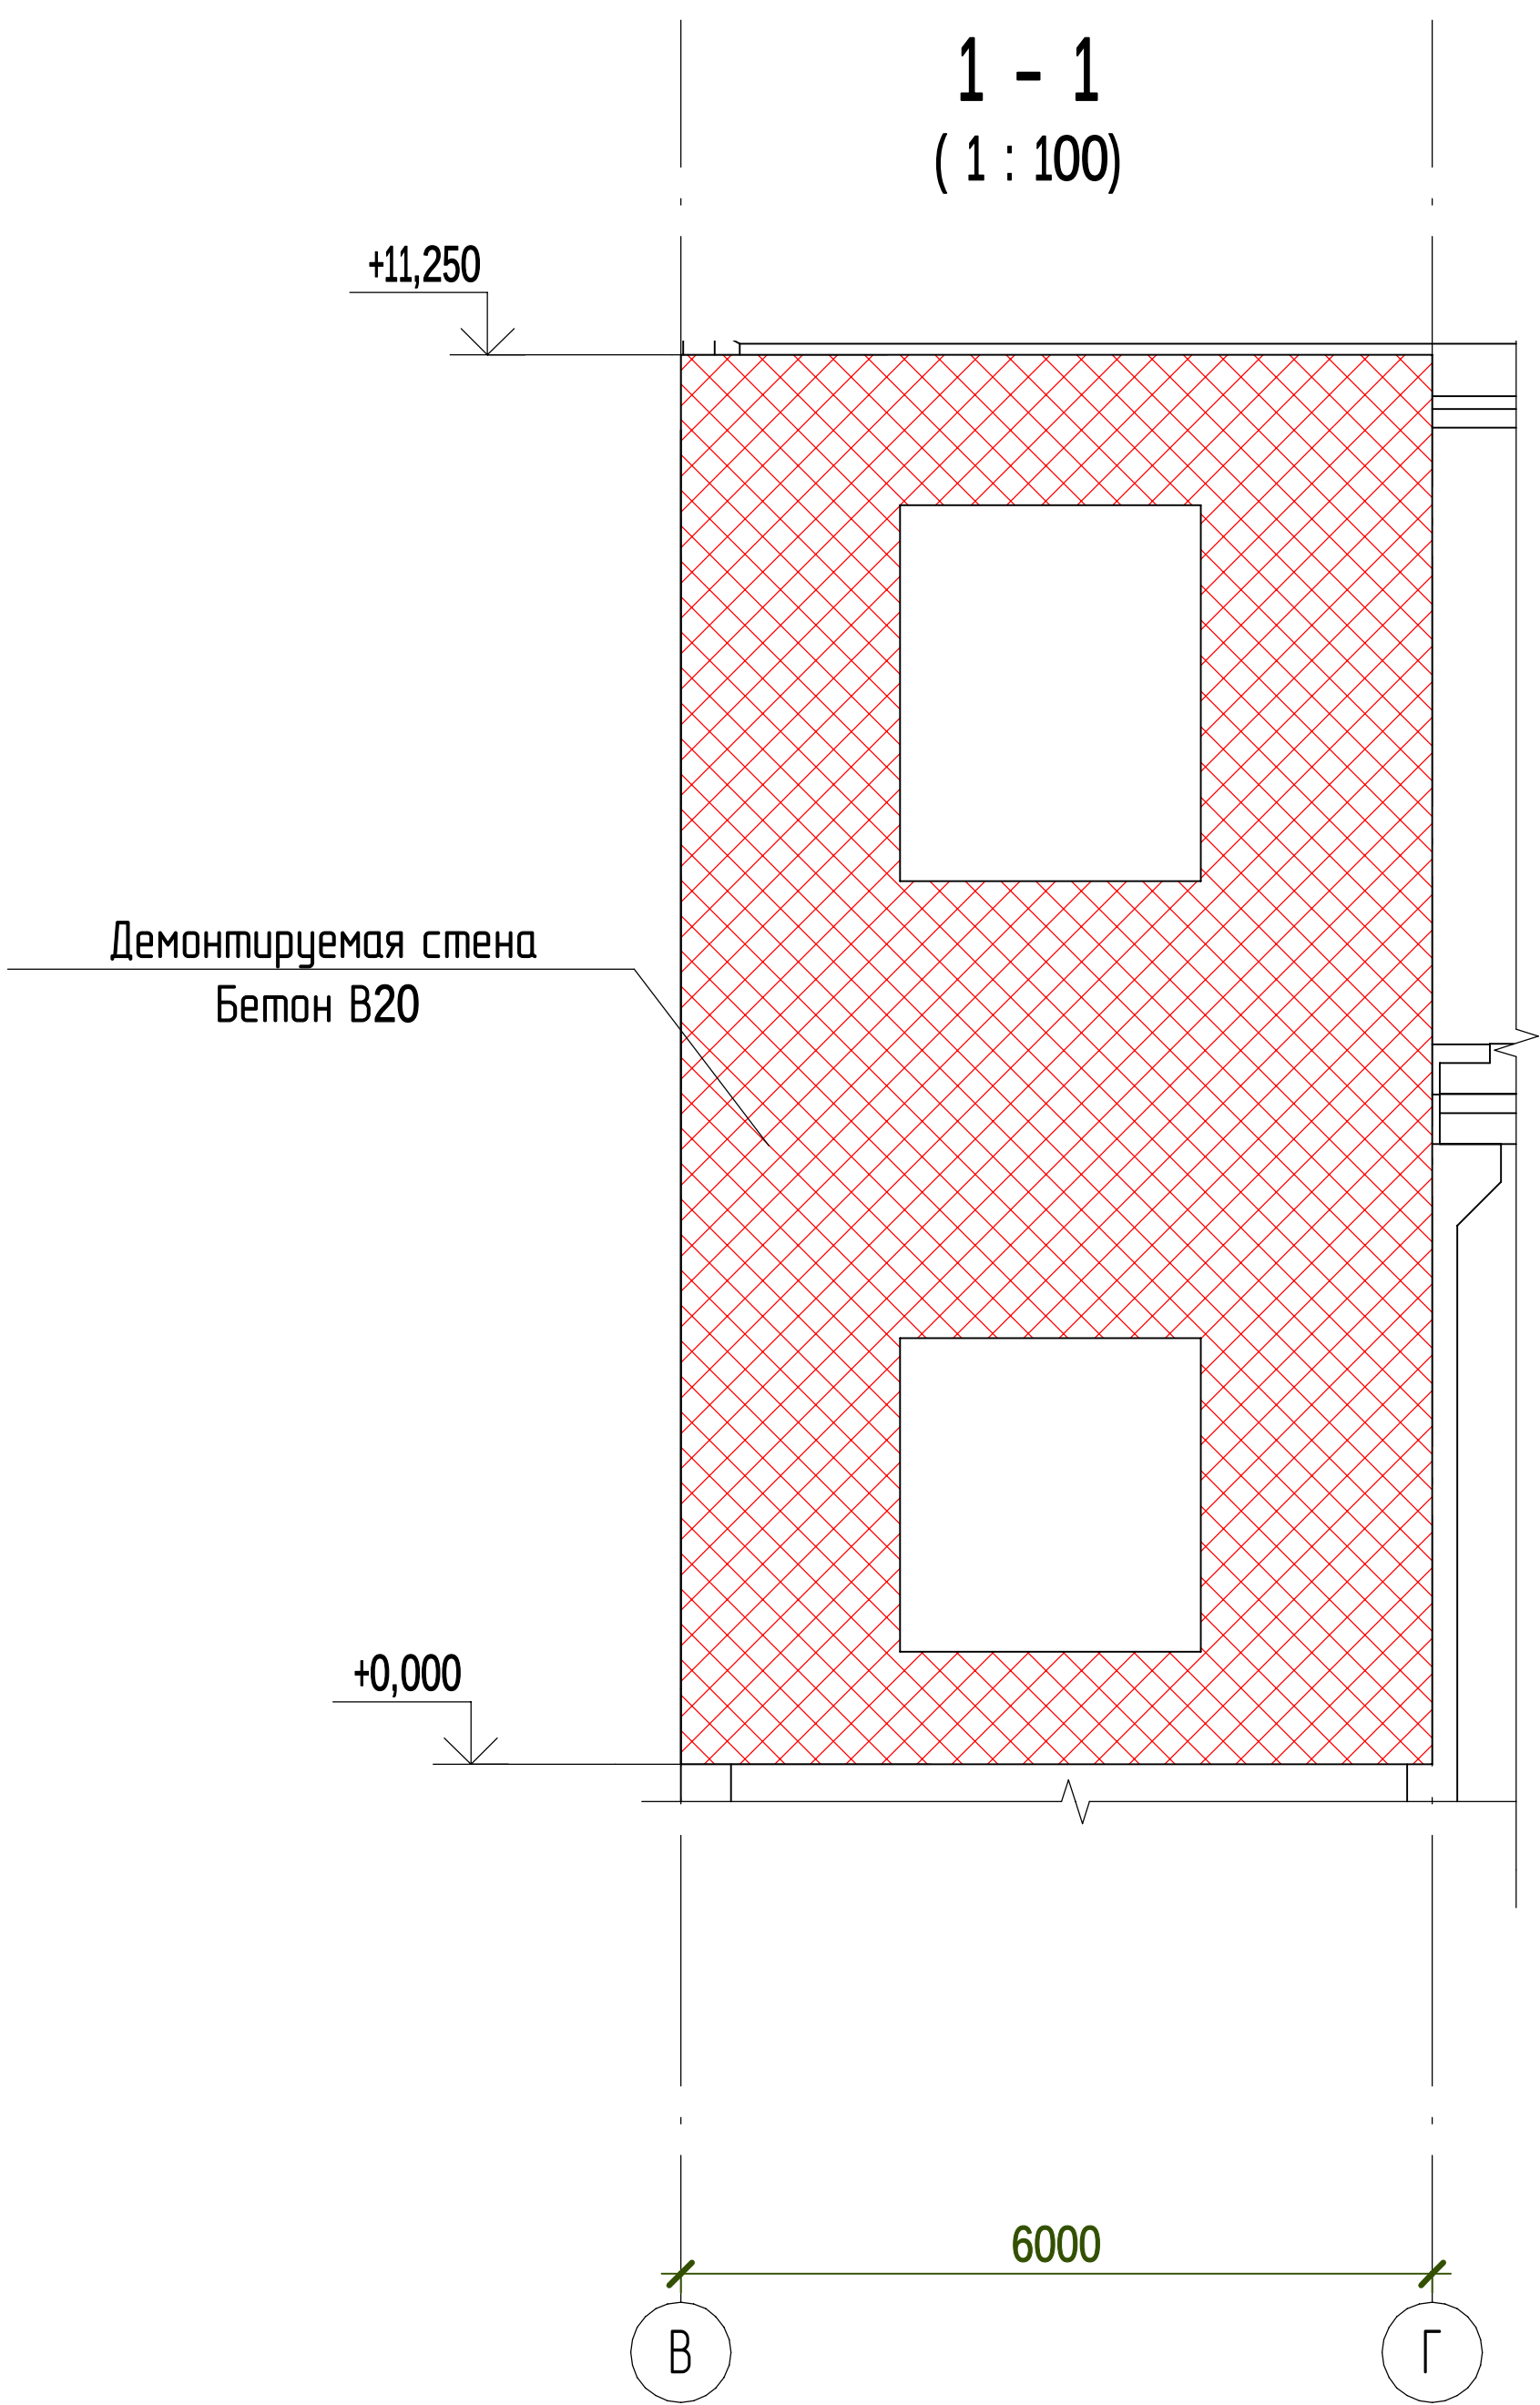

1. Объем демонтажных работ составляет 21,6 м³.

- Условные обозначения:
- Новые конструкции.
 - Демонтируемые конструкции
 - Существующие конструкции

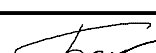						20-08 - АС			
						ООО «Производственное оборудование»			
Изм.	Колуч.	Лист	№ док.	Подпись	Дата	Реконструкция здания цеха комплектации колес, по адресу: г. Липецк, ул. Чехова,12	Стадия	Лист	Листов
Разработал	Белокопытов						Р	7	
Проверил	Батухтин					Схема расположения стен и колонн по оси 41 (демонтаж)			
Н. Контр.	Захаров								

Согласовано			
	Изд. № подл.	Подп. и дата	Взам. инв. №

Схема расположения плит покрытия в осях А-Д/1-21 (демонтаж)
(1 : 200)


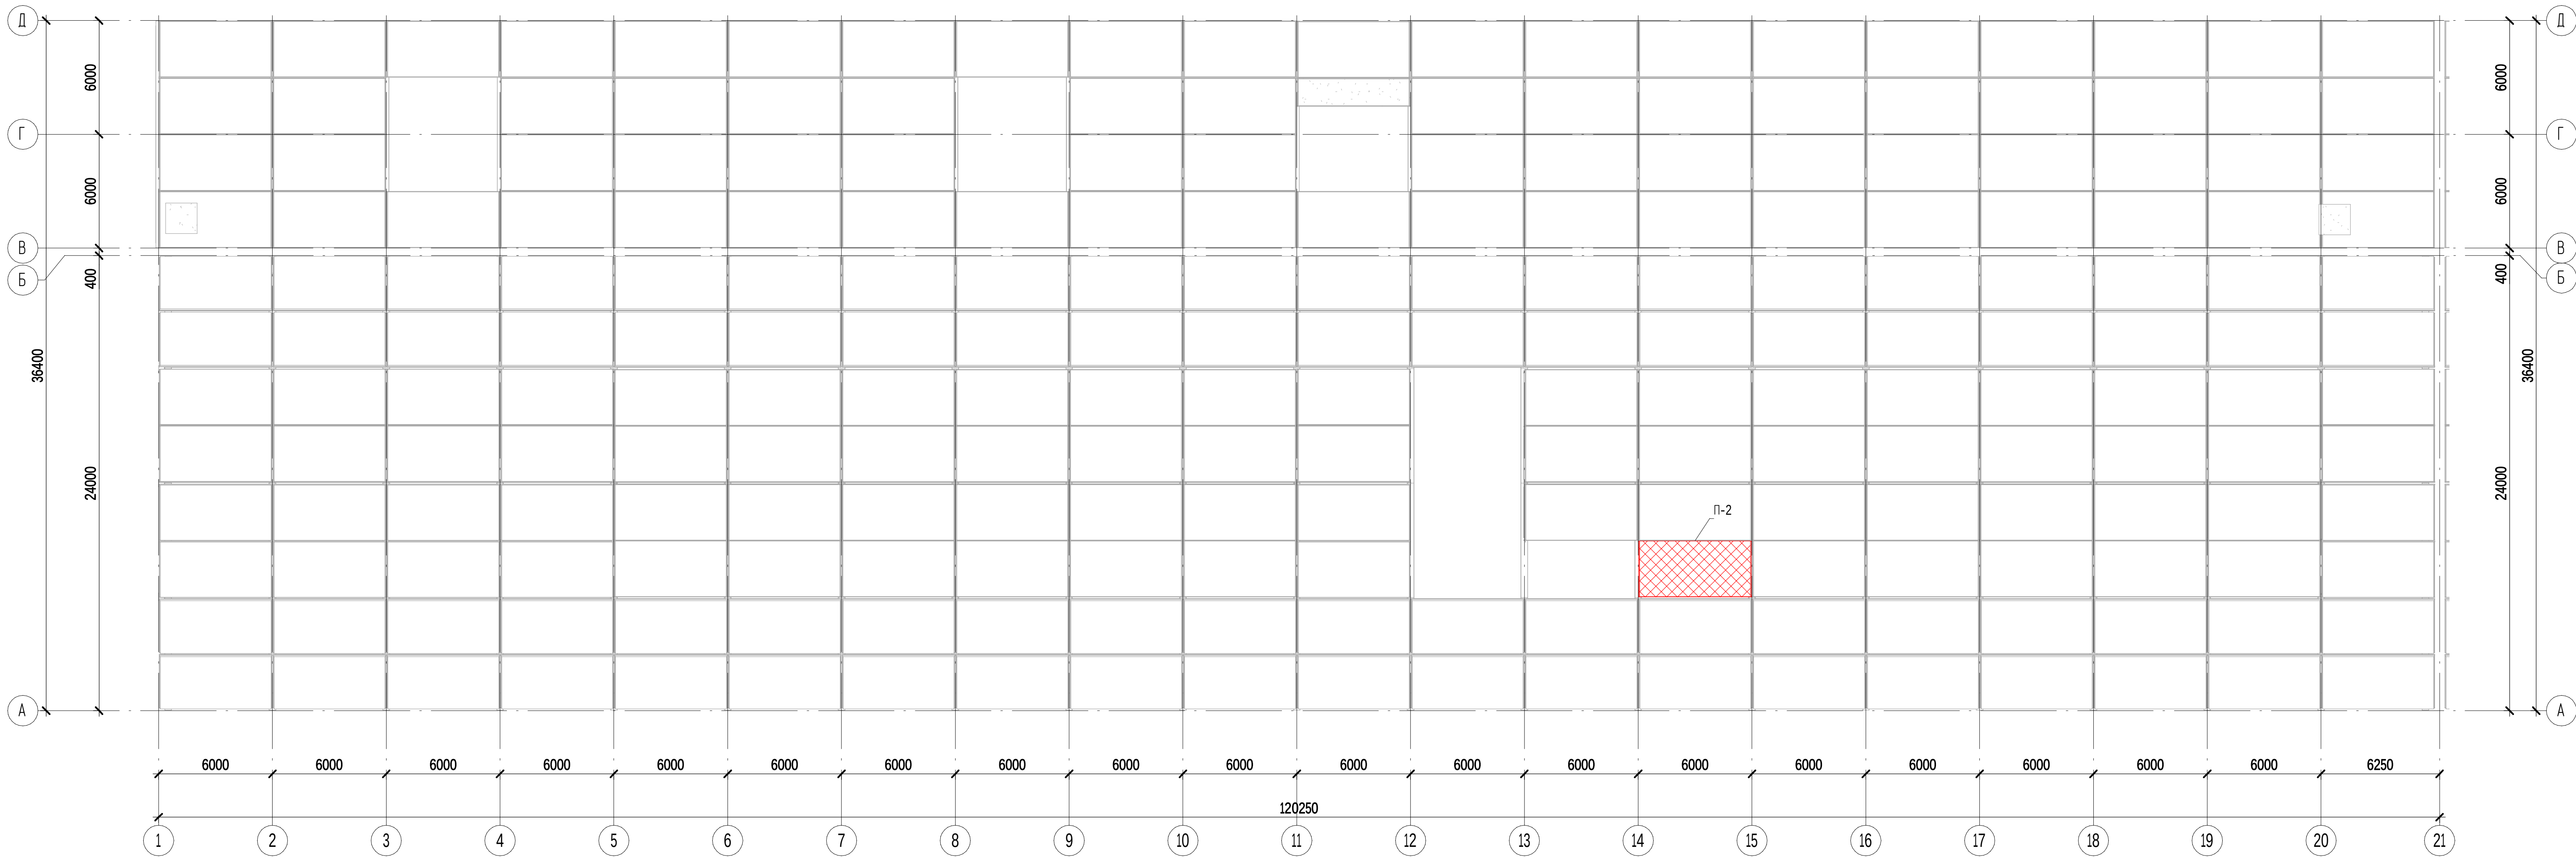


Схема расположения плит покрытия в осях А-Д/21-41 (демонтаж)
(1 : 200)

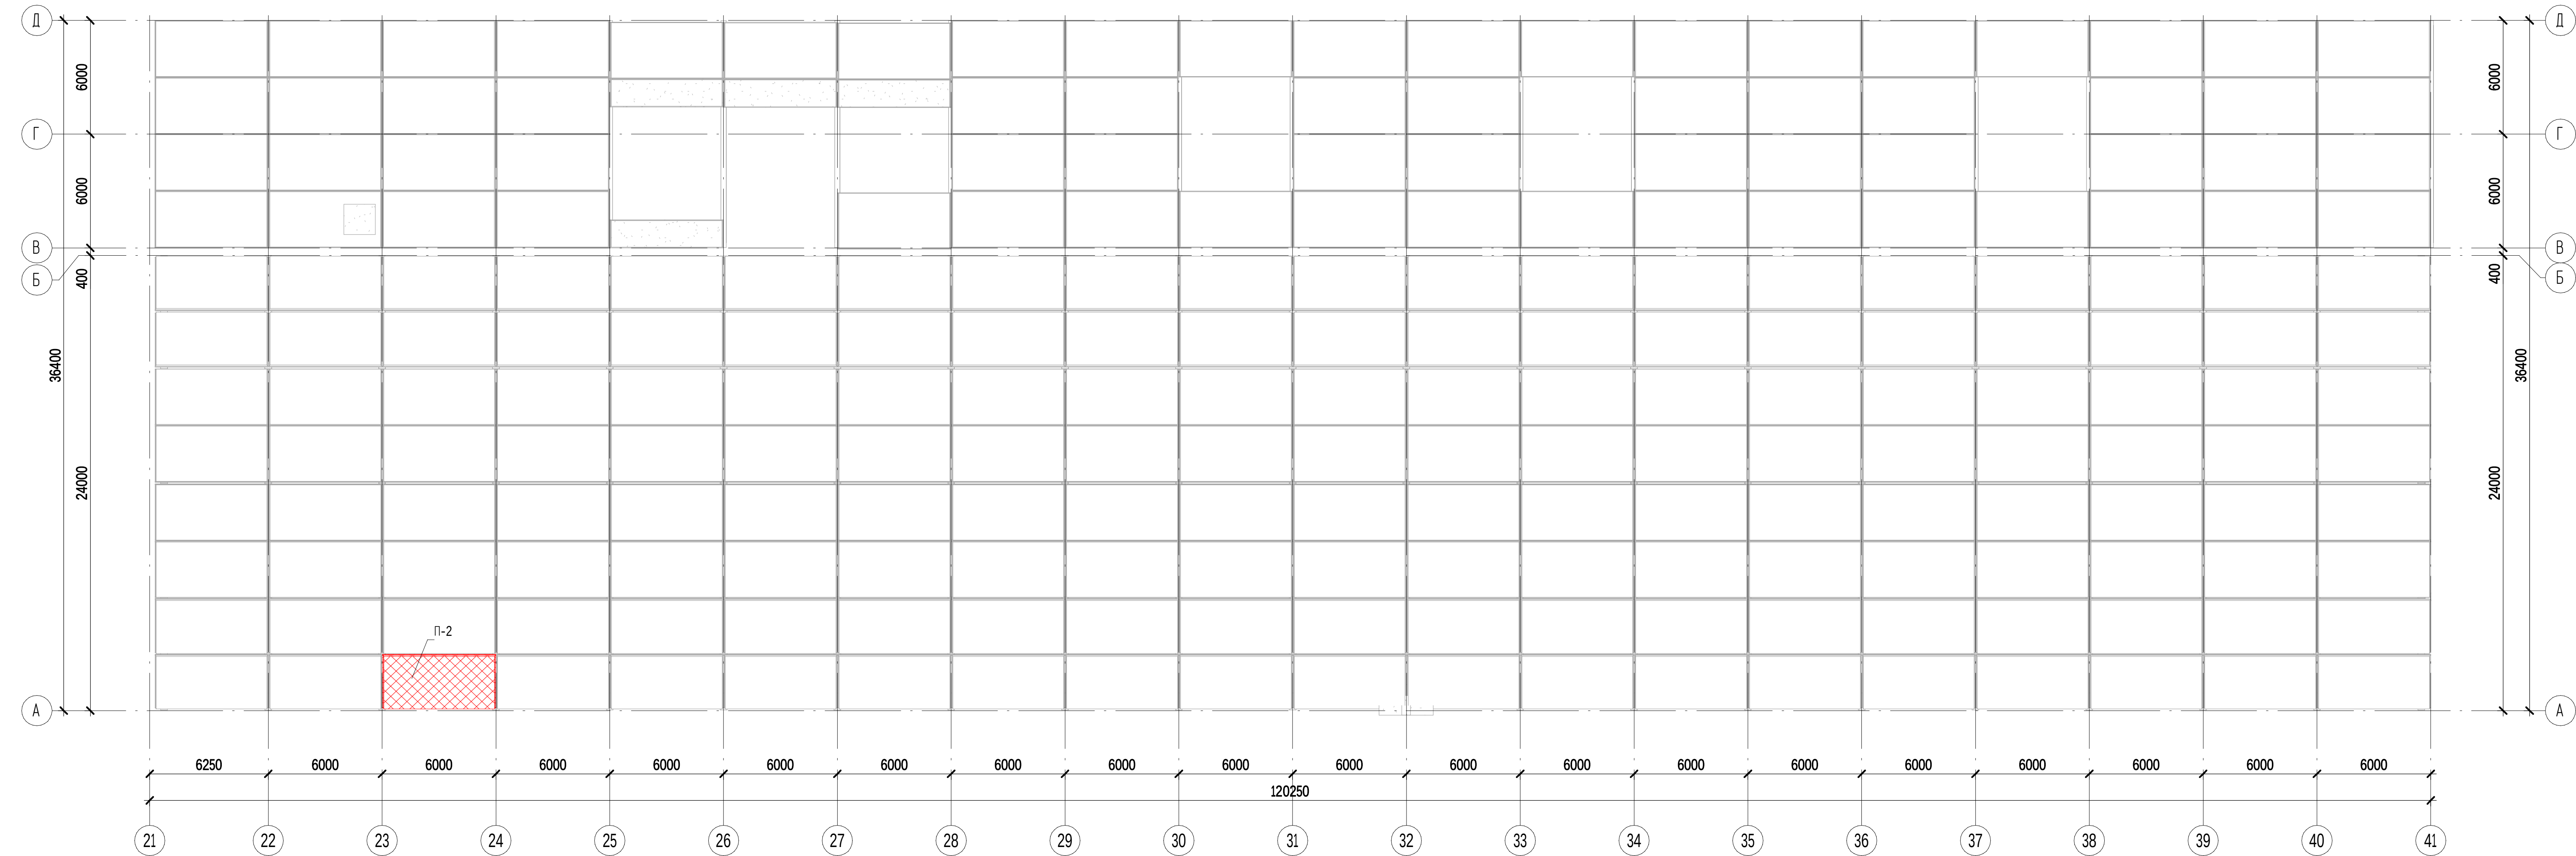


Спецификация к схеме расположения плит покрытия (демонтаж)

Марка	Обозначение	Наименование	Кол-во, шт	Примечание
П-1	Серия 1.465.1-3/80	ЛПГ-12-3К71 11960х2980	3	6200 кг
П-2	Серия ПК-01-74/62	ПКС-4/3х6 5960х2980	2	2330 кг

- Условные обозначения:
- Новые конструкции
 - Демонтируемые конструкции
 - Существующие конструкции

						20-08 - АС										
						ООО «Производственное оборудование»										
Изм.	Колуч.	Лист	№ док.	Подпись	Дата	Разработал Проверил	Белоконкин Батухтин	Реконструкция здания цеха комплектации колес, по адресу: г. Липецк, ул. Чехова,12								
												Схема расположения плит покрытия в осях А-Д/1-41 (демонтаж)				
												ИМБЕСТ ПРОЕКТ				

Согласовано		Подп. и дата	Взам. инд. №
Инж. № подл.			

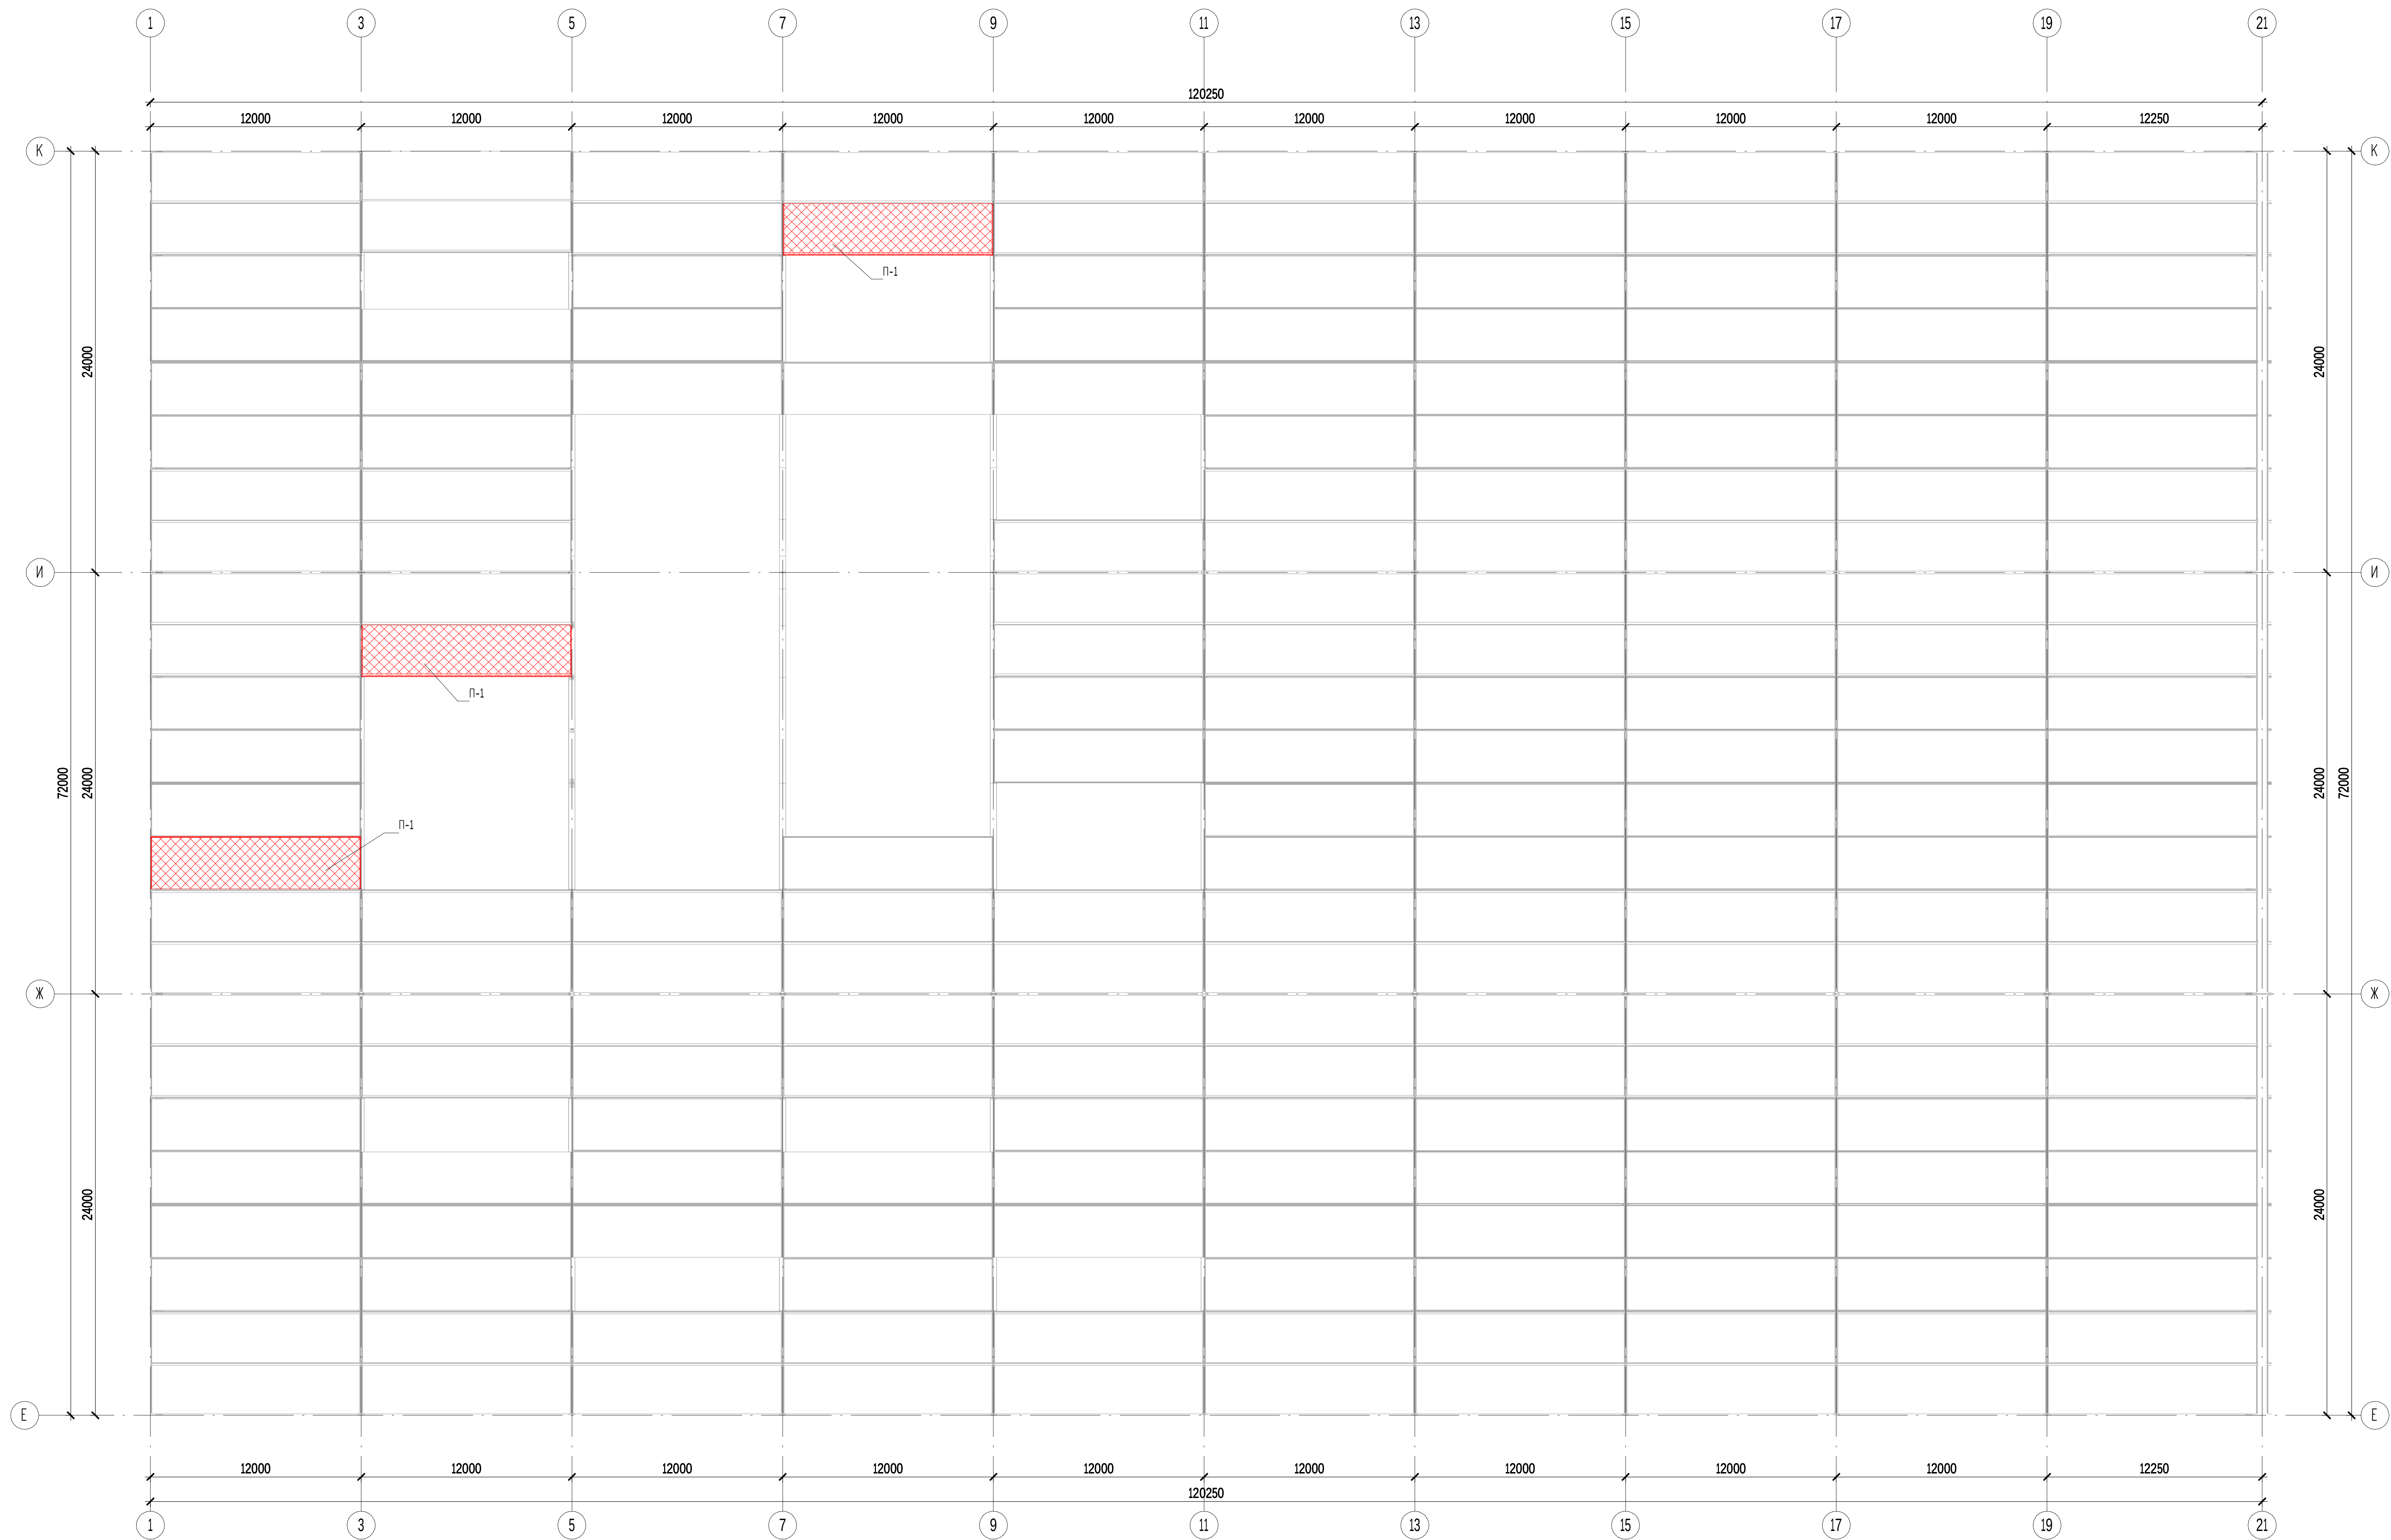

- Условные обозначения:
- Новые конструкции.
 - Демитируемые конструкции
 - Существующие конструкции

						20-08 - АС		
						ООО «Производственное оборудование»		
Изм.	Колуч.	Лист	№ док.	Подпись	Дата	Реконструкция здания цеха комплектации колес, по адресу: г. Липецк, ул. Чехова, 12	Стация	Лист
Разработал	Белокапитов						Р	9
Проверил	Батушкин					Схема расположения плит покрытия в осях Е-К/1-21 (демонтаж)	ТЕХ ИМБЕСТ ПРОЕКТ	
Н. Контр.	Захаров							

Схема расположения плит покрытия в осях А-Д/1-21 (монтаж)
(1 : 200)


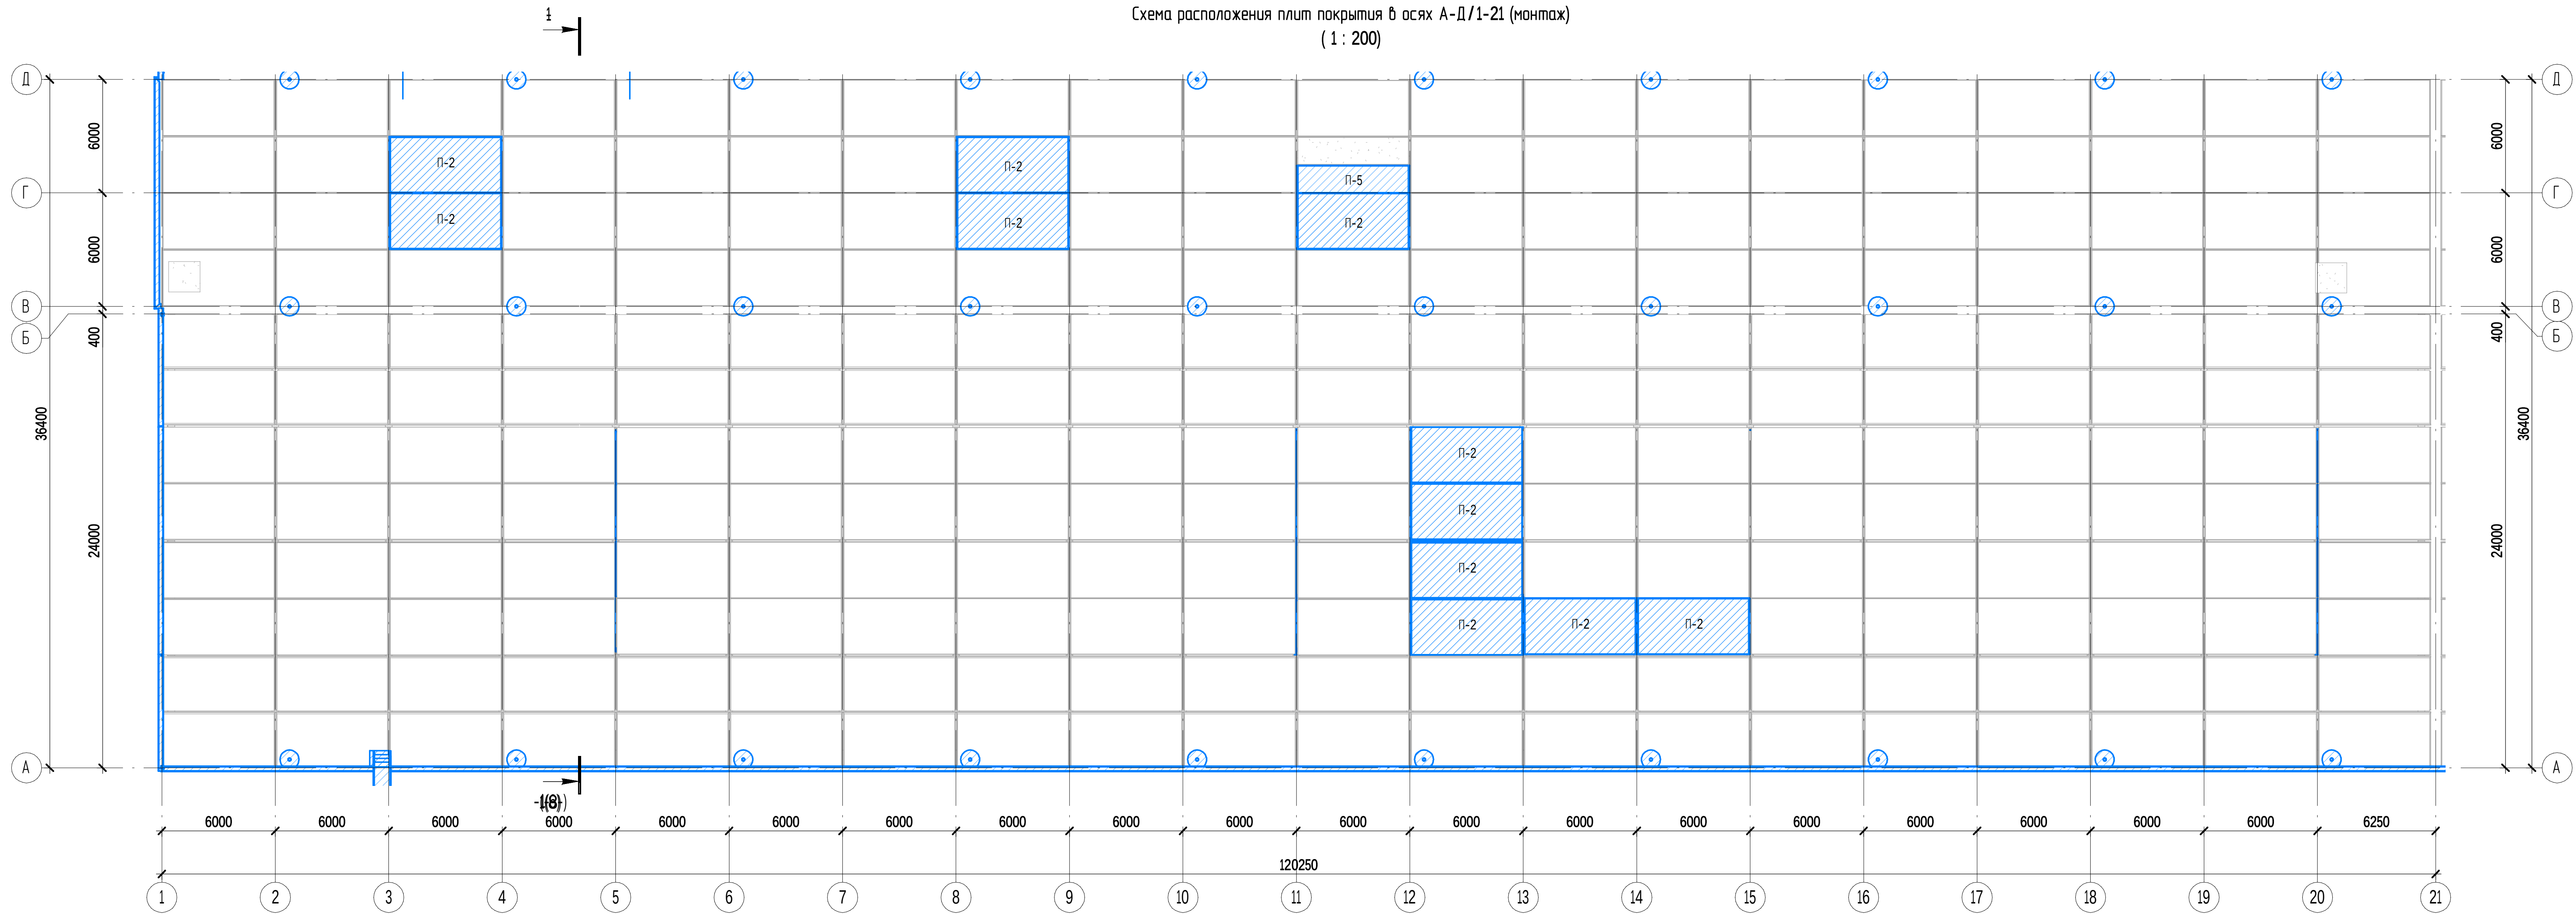


Схема расположения плит покрытия в осях А-Д/21-41 (монтаж)
(1 : 200)

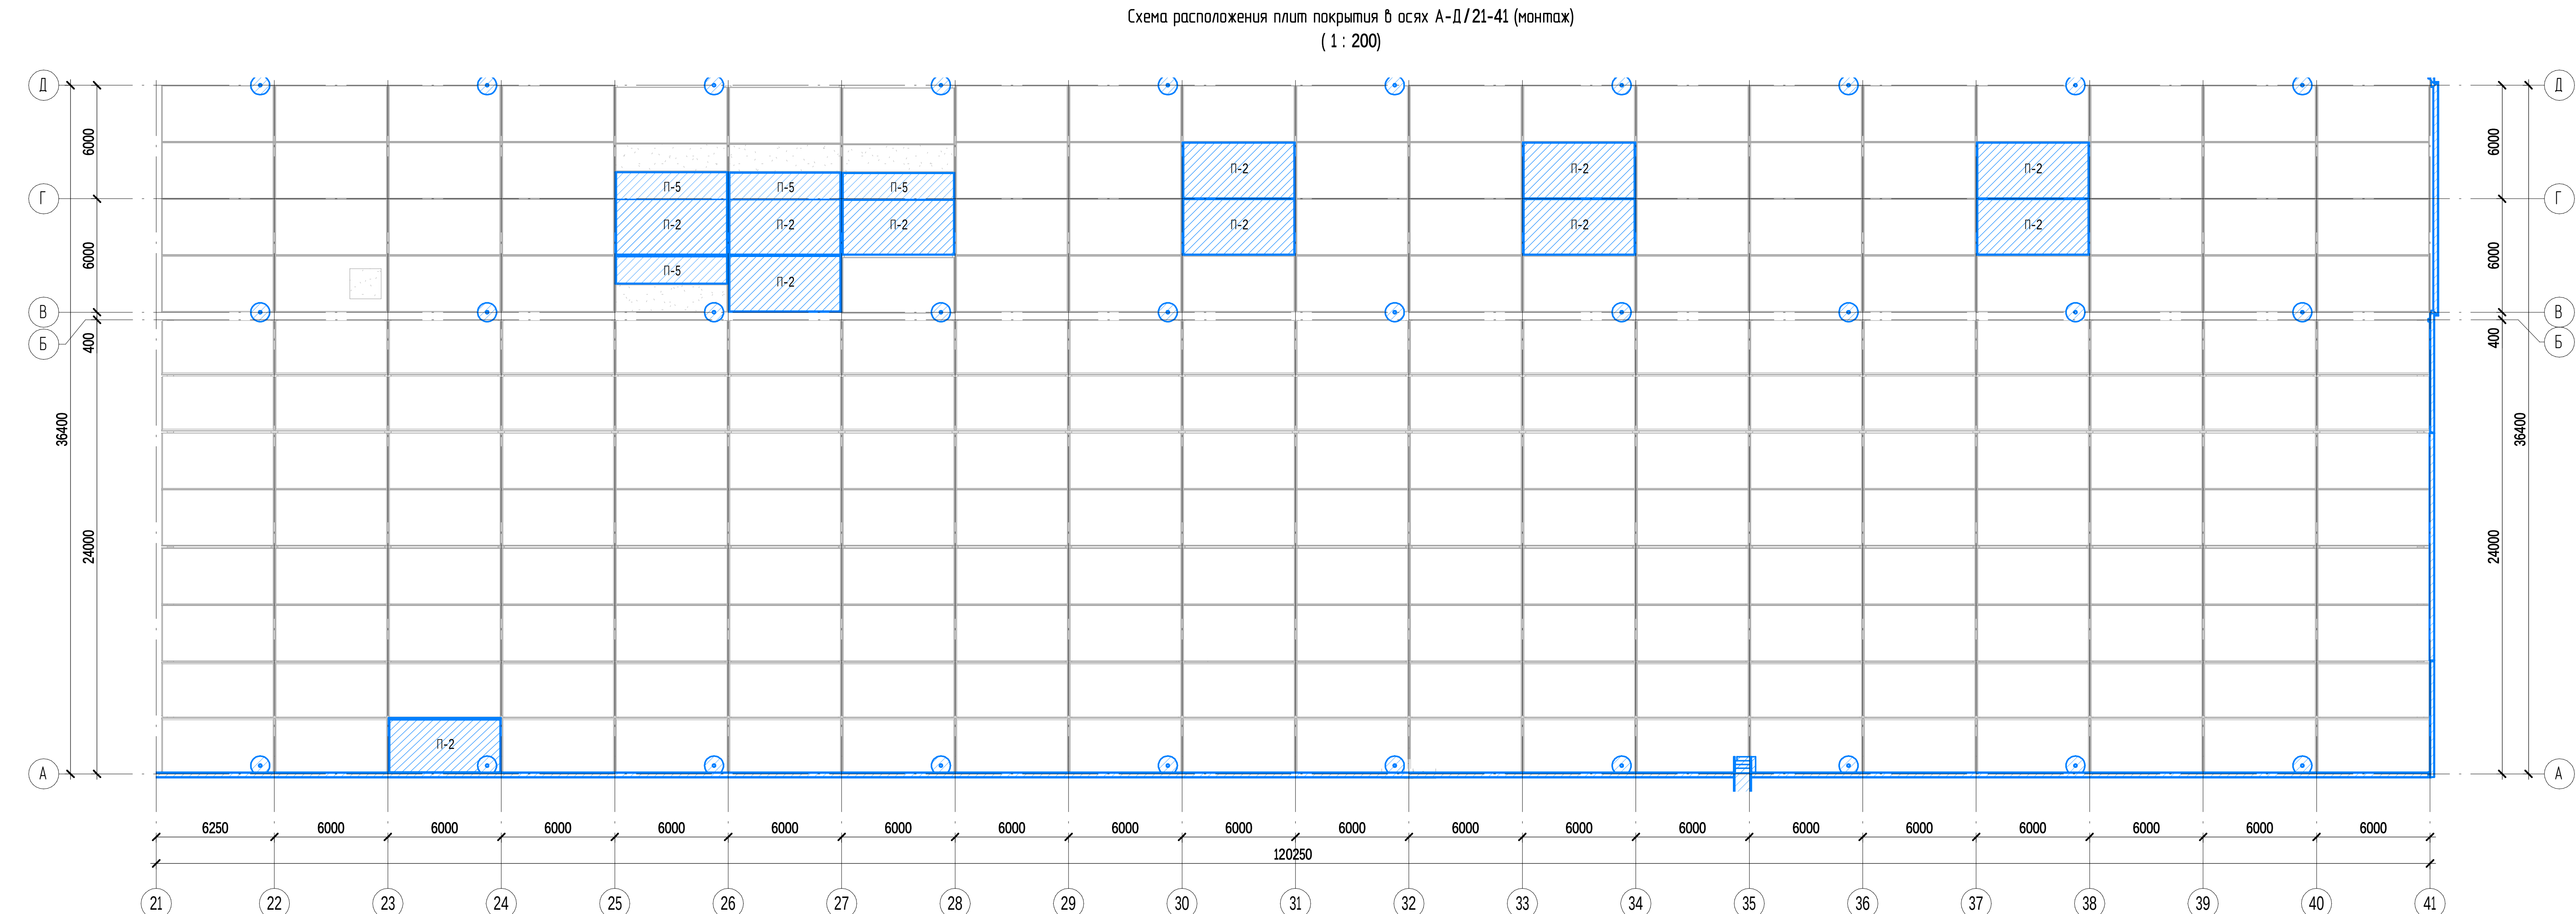


Спецификация к схеме расположения плит покрытия и перекрытия (новые)

Марка	Обозначение	Наименование	Кол-во, шт	Примечание
П-1	Серия 1.465.1-3/80	ЛП-12-3К7Т 11960х2980	54	6200 кг
П-2	Серия ПК-01-74/62	ЛНС-4/3х6 5960х2980	22	2330 кг
П-4	Серия ИИ24-11	ПЗ-9/0.75х6 5620х735	4	1500 кг
П-5	Серия ПК-01-111	ЛНС-12/1.5х6 5960х480	5	1370 кг

- Условные обозначения
- Новые конструкции.
 - Демонтируемые конструкции
 - Существующие конструкции

						20-08 - АС		
						ООО «Производственное оборудование»		
Изм.	Кол-во	Лист	№ док.	Подпись	Дата	Реконструкция здания цеха комплектации колес, по адресу: г. Липецк, ул. Чехова, 12	Стандарт	Лист
Разработал	Белоконный	Батуткин					Р	10
Н. Контр.	Захаров					Схема расположения плит покрытия в осях А-Д/1-41 (монтаж)	ТЕХ ИМБЕСТ ПРОЕКТ	

Составлено		Изм. №		Дата		Взам. инв. №	
Изм. №		Изм. №		Изм. №		Изм. №	
Изм. №		Изм. №		Изм. №		Изм. №	

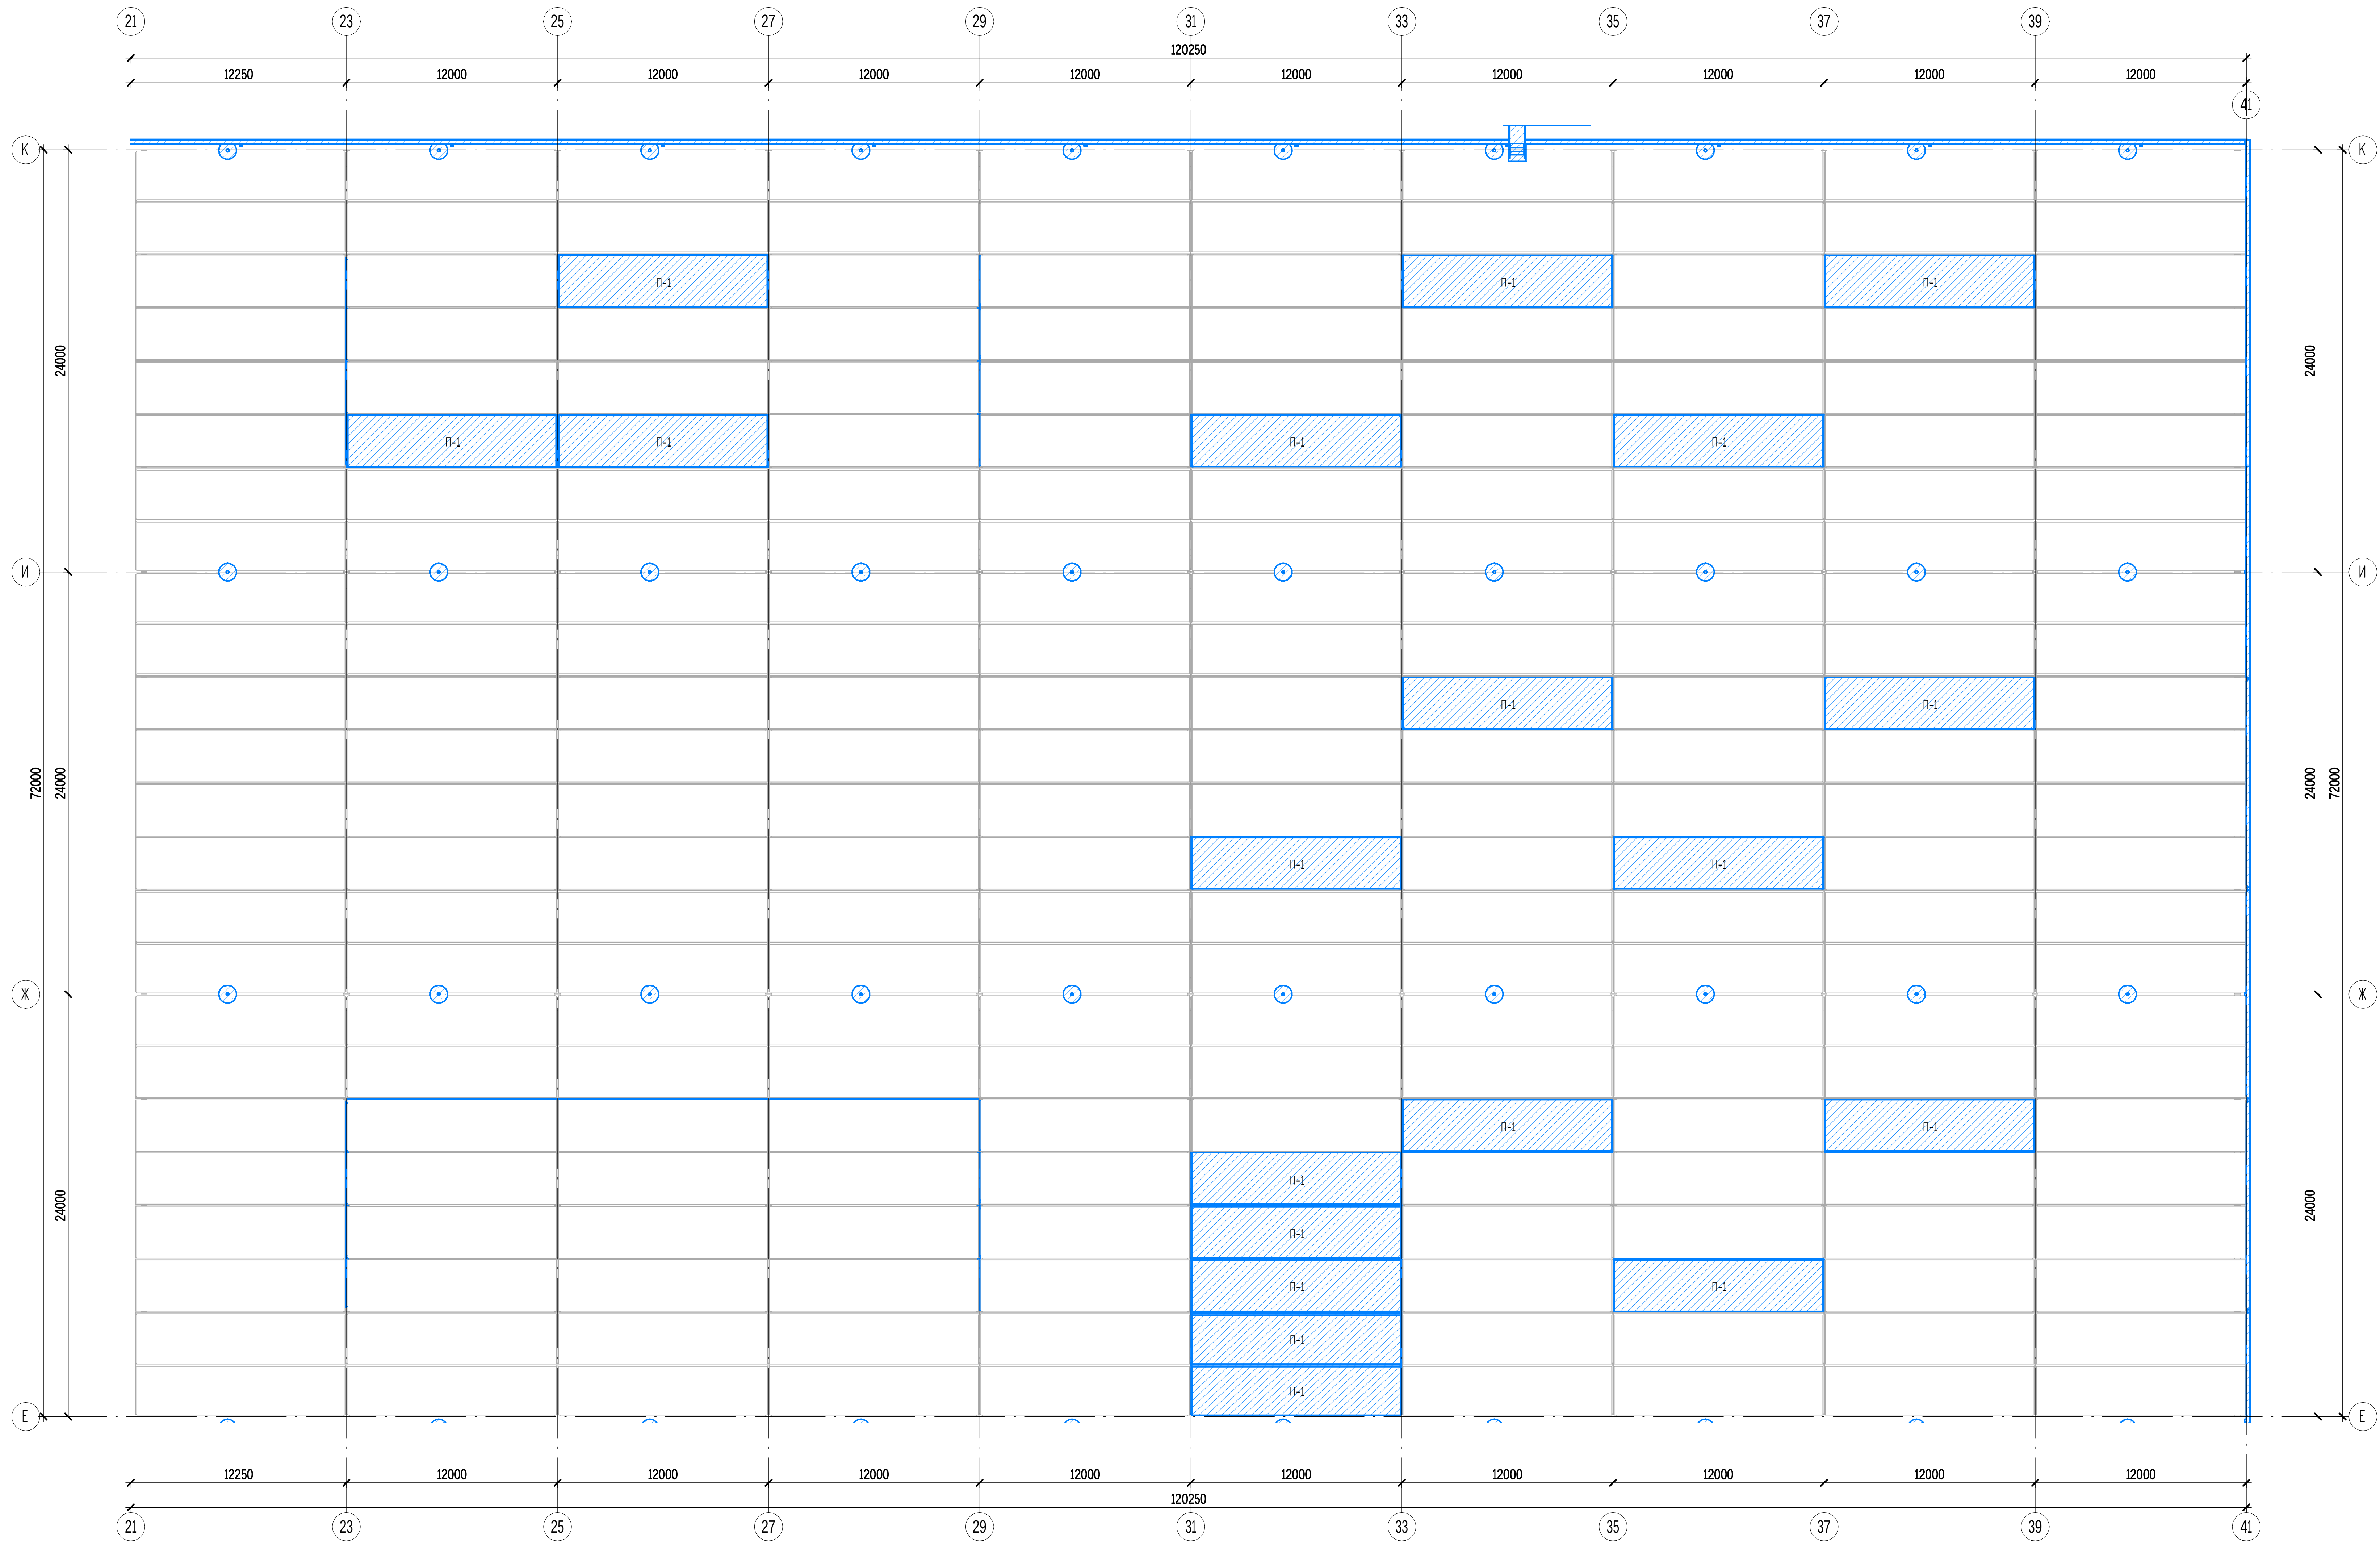

- Условные обозначения:
- Новые конструкции.
 - Демонтируемые конструкции.
 - Существующие конструкции.

						20-08 - АС		
						ООО «Производственное оборудование»		
						Реконструкция здания цеха комплектации колес, по адресу: г. Липецк, ул. Чехова, 12		
						Стация	Лист	Листов
						Р	12	
						Схема расположения плит покрытия в осях Е-К/21-41 (монтаж)		
						ТЕХ ИМБЕСТ ПРОЕКТ		
						АД		

Согласовано			
Изм. № подл.	Подп. и дата	Взам. инд. №	

Схема расположения плит перекрытия на отм. +5.350 в осях 1-21 (монтаж)
(1 : 200)




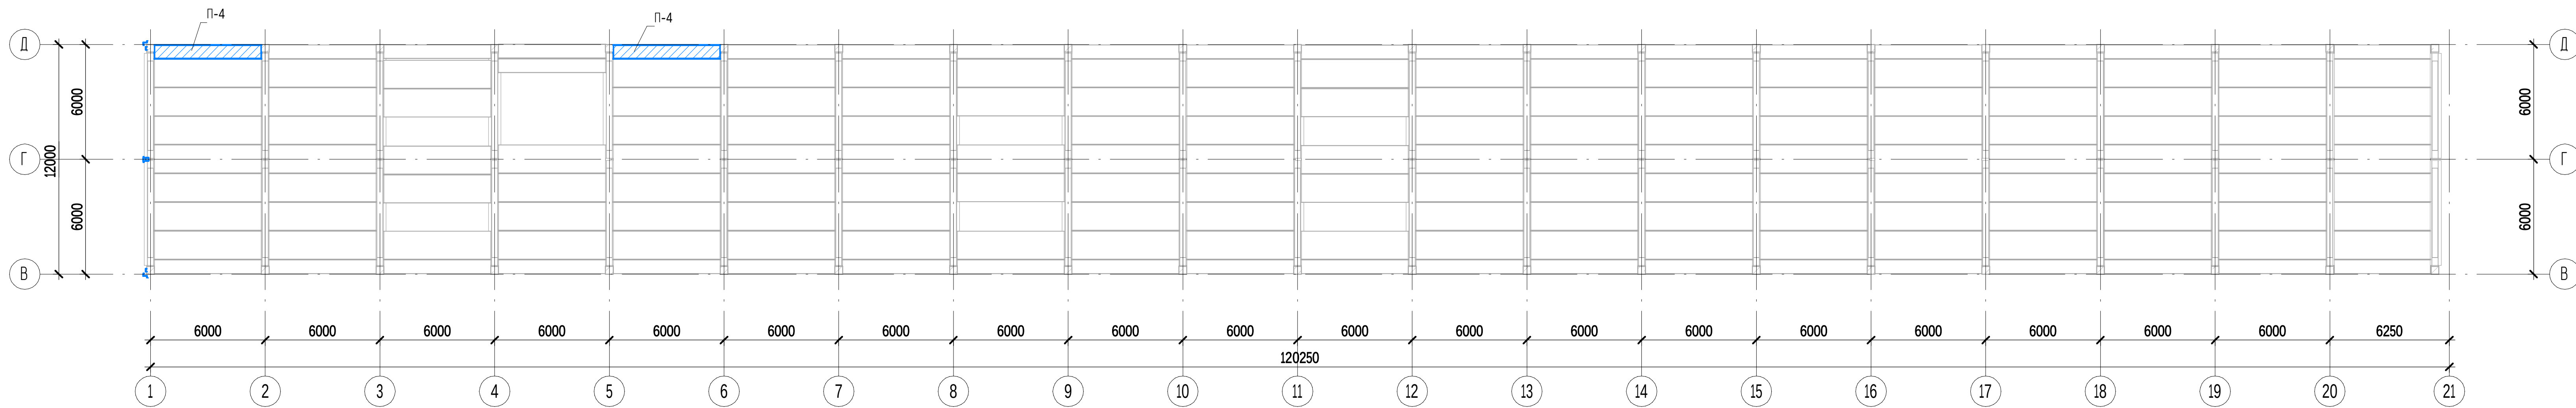


Схема расположения плит перекрытия на отм. +5.350 в осях 21-41 (монтаж)
(1 : 200)

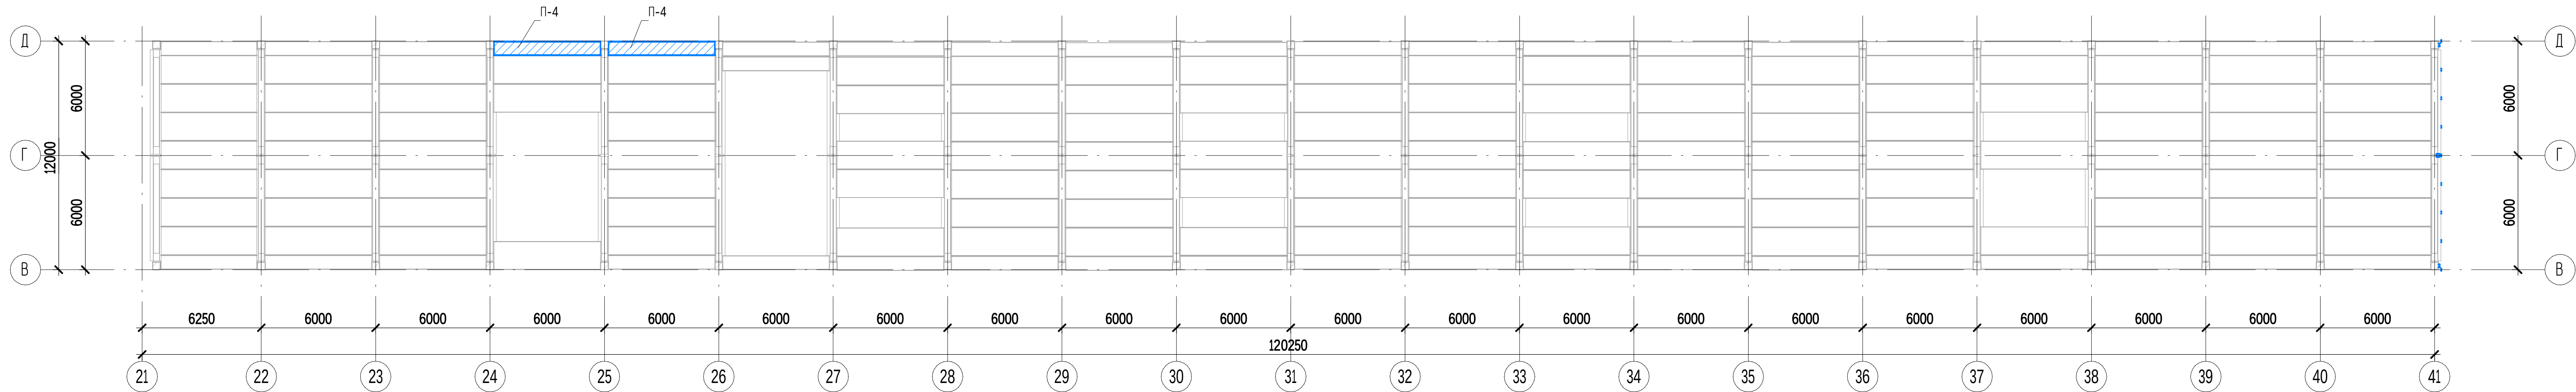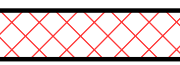 

- Условные обозначения:
-  - Новые конструкции.
 -  - Демонтируемые конструкции
 -  - Существующие конструкции

 
 
						20-08 - АС			
						ООО «Производственное оборудование»			
Изм.	Колуч.	Лист	№ док.	Подпись	Дата	Реконструкция здания цеха комплектации колес, по адресу: г. Липецк, ул. Чехова,12	Стация	Лист	Листов
Разработал	Белокапитов						Р	13	
Проверил	Батушкин					Схема расположения плит перекрытия на отм. +5.350 в осях 1-41 (монтаж)	 		
Н. Контр.	Захаров								

Схема расположения плит покрытия в осях А-Д/1-21 (ремонт)
(1 : 200)


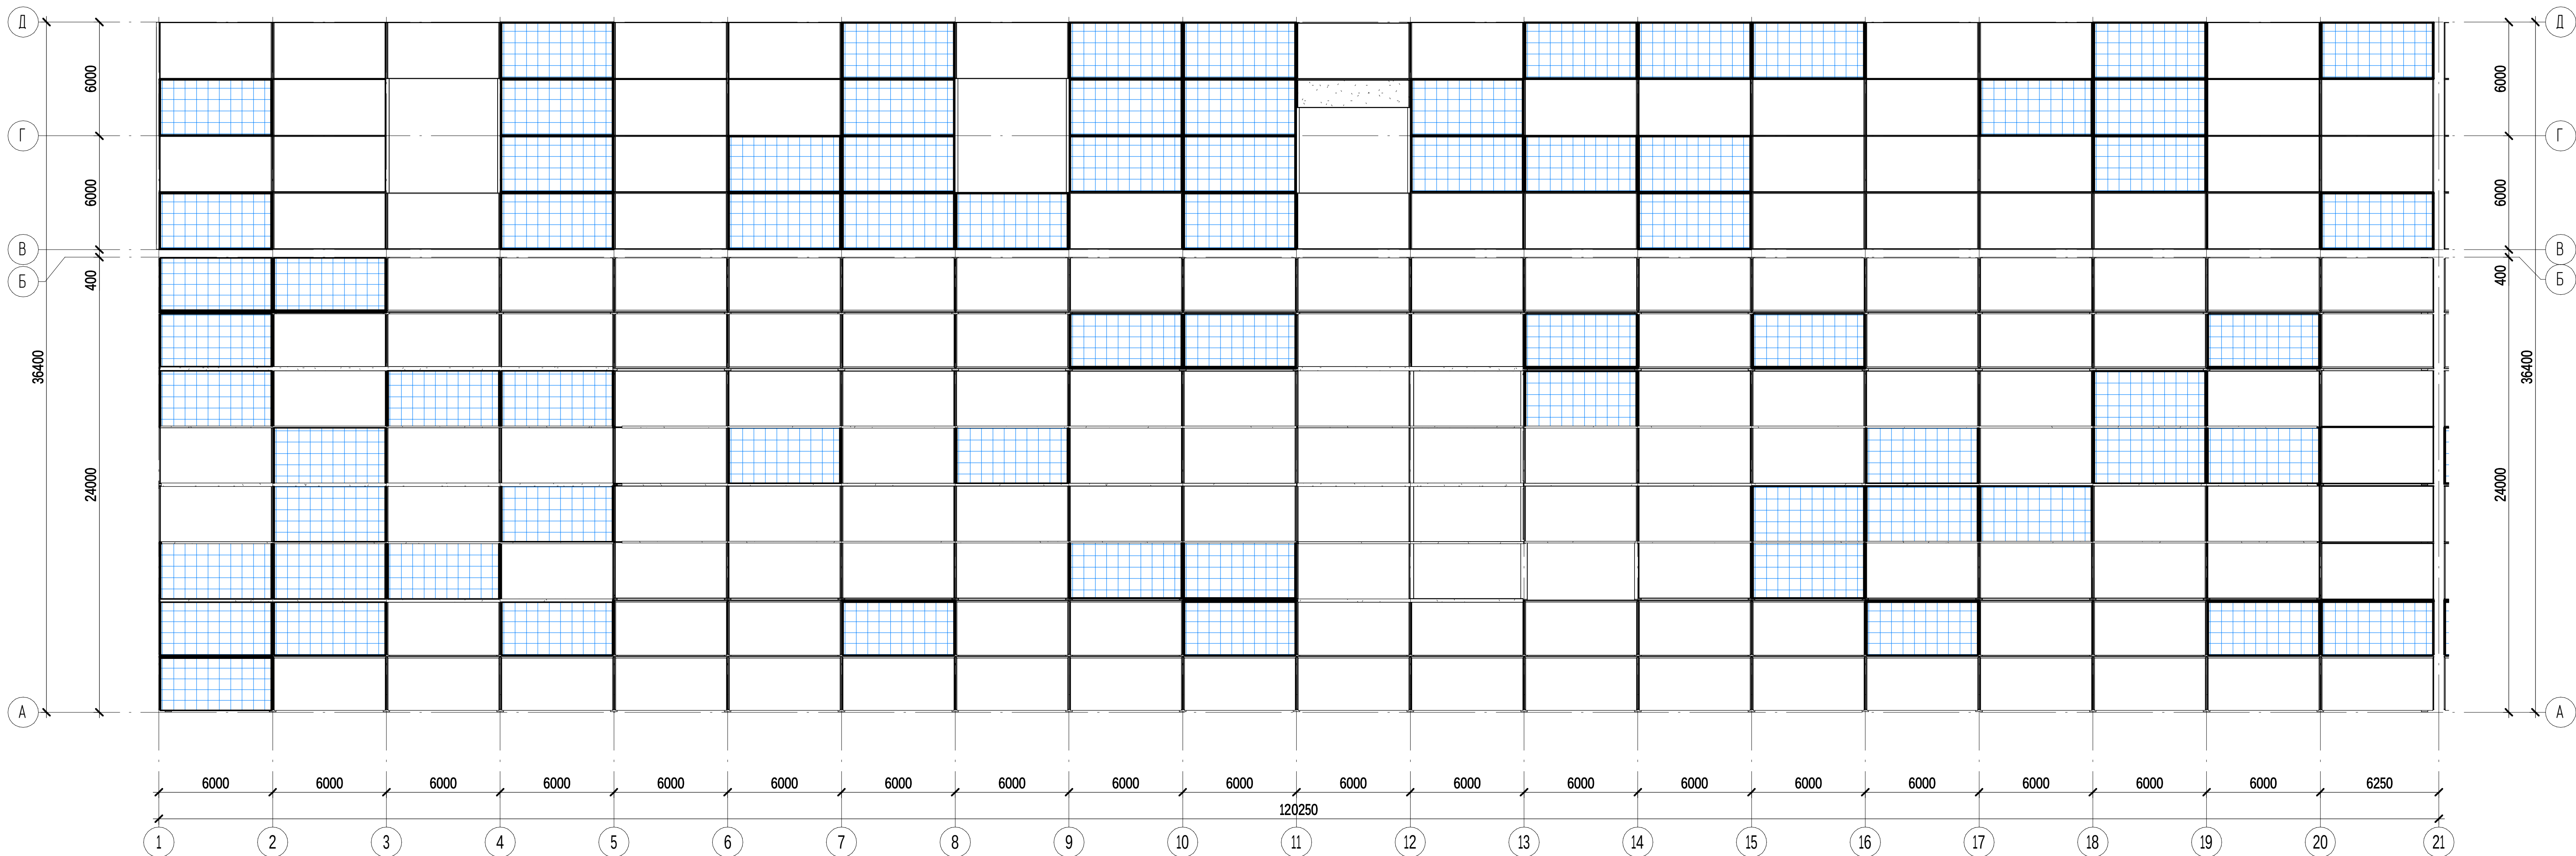


Схема расположения плит покрытия в осях А-Д/21-41 (ремонт)
(1 : 200)

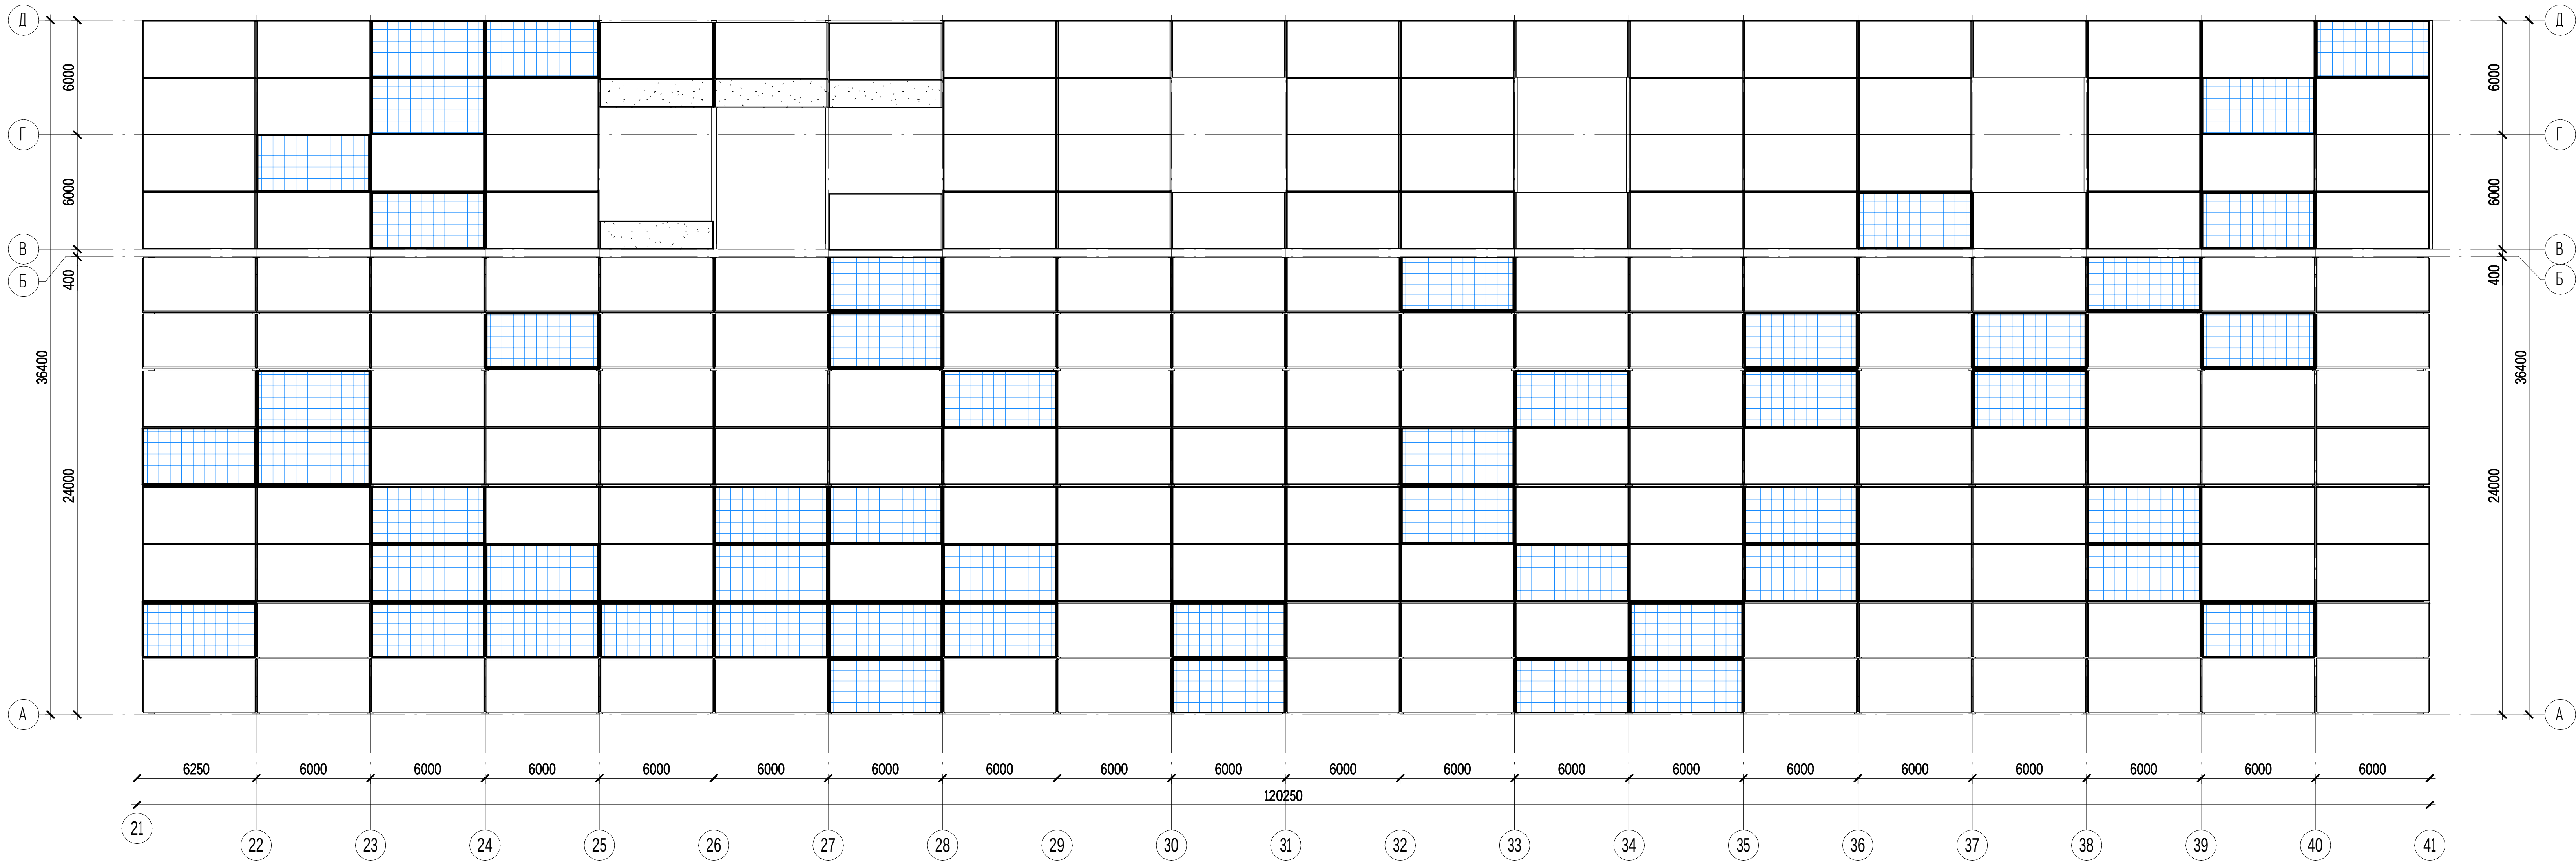

Последовательность производства работ по восстановлению несущей способности плит покрытия.


- Удалить остатки старой кровли или иных защитных покрытий до бетонной поверхности.
- Удалить все непрочные, крошащиеся части бетона, вплоть до прочного основания. При оголении арматуры, следует удалить за ней слой бетона на глубину не менее 10 мм.
- Очистить все поверхности пескоструйным методом или струей воды высокого (до 300 атмосфер) давления.
- Зачистить оголенную арматуру от следов коррозии.
- Защитить арматуру «КТран-праймер».
- Выполнить ремонт трещин в полках плит материалом КТран -2.
- Выполнить ремонт крупных дефектов, заполнить литьевым ремонтным материалом «КТран-3/1600» в заранее установленную опалубку. После снятия опалубки углы скруглить.
- Восстановление защитного слоя бетона выполнить с помощью тиксотропного ремонтного материала «КТран-31500», методом его сплошного нанесения.

Условные обозначения:


- Восстановление защитного слоя по всей плите
- Восстановление защитного слоя по половине плиты

1. Заделку трещин выполнять по всем плитам покрытия.

						20-08 - АС		
						ООО «Производственное оборудование»		
						Реконструкция здания цеха комплектации колес, по адресу: г. Липецк, ул. Чехова, 12		
						Стация	Лист	Листов
						Р	14	
						Схема расположения плит покрытия в осях А-Д/1-41 (ремонт)		
						ТЕХ ИМБЕСТ ПРОЕКТ		

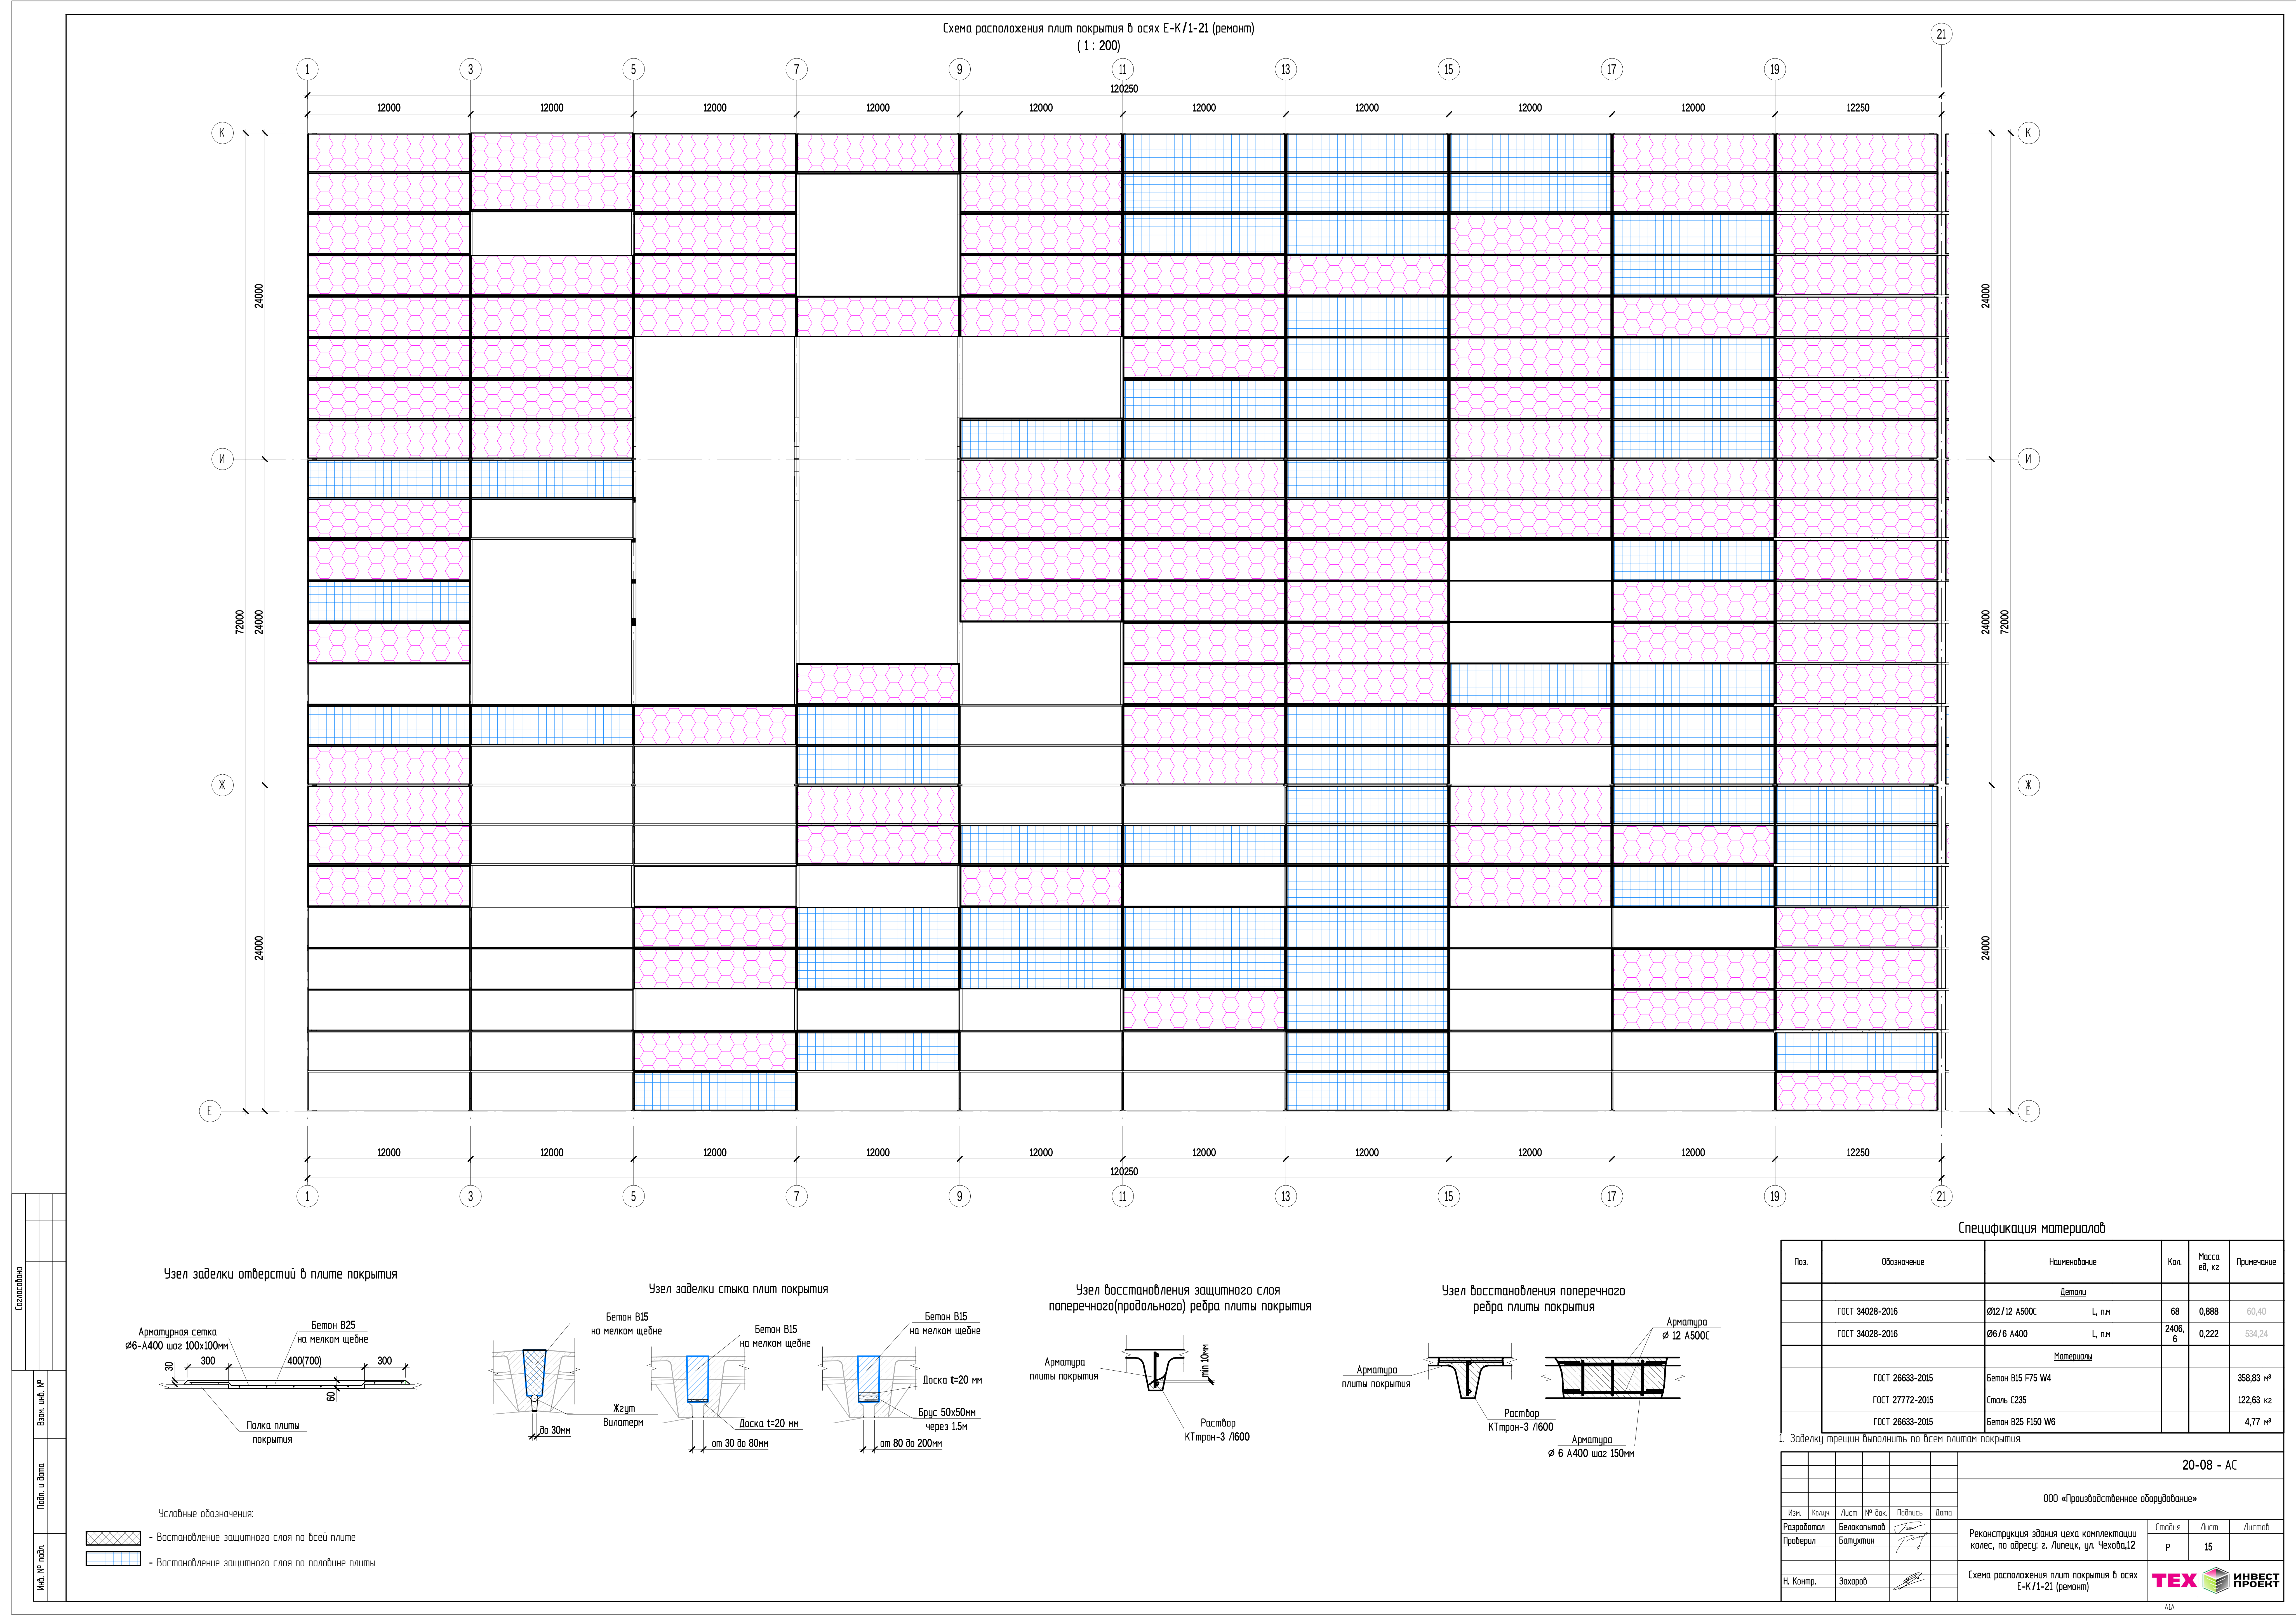

Согласовано		Взам. инв. №	
Инв. № подл.		Лист и дата	

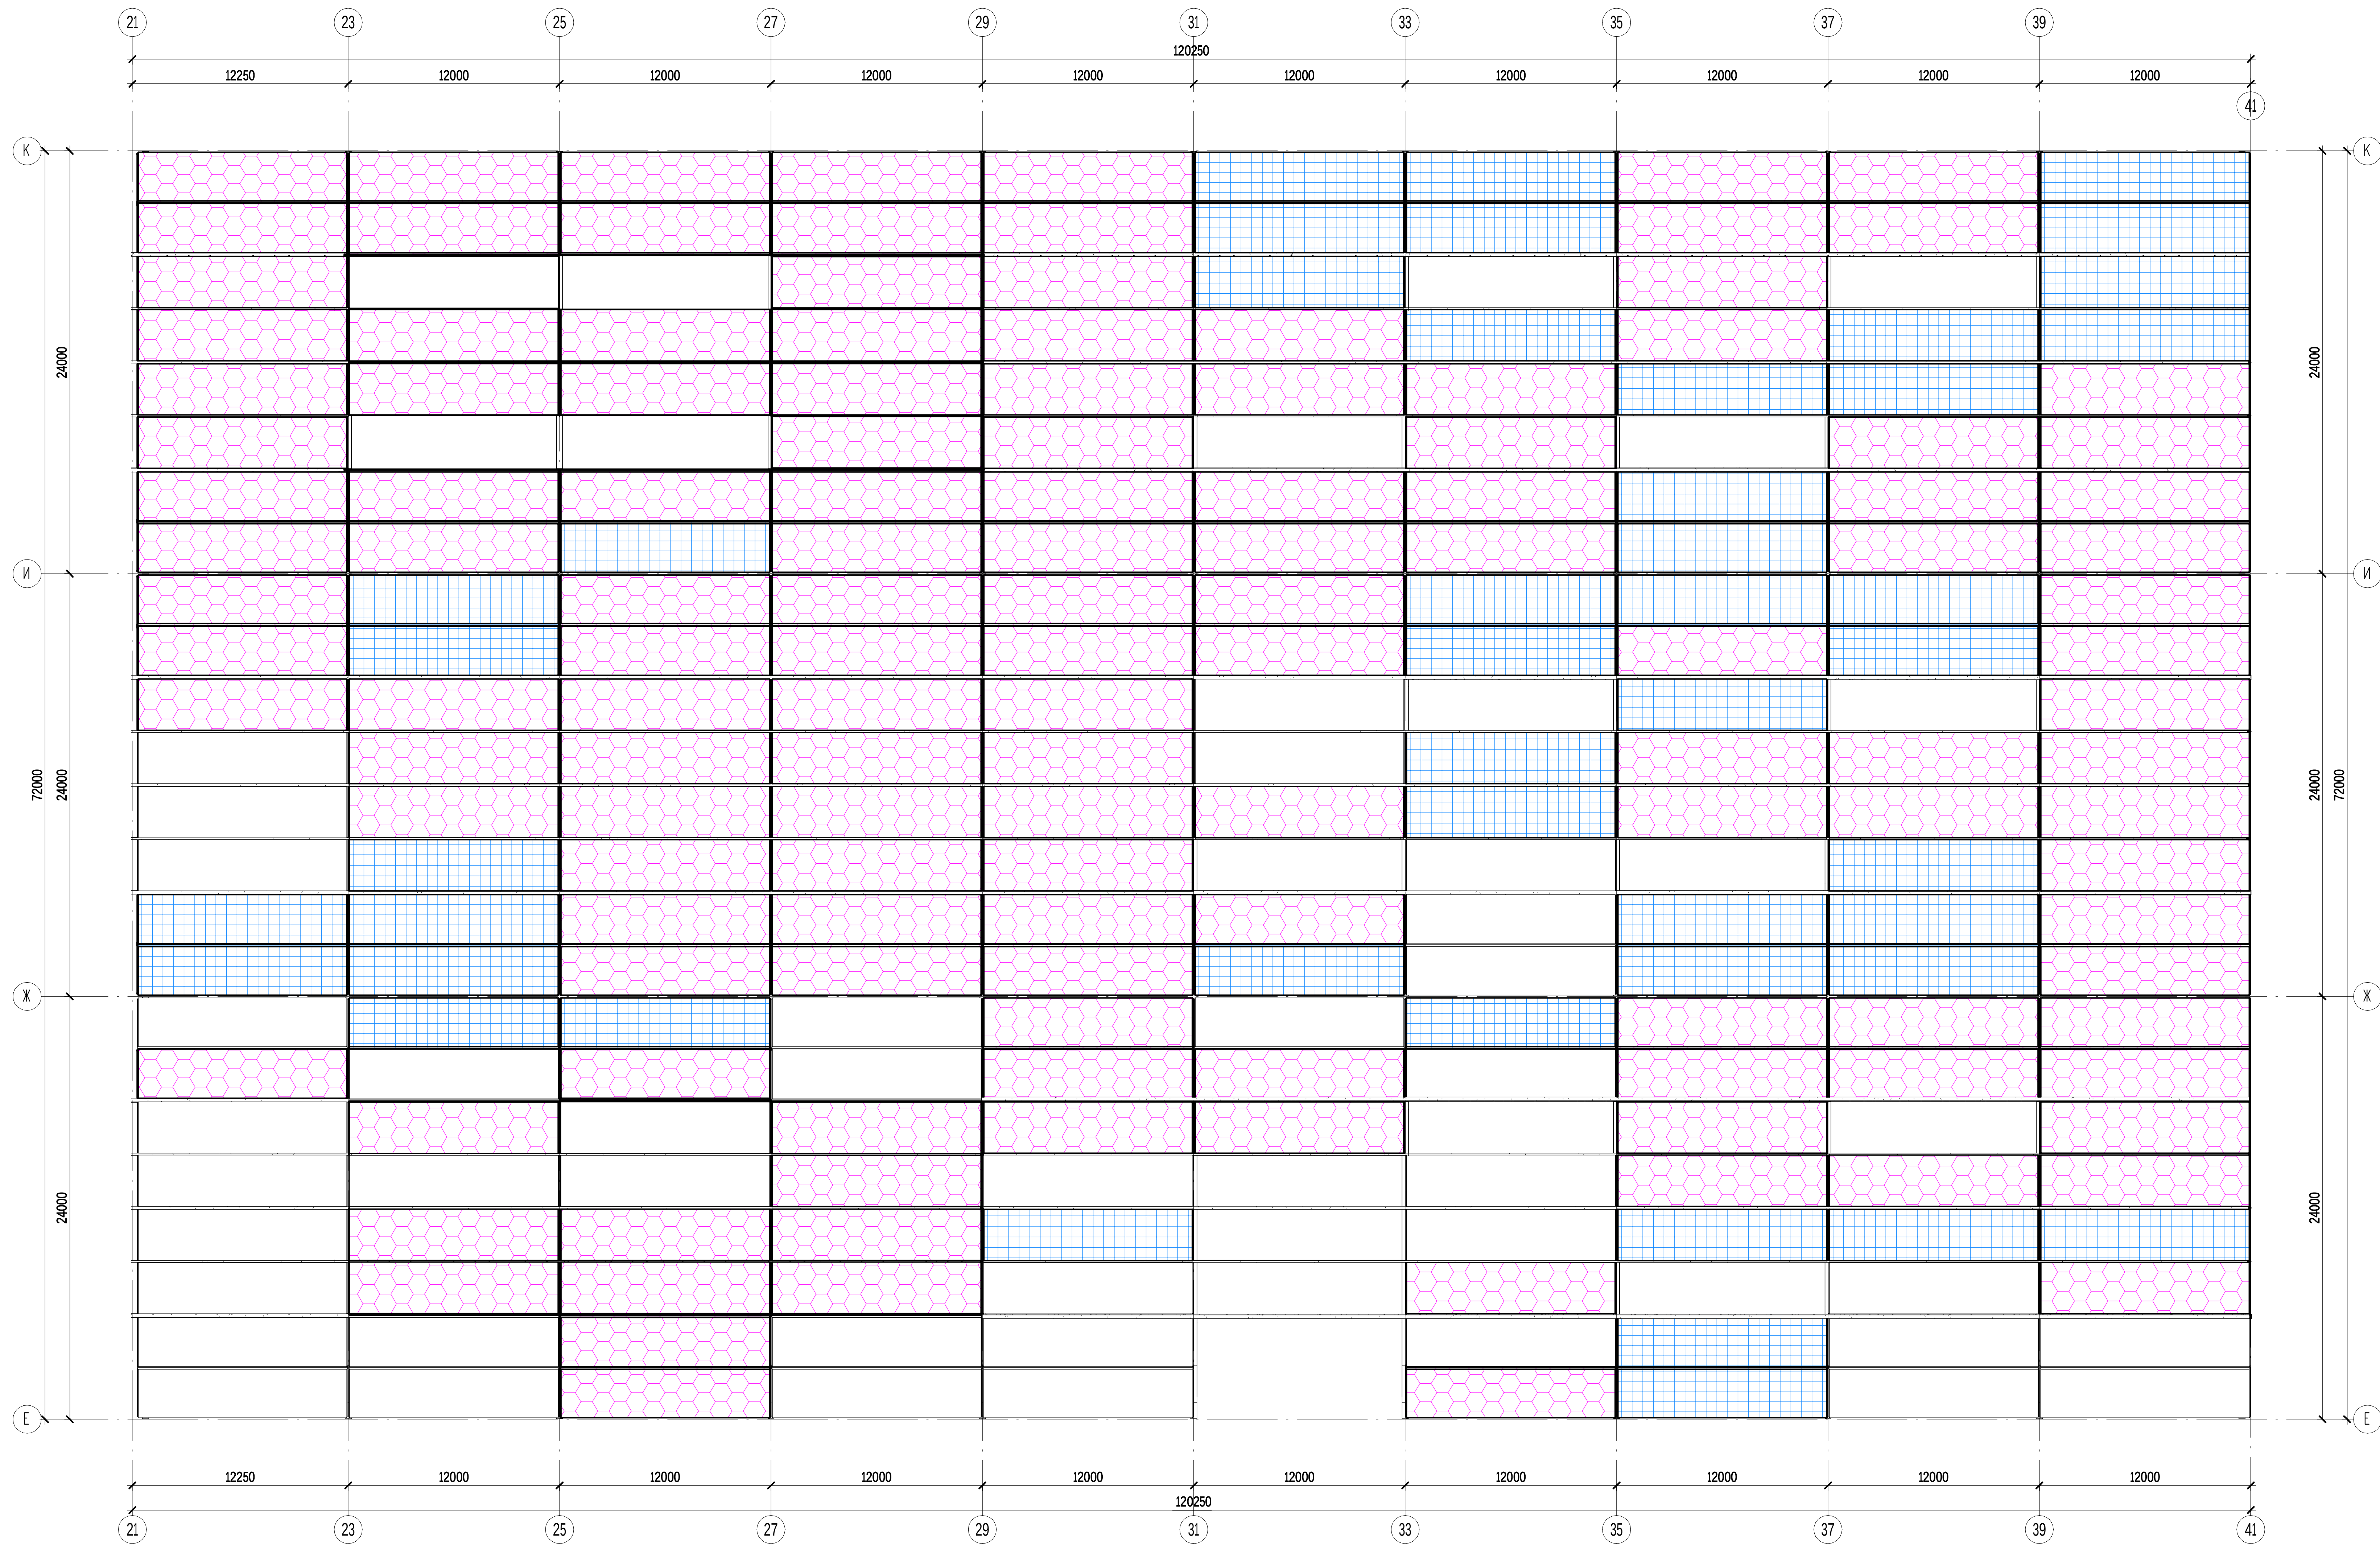


Условные обозначения:

- Восстановление защитного слоя по всей плите
- Восстановление защитного слоя по половине плиты

1. Заделку трещин выполнить по всем плитам покрытия.

						20-08 - АС					
						ООО «Производственное оборудование»					
Изм.	Колуч.	Лист	№ док.	Подпись	Дата	Реконструкция здания цеха комплектации колес, по адресу: г. Липецк, ул. Чехова, 12			Стация	Лист	Листов
Разработал	Белокапитов					Р			16		
Проверил	Батушкин										
Н. Контр.	Захаров					Схема расположения плит покрытия в осях Е-К/21-41 (ремонт)					

АД

 




Спецификация фасадных кассет ФК									
Поз.	Обозначение		Наименование				Кол.	Масса ед., кг	Прим.
ФК-1	Забод "Спальный Фасад"	Фасадные кассеты	1,2	544	1480	RaI6005 / Zn	686		
ФК-2	Забод "Спальный Фасад"	Фасадные кассеты	1,2	544	1480	RaI7004 / Zn	515		
ФК-3	Забод "Спальный Фасад"	Фасадные кассеты	1,2	544	1480	RaI3020 / Zn	153		
ФК-4	Забод "Спальный Фасад"	Фасадные кассеты	1,2	260	1480	RaI7004 / Zn	64		
ФК-5	Забод "Спальный Фасад"	Фасадные кассеты	1,2	342	1480	RaI7004 / Zn	55		
ФК-6	Забод "Спальный Фасад"	Фасадные кассеты	1,2	120	1480	RaI7004 / Zn	55		
ФК-7	Забод "Спальный Фасад"	Фасадные кассеты	1,2	544	980	RaI7004 / Zn	40		
ФК-8	Забод "Спальный Фасад"	Фасадные кассеты	1,2	544	980	RaI6005 / Zn	37		
ФК-9	Забод "Спальный Фасад"	Фасадные кассеты	1,2	544	1780	RaI6005 / Zn	12		
ФК-10	Забод "Спальный Фасад"	Фасадные кассеты	1,2	544	1640	RaI6005 / Zn	12		
ФК-11	Забод "Спальный Фасад"	Фасадные кассеты	1,2	544	2030	RaI7004 / Zn	11		
ФК-12	Забод "Спальный Фасад"	Фасадные кассеты	1,2	544	2030	RaI6005 / Zn	11		
ФК-13	Забод "Спальный Фасад"	Фасадные кассеты	1,2	544	1040	RaI7004 / Zn	11		
ФК-14	Забод "Спальный Фасад"	Фасадные кассеты	1,2	544	1040	RaI6005 / Zn	11		
ФК-15	Забод "Спальный Фасад"	Фасадные кассеты	1,2	544	1780	RaI7004 / Zn	9		
ФК-16	Забод "Спальный Фасад"	Фасадные кассеты	1,2	544	1640	RaI7004 / Zn	9		
ФК-17	Забод "Спальный Фасад"	Фасадные кассеты	1,2	338	1480	RaI6005 / Zn	8		
ФК-18	Забод "Спальный Фасад"	Фасадные кассеты	1,2	544	940	RaI7004 / Zn	4		
ФК-19	Забод "Спальный Фасад"	Фасадные кассеты	1,2	544	2030	RaI3020 / Zn	2		
ФК-20	Забод "Спальный Фасад"	Фасадные кассеты	1,2	544	1780	RaI3020 / Zn	2		
ФК-21	Забод "Спальный Фасад"	Фасадные кассеты	1,2	544	1640	RaI3020 / Zn	2		
ФК-22	Забод "Спальный Фасад"	Фасадные кассеты	1,2	338	1480	RaI7004 / Zn	2		
ФК-23	Забод "Спальный Фасад"	Фасадные кассеты	1,2	544	1040	RaI3020 / Zn	2		
ФК-24	Забод "Спальный Фасад"	Фасадные кассеты	1,2	544	980	RaI3020 / Zn	2		
ФК-25	Забод "Спальный Фасад"	Фасадные кассеты	1,2	260	2980	RaI7004 / Zn	1		
ФК-26	Забод "Спальный Фасад"	Фасадные кассеты	1,2	260	2030	RaI7004 / Zn	1		
ФК-27	Забод "Спальный Фасад"	Фасадные кассеты	1,2	260	1780	RaI7004 / Zn	1		
ФК-28	Забод "Спальный Фасад"	Фасадные кассеты	1,2	260	1640	RaI7004 / Zn	1		
ФК-29	Забод "Спальный Фасад"	Фасадные кассеты	1,2	544	1490	RaI7004 / Zn	1		
ФК-30	Забод "Спальный Фасад"	Фасадные кассеты	1,2	342	1480	RaI6005 / Zn	1		
ФК-31	Забод "Спальный Фасад"	Фасадные кассеты	1,2	120	1480	RaI6005 / Zn	1		
ФК-32	Забод "Спальный Фасад"	Фасадные кассеты	1,2	544	1240	RaI7004 / Zn	1		
ФК-33	Забод "Спальный Фасад"	Фасадные кассеты	1,2	544	1100	RaI7004 / Zn	1		
ФК-34	Забод "Спальный Фасад"	Фасадные кассеты	1,2	260	1040	RaI7004 / Zn	1		
ФК-35	Забод "Спальный Фасад"	Фасадные кассеты	1,2	260	980	RaI7004 / Zn	1		
ФК-36	Забод "Спальный Фасад"	Фасадные кассеты	1,2	544	500	RaI7004 / Zn	1		

Спецификация стеновых сэндвич-панелей ПС									
Поз.	Обозначение		Наименование			Кол.	Масса ед., кг	Прим.	
ПС1	000 "Забайт (Полынонорф)"	Сэндвич-панель	6620	1190	100	Ral7004 / Zn	4		
ПС2	000 "Забайт (Полынонорф)"	Сэндвич-панель	6620	450	100	Ral7004 / Zn	1		
ПС3	000 "Забайт (Полынонорф)"	Сэндвич-панель	6620	1190	100	Ral6006 / Zn	5		
ПС4	000 "Забайт (Полынонорф)"	Сэндвич-панель	6620	1190	100	Ral3020 / Zn	1		
ПС5	000 "Забайт (Полынонорф)"	Сэндвич-панель	6530	1190	100	Ral7004 / Zn	4		
ПС6	000 "Забайт (Полынонорф)"	Сэндвич-панель	6530	450	100	Ral7004 / Zn	1		
ПС7	000 "Забайт (Полынонорф)"	Сэндвич-панель	6530	1190	100	Ral6006 / Zn	5		
ПС8	000 "Забайт (Полынонорф)"	Сэндвич-панель	6530	1190	100	Ral3020 / Zn	1		
ПС9	000 "Забайт (Полынонорф)"	Сэндвич-панель	6270	1190	100	Ral7004 / Zn	4		
ПС10	000 "Забайт (Полынонорф)"	Сэндвич-панель	6270	450	100	Ral7004 / Zn	1		
ПС11	000 "Забайт (Полынонорф)"	Сэндвич-панель	6270	1190	100	Ral6006 / Zn	5		
ПС12	000 "Забайт (Полынонорф)"	Сэндвич-панель	6270	1190	100	Ral3020 / Zn	1		
ПС13	000 "Забайт (Полынонорф)"	Сэндвич-панель	6230	1190	100	Ral7004 / Zn	12		
ПС14	000 "Забайт (Полынонорф)"	Сэндвич-панель	6230	400	100	Ral7004 / Zn	4		
ПС15	000 "Забайт (Полынонорф)"	Сэндвич-панель	6230	1190	100	Ral6006 / Zn	20		
ПС16	000 "Забайт (Полынонорф)"	Сэндвич-панель	6230	1190	100	Ral3020 / Zn	4		
ПС17	000 "Забайт (Полынонорф)"	Сэндвич-панель	6130	1190	100	Ral7004 / Zn	4		
ПС18	000 "Забайт (Полынонорф)"	Сэндвич-панель	6130	450	100	Ral7004 / Zn	1		
ПС19	000 "Забайт (Полынонорф)"	Сэндвич-панель	6130	1190	100	Ral6006 / Zn	5		
ПС20	000 "Забайт (Полынонорф)"	Сэндвич-панель	6130	1190	100	Ral3020 / Zn	1		
ПС21	000 "Забайт (Полынонорф)"	Сэндвич-панель	6030	1190	100	Ral7004 / Zn	12		
ПС22	000 "Забайт (Полынонорф)"	Сэндвич-панель	6030	400	100	Ral7004 / Zn	4		
ПС23	000 "Забайт (Полынонорф)"	Сэндвич-панель	6030	1190	100	Ral6006 / Zn	20		
ПС24	000 "Забайт (Полынонорф)"	Сэндвич-панель	6030	1190	100	Ral3020 / Zn	4		
ПС25	000 "Забайт (Полынонорф)"	Сэндвич-панель	5980	1190	100	Ral7004 / Zn	256		
ПС26	000 "Забайт (Полынонорф)"	Сэндвич-панель	5980	450	100	Ral7004 / Zn	4		
ПС27	000 "Забайт (Полынонорф)"	Сэндвич-панель	5980	400	100	Ral7004 / Zn	72		
ПС28	000 "Забайт (Полынонорф)"	Сэндвич-панель	5980	1190	100	Ral6006 / Zn	412		
ПС29	000 "Забайт (Полынонорф)"	Сэндвич-панель	5980	1190	100	Ral3020 / Zn	84		
ПС30	000 "Забайт (Полынонорф)"	Сэндвич-панель	5970	1190	100	Ral7004 / Zn	15		
ПС31	000 "Забайт (Полынонорф)"	Сэндвич-панель	5970	400	100	Ral7004 / Zn	2		
ПС32	000 "Забайт (Полынонорф)"	Сэндвич-панель	5970	1190	100	Ral3020 / Zn	2		
ПС33	000 "Забайт (Полынонорф)"	Сэндвич-панель	2420	1190	100	Ral7004 / Zn	2		
ПС34	000 "Забайт (Полынонорф)"	Сэндвич-панель	1920	1190	100	Ral7004 / Zn	2		
ПС35	000 "Забайт (Полынонорф)"	Сэндвич-панель	1590	1190	100	Ral7004 / Zn	1		
ПС36	000 "Забайт (Полынонорф)"	Сэндвич-панель	1500	1190	100	Ral7004 / Zn	1		
ПС37	000 "Забайт (Полынонорф)"	Сэндвич-панель	1240	1190	100	Ral7004 / Zn	1		
ПС38	000 "Забайт (Полынонорф)"	Сэндвич-панель	1100	1190	100	Ral7004 / Zn	1		
ПС39	000 "Забайт (Полынонорф)"	Сэндвич-панель	1000	1190	100	Ral7004 / Zn	4		
ПС40	000 "Забайт (Полынонорф)"	Сэндвич-панель	990	1190	100	Ral7004 / Zn	19		
ПС41	000 "Забайт (Полынонорф)"	Сэндвич-панель	990	1190	100	Ral6006 / Zn	32		
ПС42	000 "Забайт (Полынонорф)"	Сэндвич-панель	980	1190	100	Ral7004 / Zn	3		

Поз.	Обозначение	Наименование	Кол.	Масса ед., кг	Прим.
ПФ1	010 "Забол (Полнотерм)"	Сэндвич-профиль 6560 600 100	Ral9003 / Макс. тепло 2000с/ч3	23	
ПФ2	010 "Забол (Полнотерм)"	Сэндвич-профиль 6560 600 100	Ral9003 / Макс. тепло 2000с/ч3	23	
ПФ3	010 "Забол (Полнотерм)"	Сэндвич-профиль 6300 600 100	Ral9003 / Макс. тепло 2000с/ч3	22	
ПФ4	010 "Забол (Полнотерм)"	Сэндвич-профиль 6160 600 100	Ral9003 / Макс. тепло 2000с/ч3	22	
ПФ5	010 "Забол (Полнотерм)"	Сэндвич-профиль 6007 600 100	Ral9003 / Макс. тепло 2000с/ч3	46	
ПФ6	010 "Забол (Полнотерм)"	Сэндвич-профиль 6000 600 100	Ral9003 / Макс. тепло 2000с/ч3	215	
ПФ7	010 "Забол (Полнотерм)"	Сэндвич-профиль 6000 490 100	Ral9003 / Макс. тепло 2000с/ч3	7	
ПФ8	010 "Забол (Полнотерм)"	Сэндвич-профиль 6000 120 100	Ral9003 / Макс. тепло 2000с/ч3	7	
ПФ10	010 "Забол (Полнотерм)"	Сэндвич-профиль 5985 600 100	Ral9003 / Макс. тепло 2000с/ч3	22	
ПФ11	010 "Забол (Полнотерм)"	Сэндвич-профиль 5985 490 100	Ral9003 / Макс. тепло 2000с/ч3	1	
ПФ12	010 "Забол (Полнотерм)"	Сэндвич-профиль 5985 120 100	Ral9003 / Макс. тепло 2000с/ч3	1	
ПФ13	010 "Забол (Полнотерм)"	Сэндвич-профиль 1520 600 100	Ral9003 / Макс. тепло 2000с/ч3	1	
ПФ14	010 "Забол (Полнотерм)"	Сэндвич-профиль 1510 600 100	Ral9003 / Макс. тепло 2000с/ч3	1	
ПФ15	010 "Забол (Полнотерм)"	Сэндвич-профиль 1260 600 100	Ral9003 / Макс. тепло 2000с/ч3	1	
ПФ16	010 "Забол (Полнотерм)"	Сэндвич-профиль 1120 600 100	Ral9003 / Макс. тепло 2000с/ч3	1	
ПФ17	010 "Забол (Полнотерм)"	Сэндвич-профиль 1000 600 100	Ral9003 / Макс. тепло 2000с/ч3	50	
ПФ19	010 "Забол (Полнотерм)"	Сэндвич-профиль 967 600 100	Ral9003 / Макс. тепло 2000с/ч3	1	
ПФ20	010 "Забол (Полнотерм)"	Сэндвич-профиль 960 600 100	Ral9003 / Макс. тепло 2000с/ч3	2	
ПФ21	010 "Забол (Полнотерм)"	Сэндвич-профиль 953 600 100	Ral9003 / Макс. тепло 2000с/ч3	1	



Ведомость заполнения окнами и дверей проемов					
Марка	Обозначение	Наименование	Число	Масса, ед. кол.	Примечание
В-1	ТУ Р5 10452725.002-2000	Секционные ворота серии ProPlus 4000x4200(л)	19		
ДВ-1	ГОСТ 31173-2003	ДВН (ПН 2100-900 900x2100(л))	3		
ОК-1	ГОСТ 23166-99	ОП ОКП 15-13 /5040x1190(л)	32		
ОК-2	ГОСТ 23166-99	ОП ОКП 15-13 /3000x1190(л)	192		

Спецификация полов					
Номер помещения	Тип пола	Изображение типоразмера	Данные элементов пола, мм - Плита х/б бетона 825 с армированием 10/9 АКВ - 1300/55 13 2296-00-08611770-2016 с защитным покрытием EscorTech Fingmate (Плиты 50 мм, диаметр 1 мм) из чистого 6 кг на 1м3 с покрытием утроитель EscorTond / расход 3,5 кг на 1м2, E250 мм - мембрана PLANTER от ТехноНИКОЛЬ	Площадь	Примечание
12,3,4	1			26247 м²	

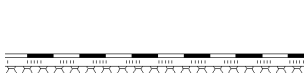Спецификация на кровлю				
Тип кровли	Изображение	Состав	Площадь	Примечание
1		-полимерная мембрана LOGICROOF V-GF FB -клеевой состав LOGICROOF Spray Клей контактный -дренажный слой - PR-SLOPE-50mm -клеевой состав LOGICROOF Spray Клей-пена -плиты пенополиизоционные PR-50mm -клеевой состав LOGICROOF Spray Клей-пена -плиты пенополиизоционные PR-50mm -клеевой состав LOGICROOF Spray Клей-пена -унифлекс Г -профилер Ватный ТехноНИКОЛЬ №P01 -стальной железобетон	26993 м²	


Изд. № подл.	Подп. и дата	Взам. инд. №	Согласовано	

Спецификация угловых фасадных кассет ФКУ									
Поз.	Обозначение	Наименование					Кол.	Масса ед., кг	Прим.
ФКУ-1	Забой "Стальной Фасад"	Фасадные кассеты					40		
ФКУ-1	Забой "Стальной Фасад"	Фасадные кассеты					2		
ФКУ-2	Забой "Стальной Фасад"	Фасадные кассеты					4		

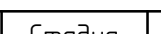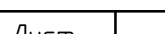
					20-08 - АС		
					ООО «Производственное оборудование»		
Изм. Контр.		Лист	№ док.	Подпись	Дата		
Разработал Проверил		Белокотиков Батумкин				Реконструкция здания цеха комплектации колес, по адресу: г. Липецк, ул. Чехова,12	Страница
							Лист
							Листов
Н. Контр.		Захаров				Спецификации и ведомости	 

Согласовано			
Инд. № подл.	Взам. инд. №	Подп. и дата	


Стык сэндвич-панелей по колонне

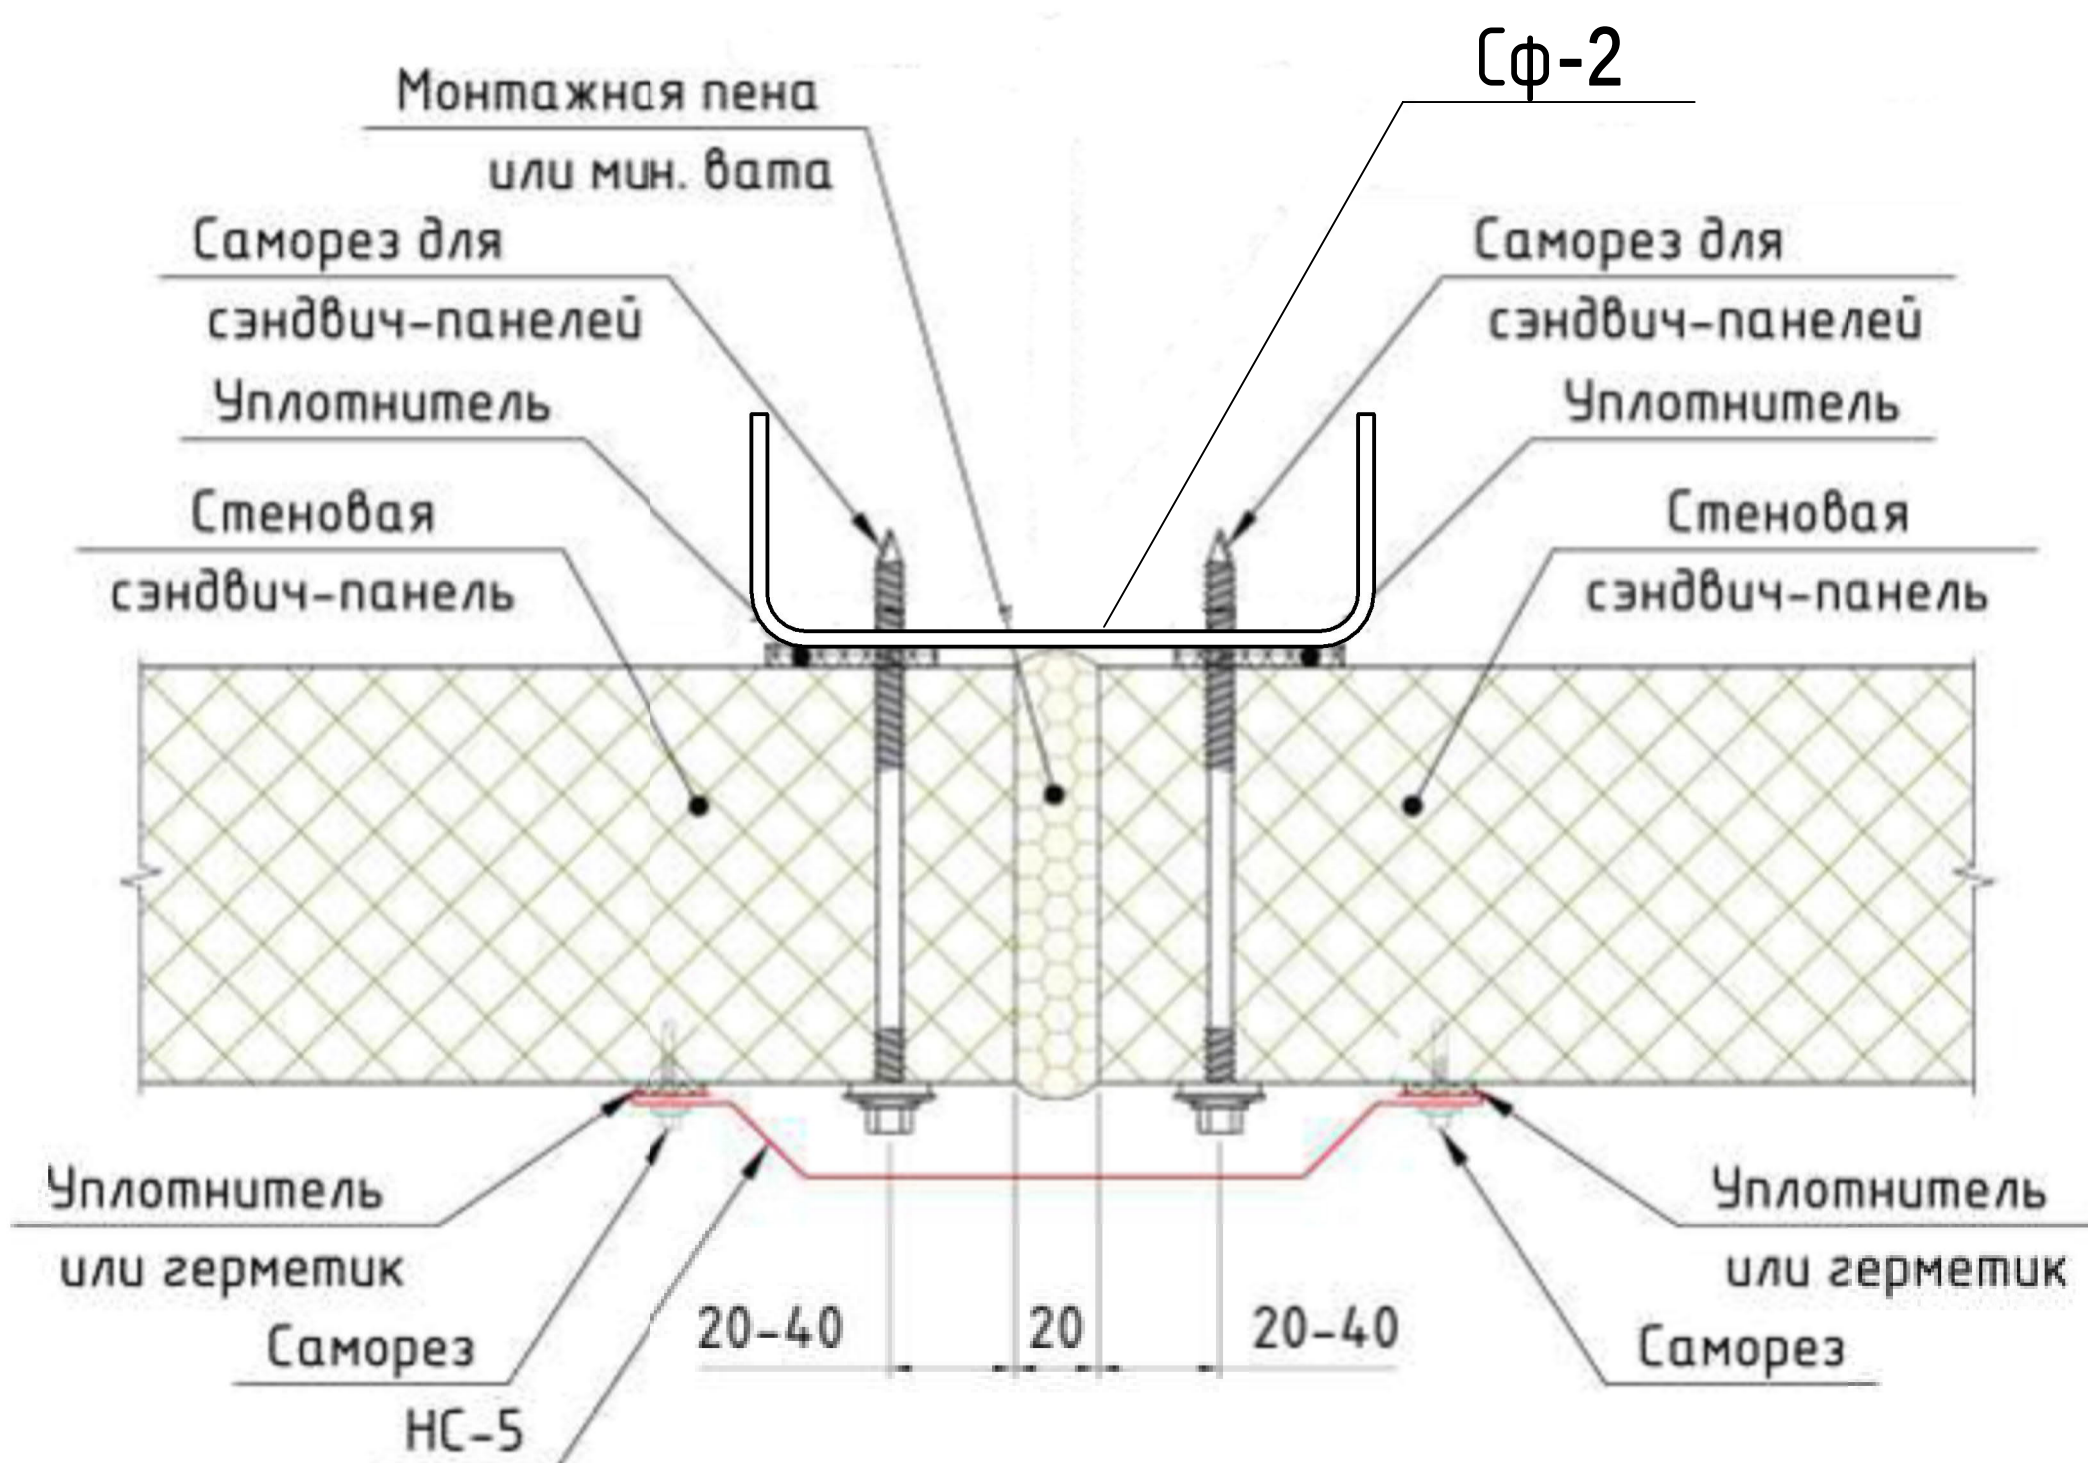



Примыкание сэндвич-панели к цоколю

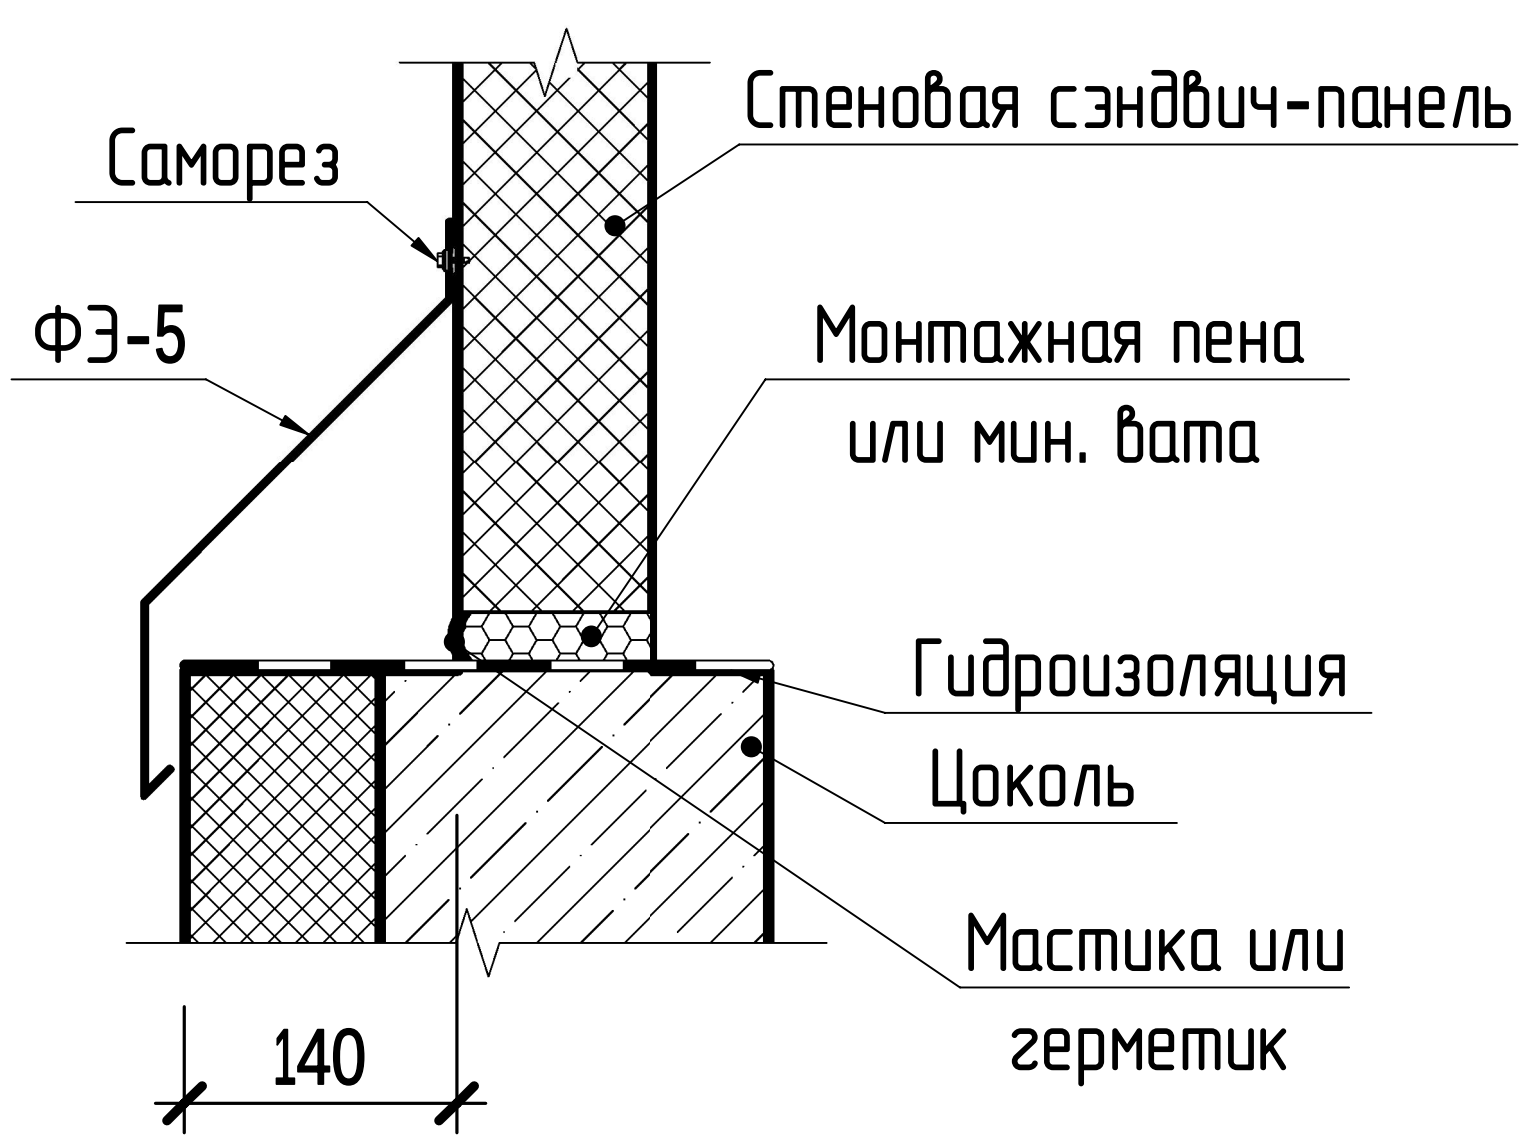



Стык сэндвич-панелей по внешнему углу

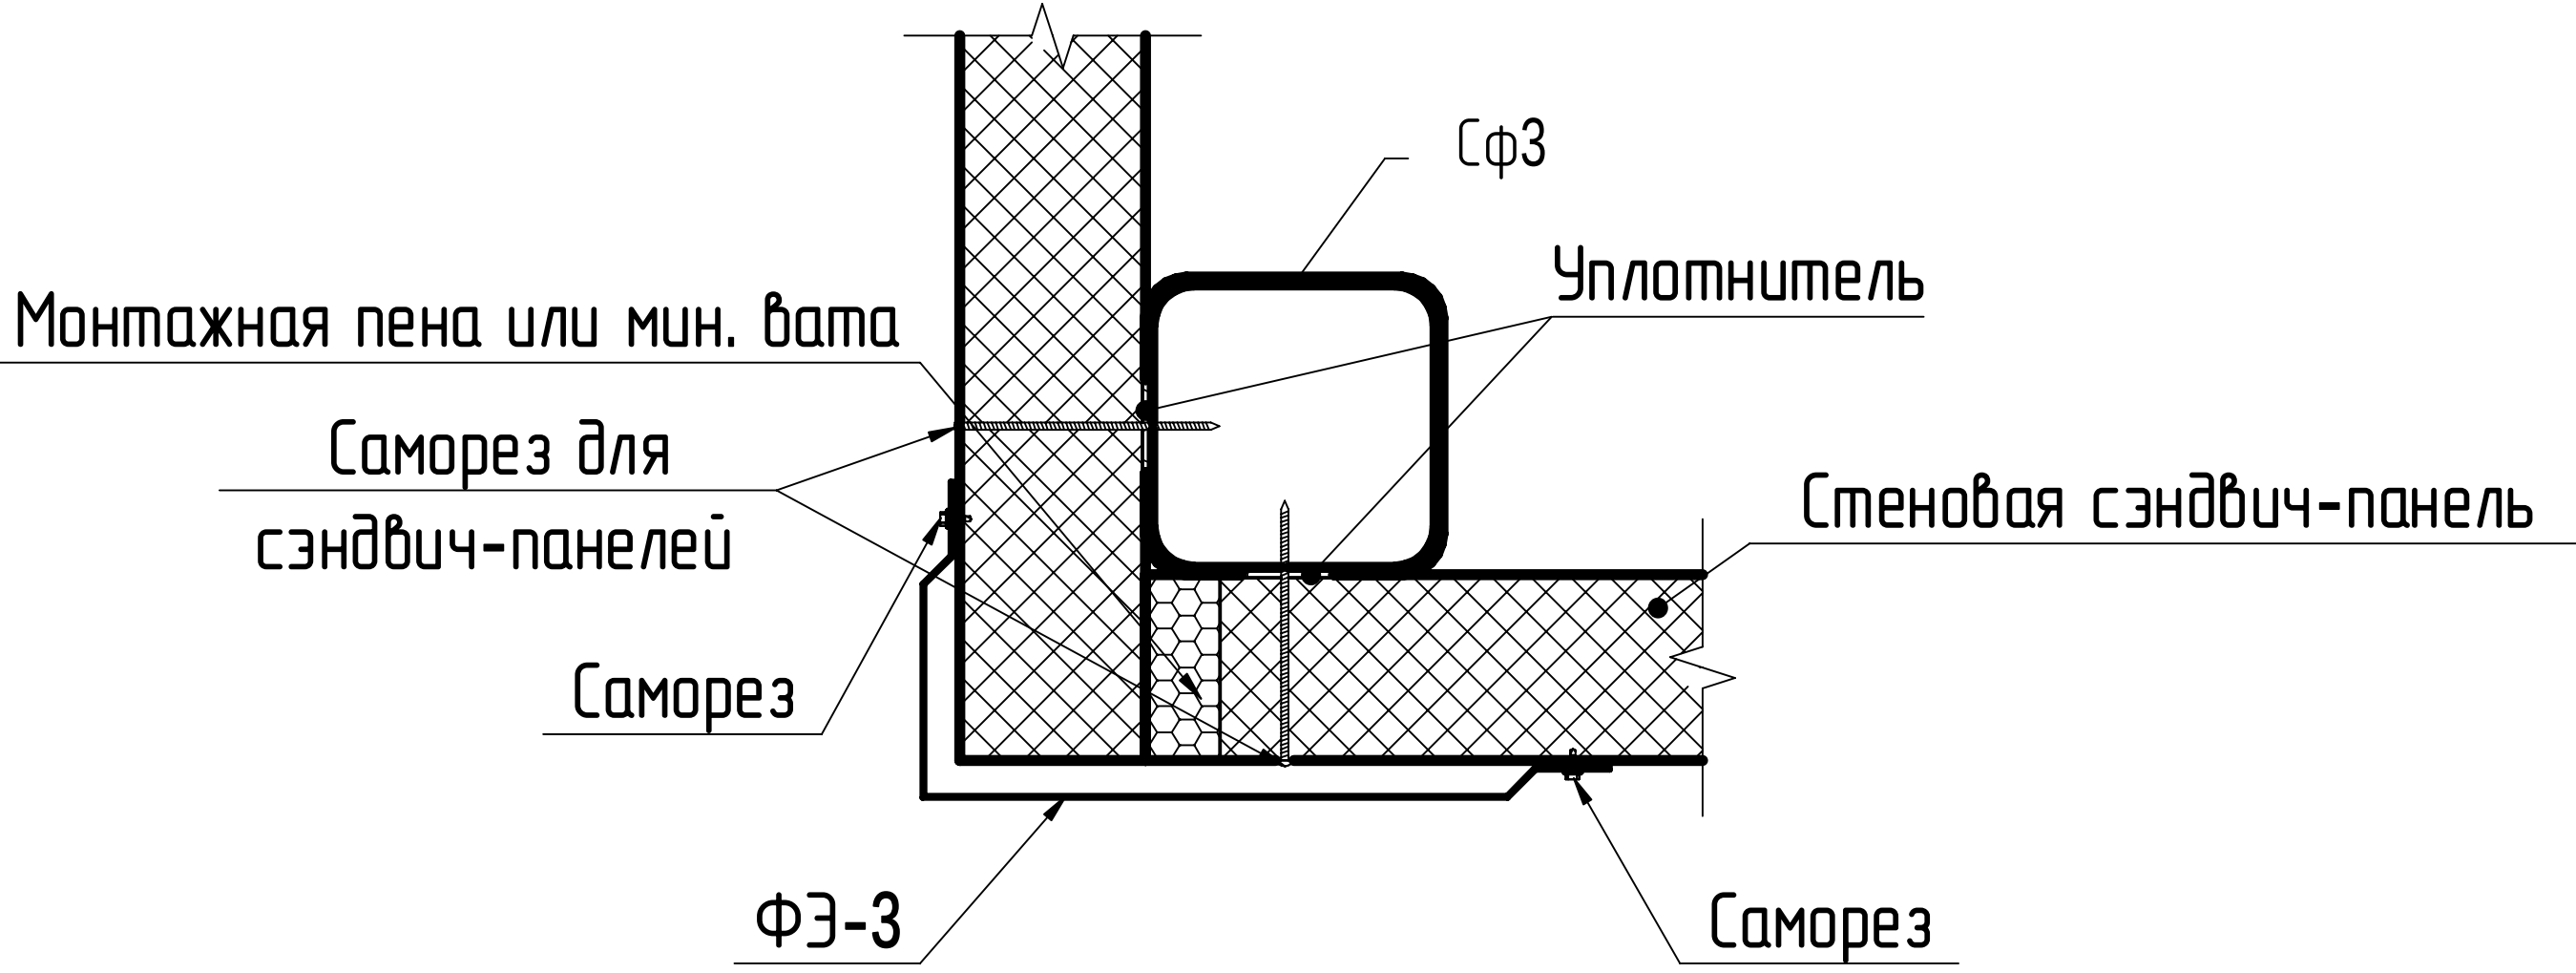

Обрамление секционных (подъемных) ворот

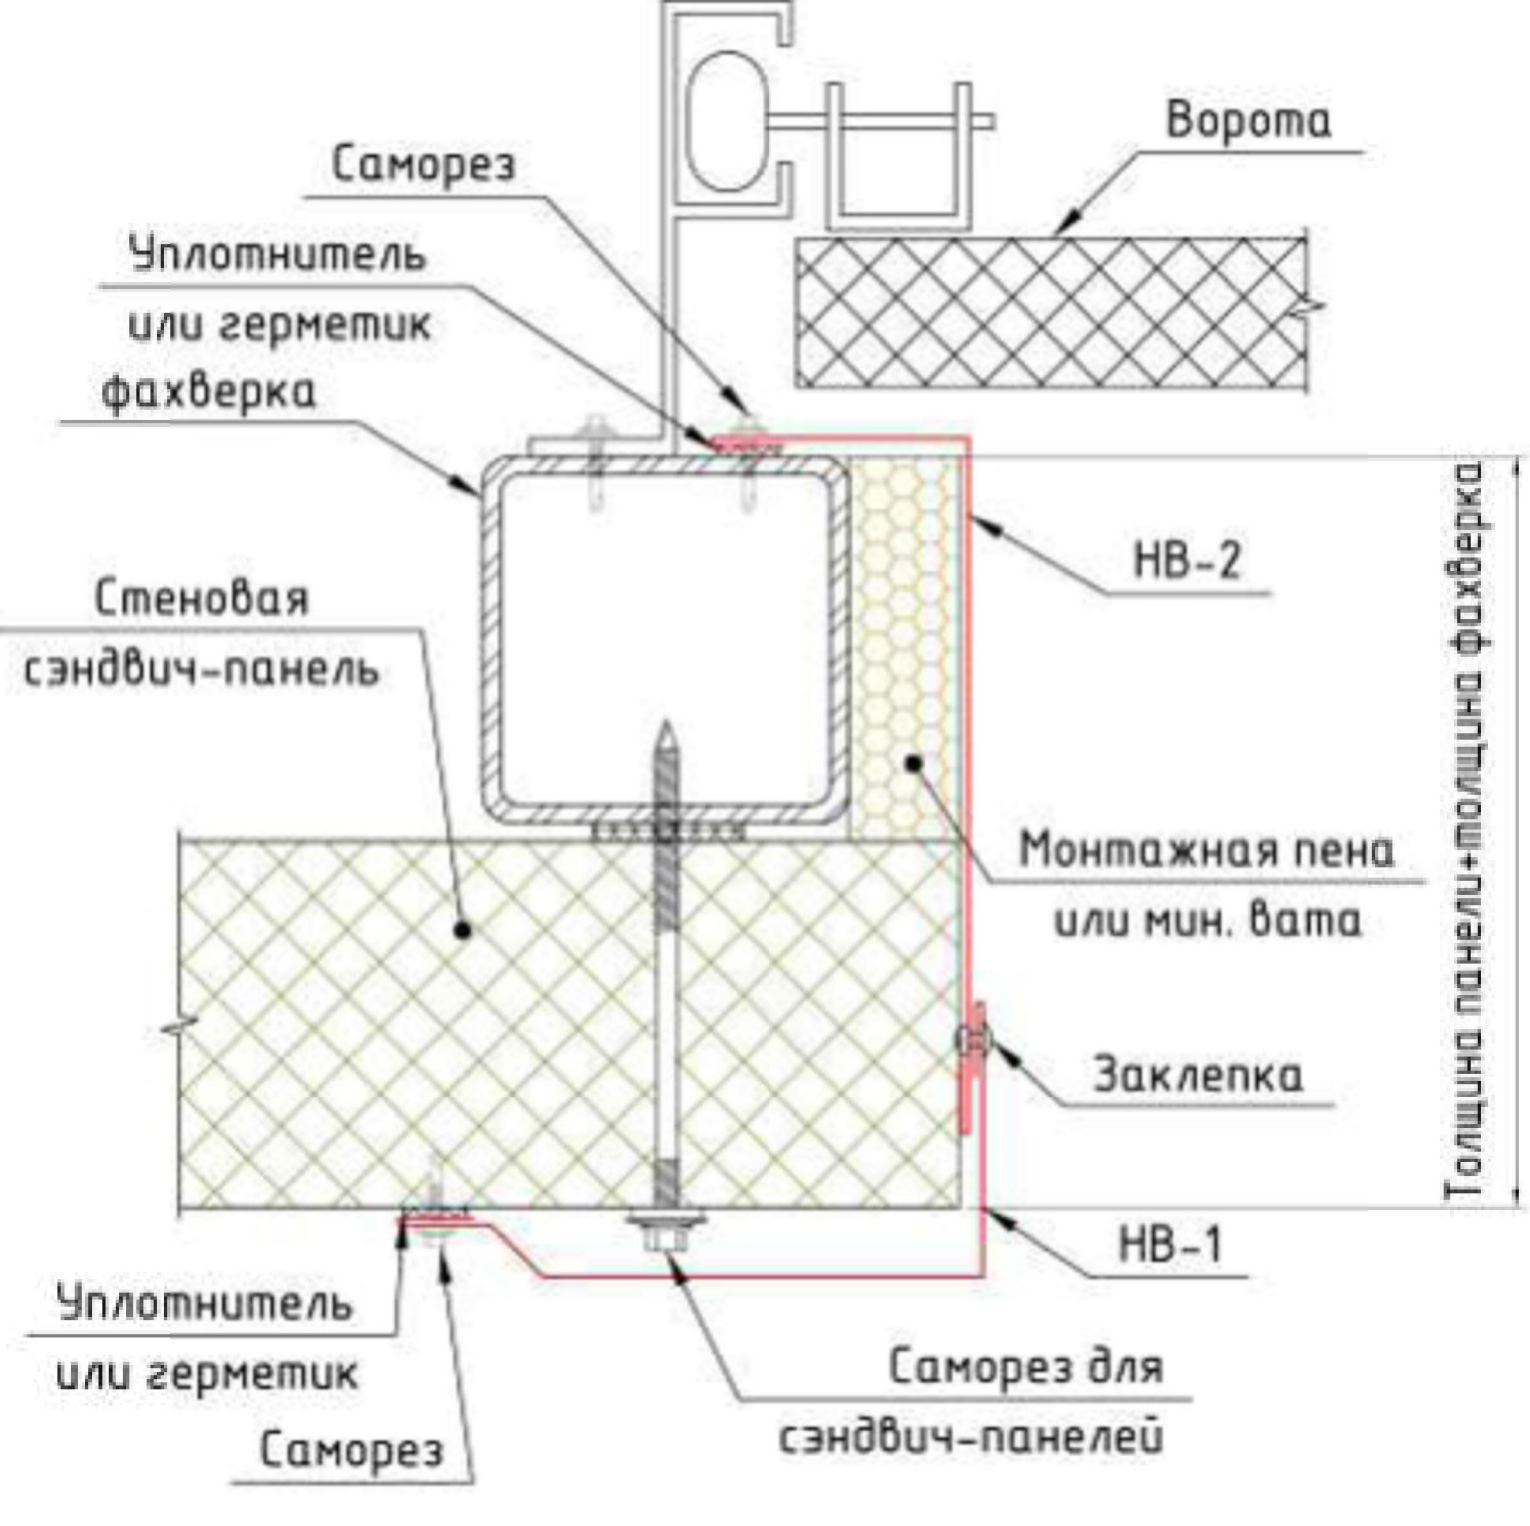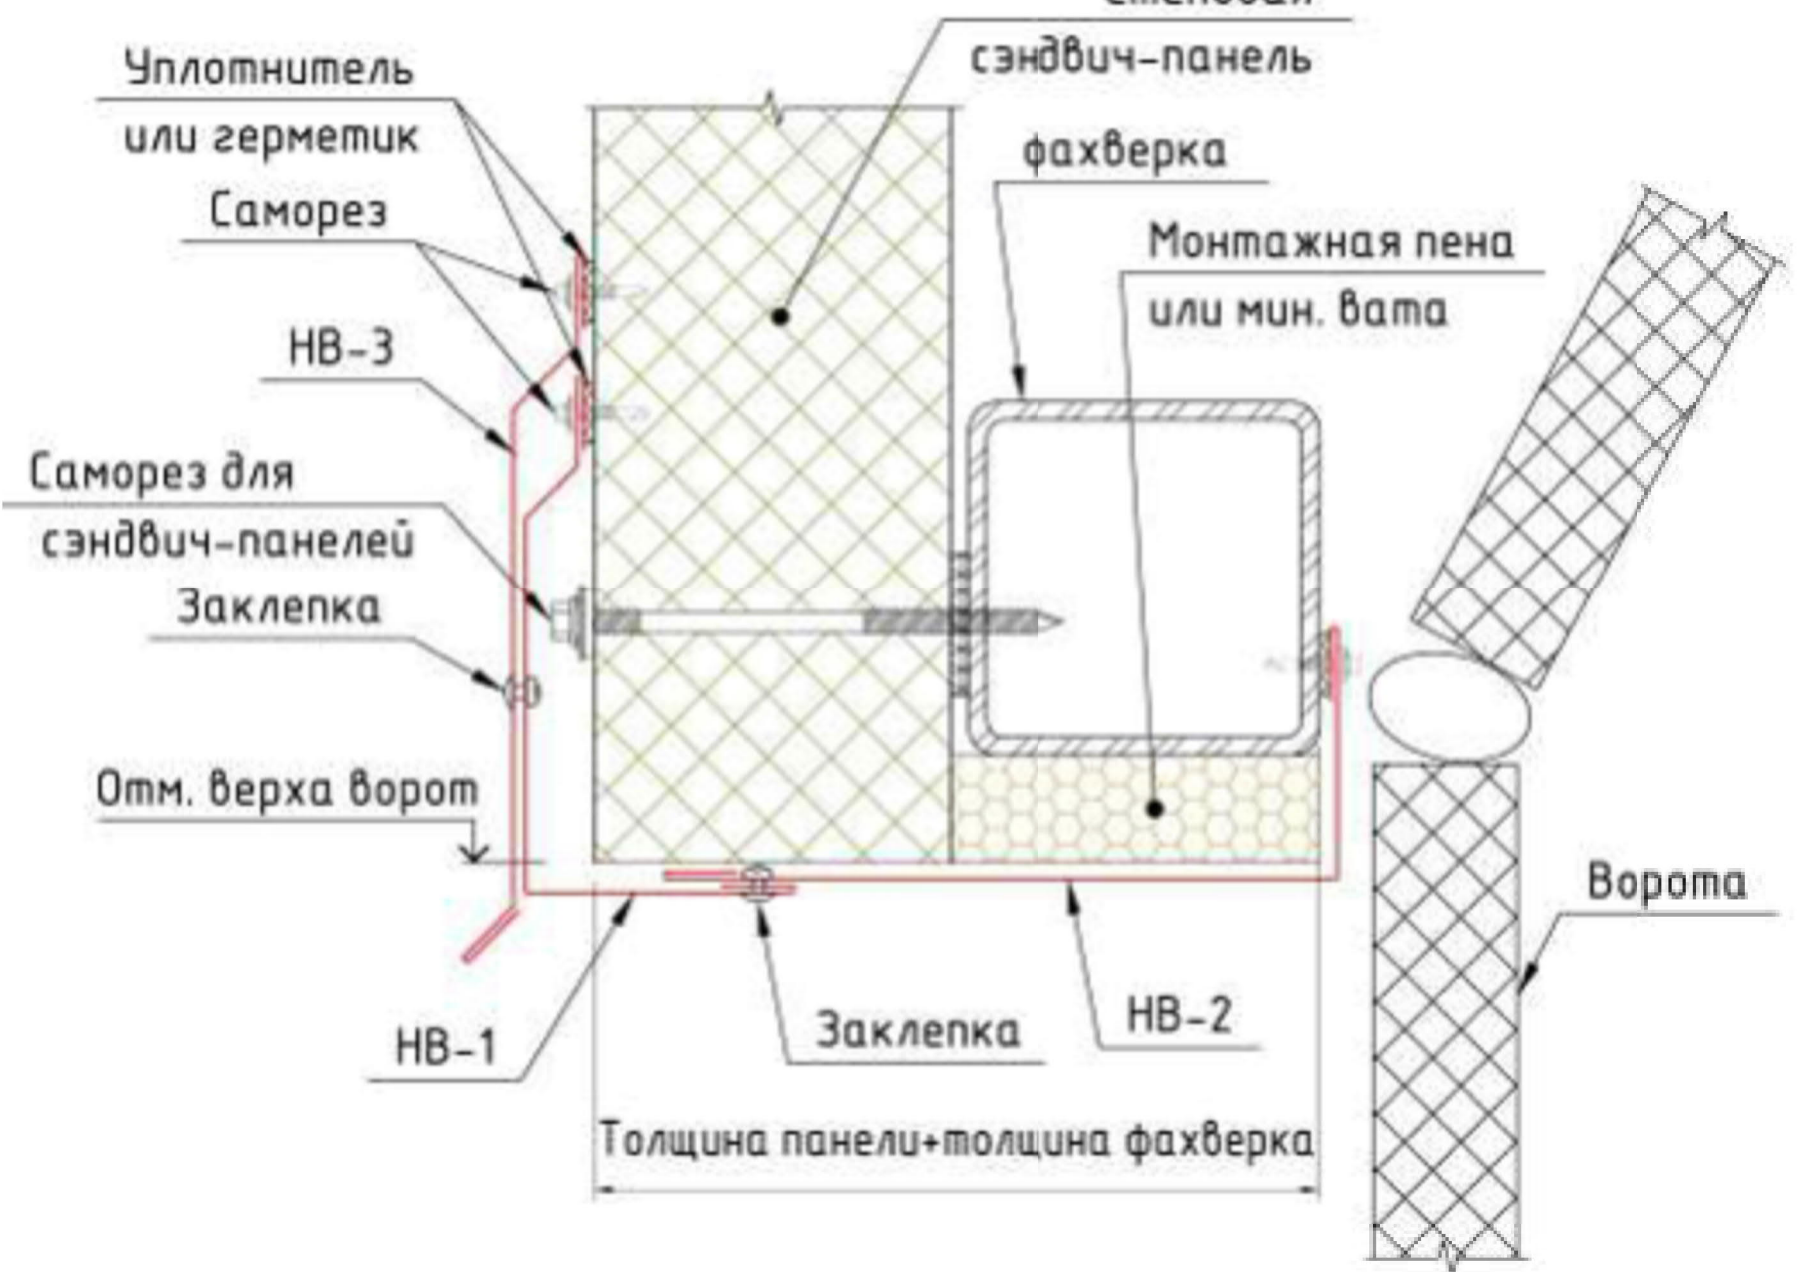

Обрамление оконных блоков из ПВХ

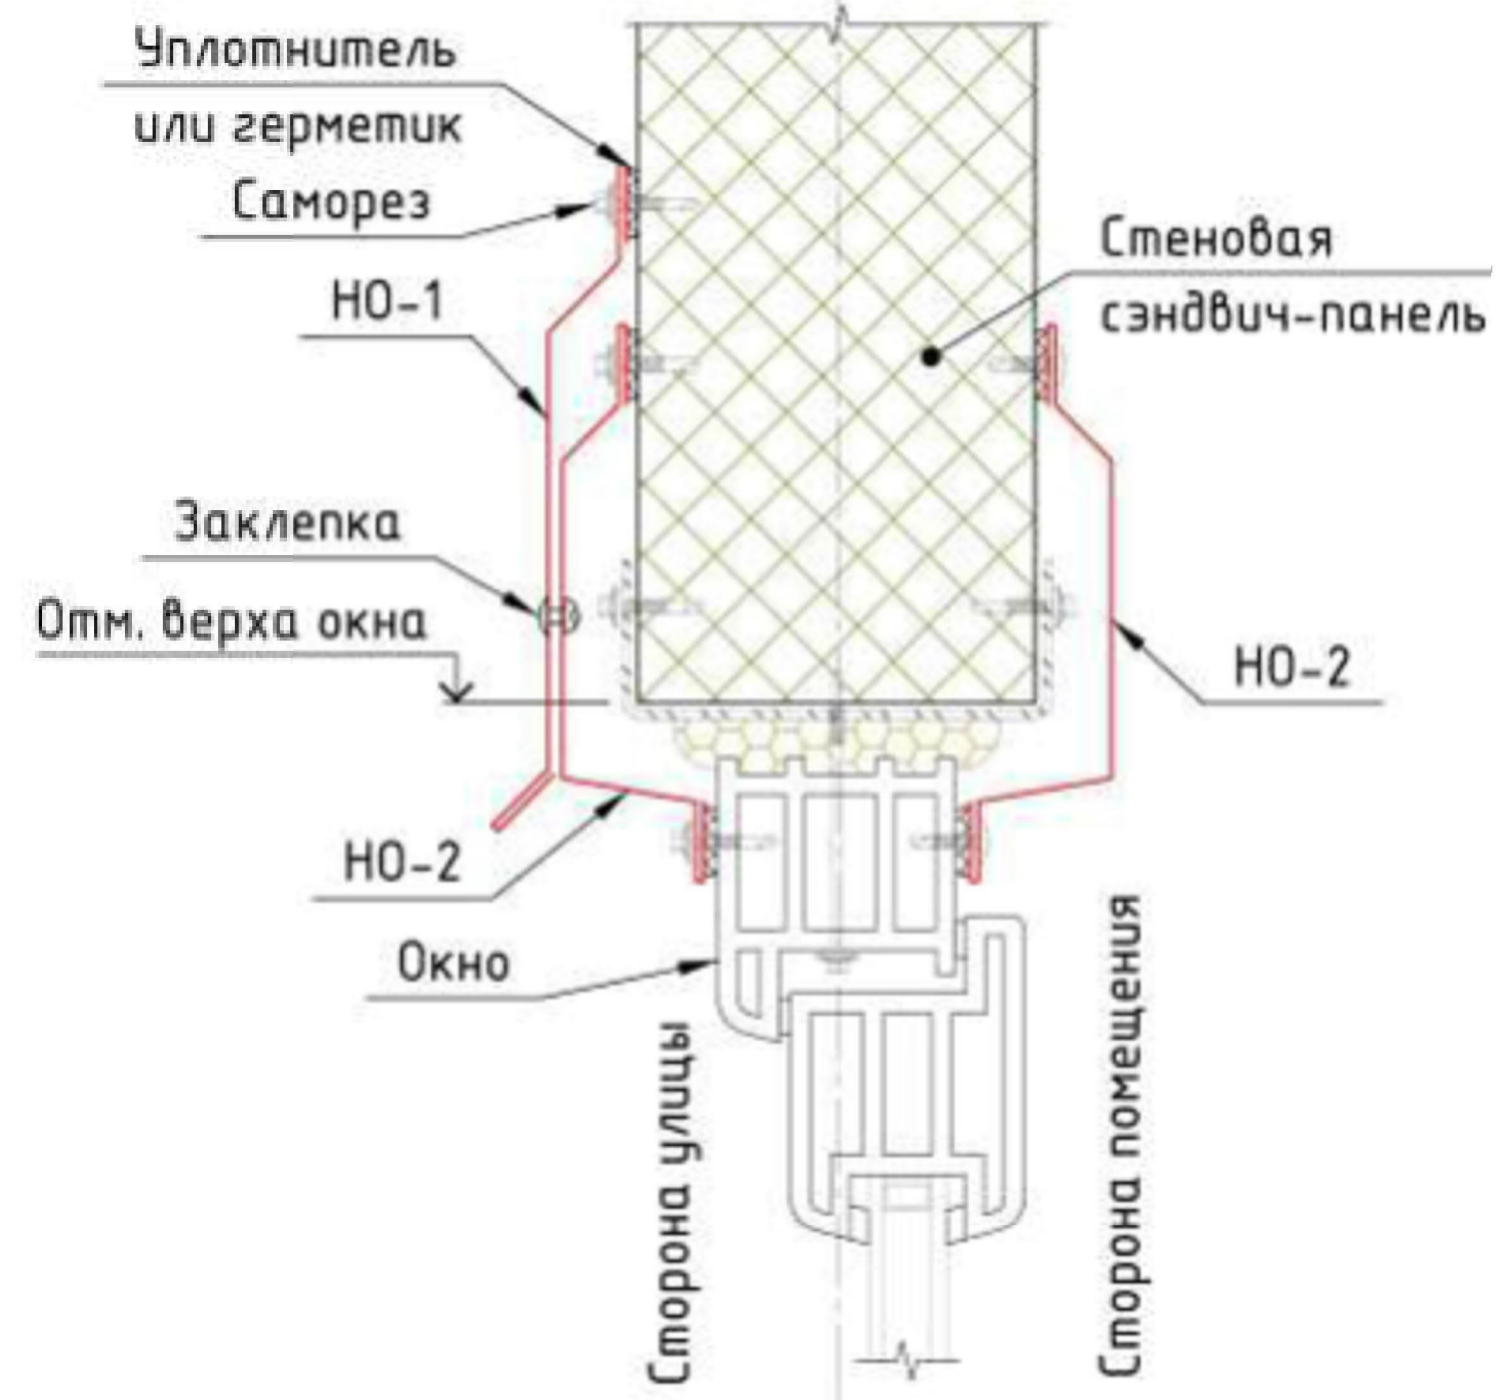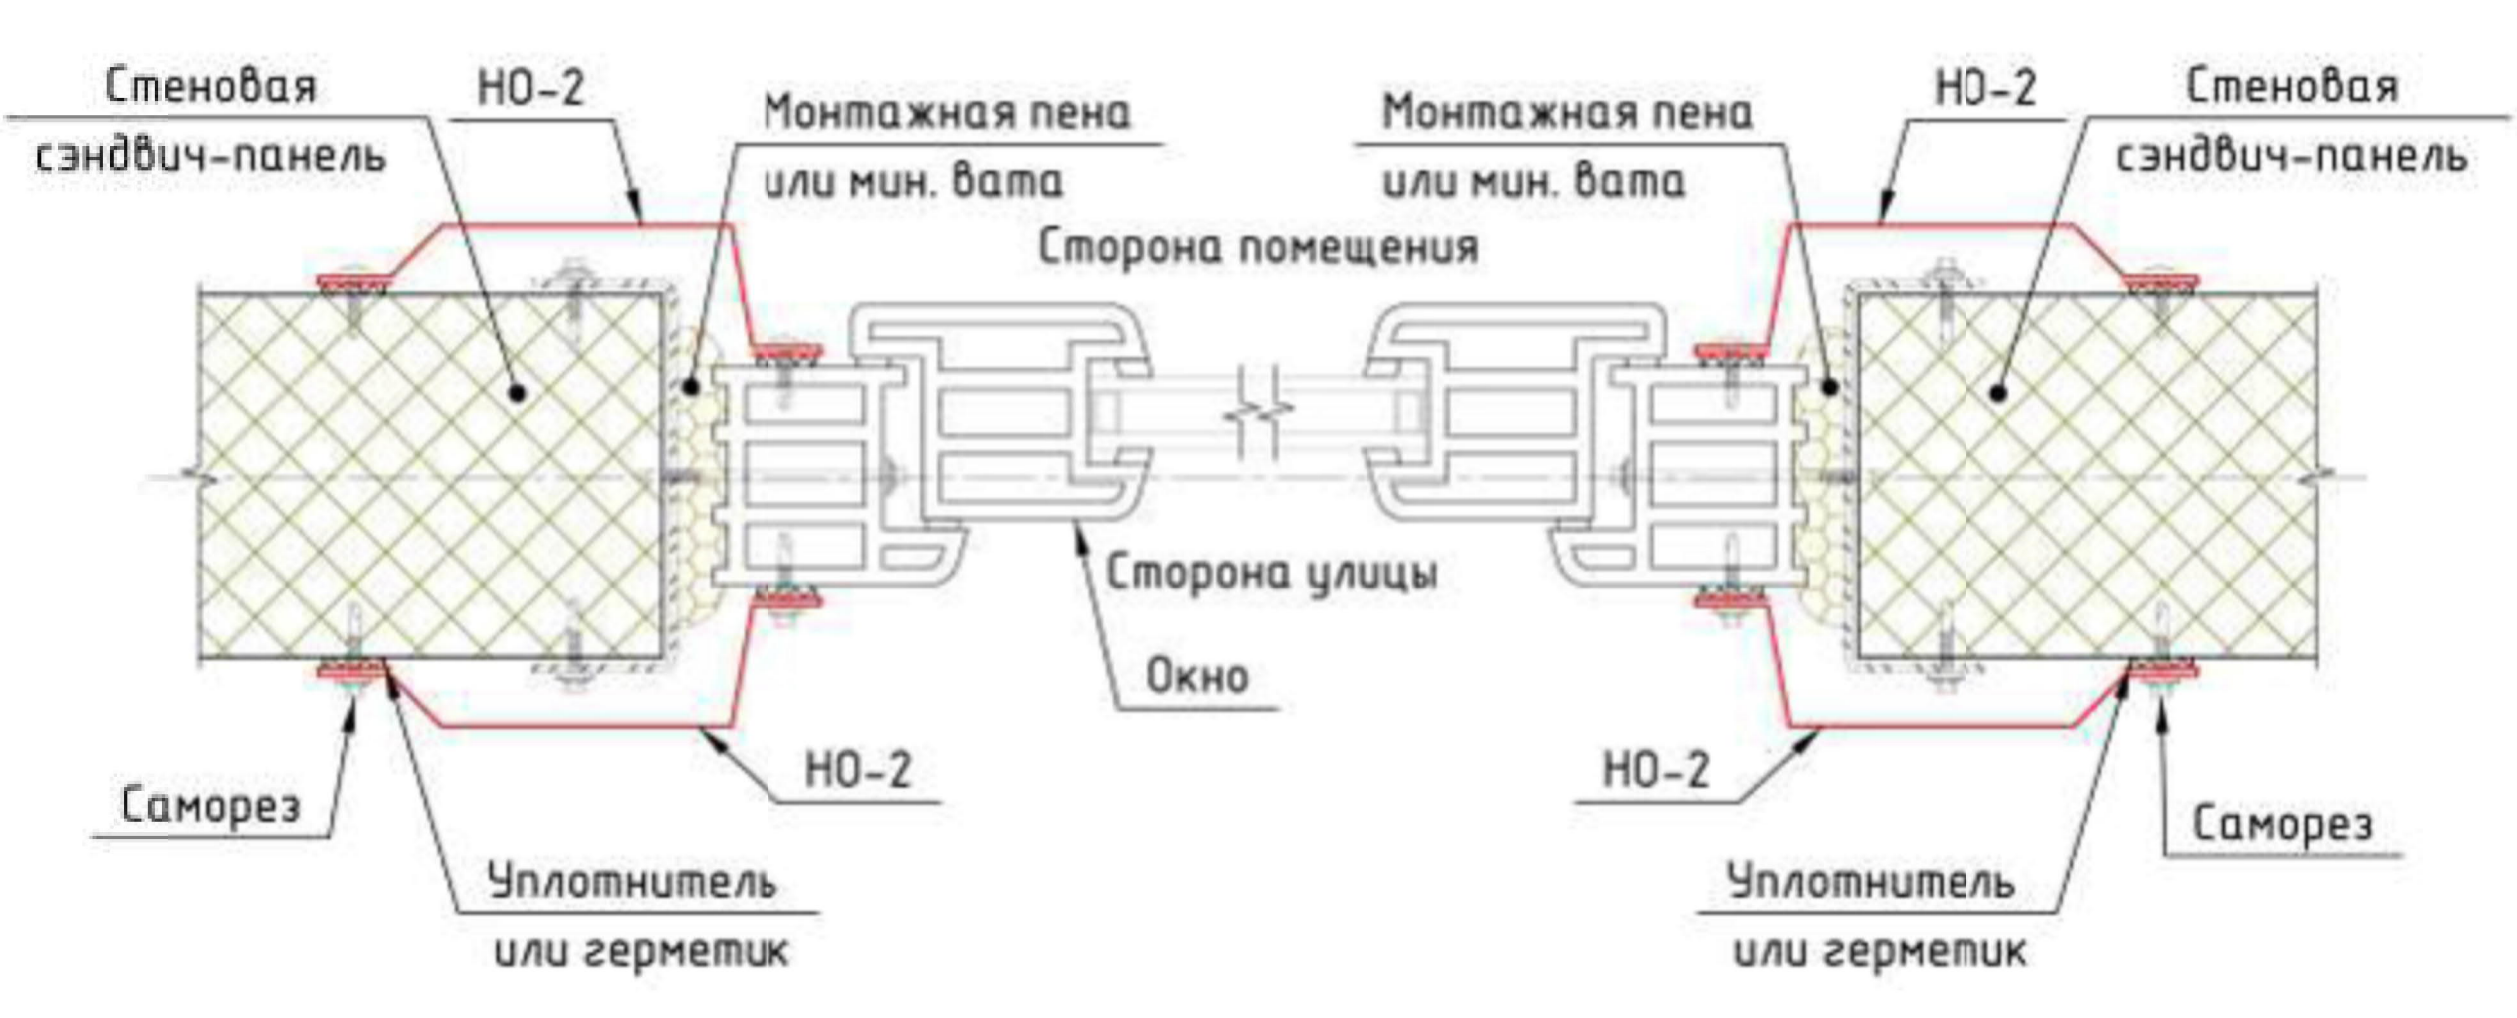

						20-08 - АС		
						ООО «Производственное оборудование»		
Изм.	Колуч.	Лист	№ док.	Подпись	Дата	Реконструкция здания цеха комплектации колес, по адресу: г. Липецк, ул. Чехова,12	Стадия	Лист
Разработал	Белокопытов						р	20
Проверил	Батухтин					Узлы крепления сэндвич-панелей	ТЕХ ИНВЕСТ ПРОЕКТ	
Н. Контр.	Захаров							