


5 ЭТАЖ

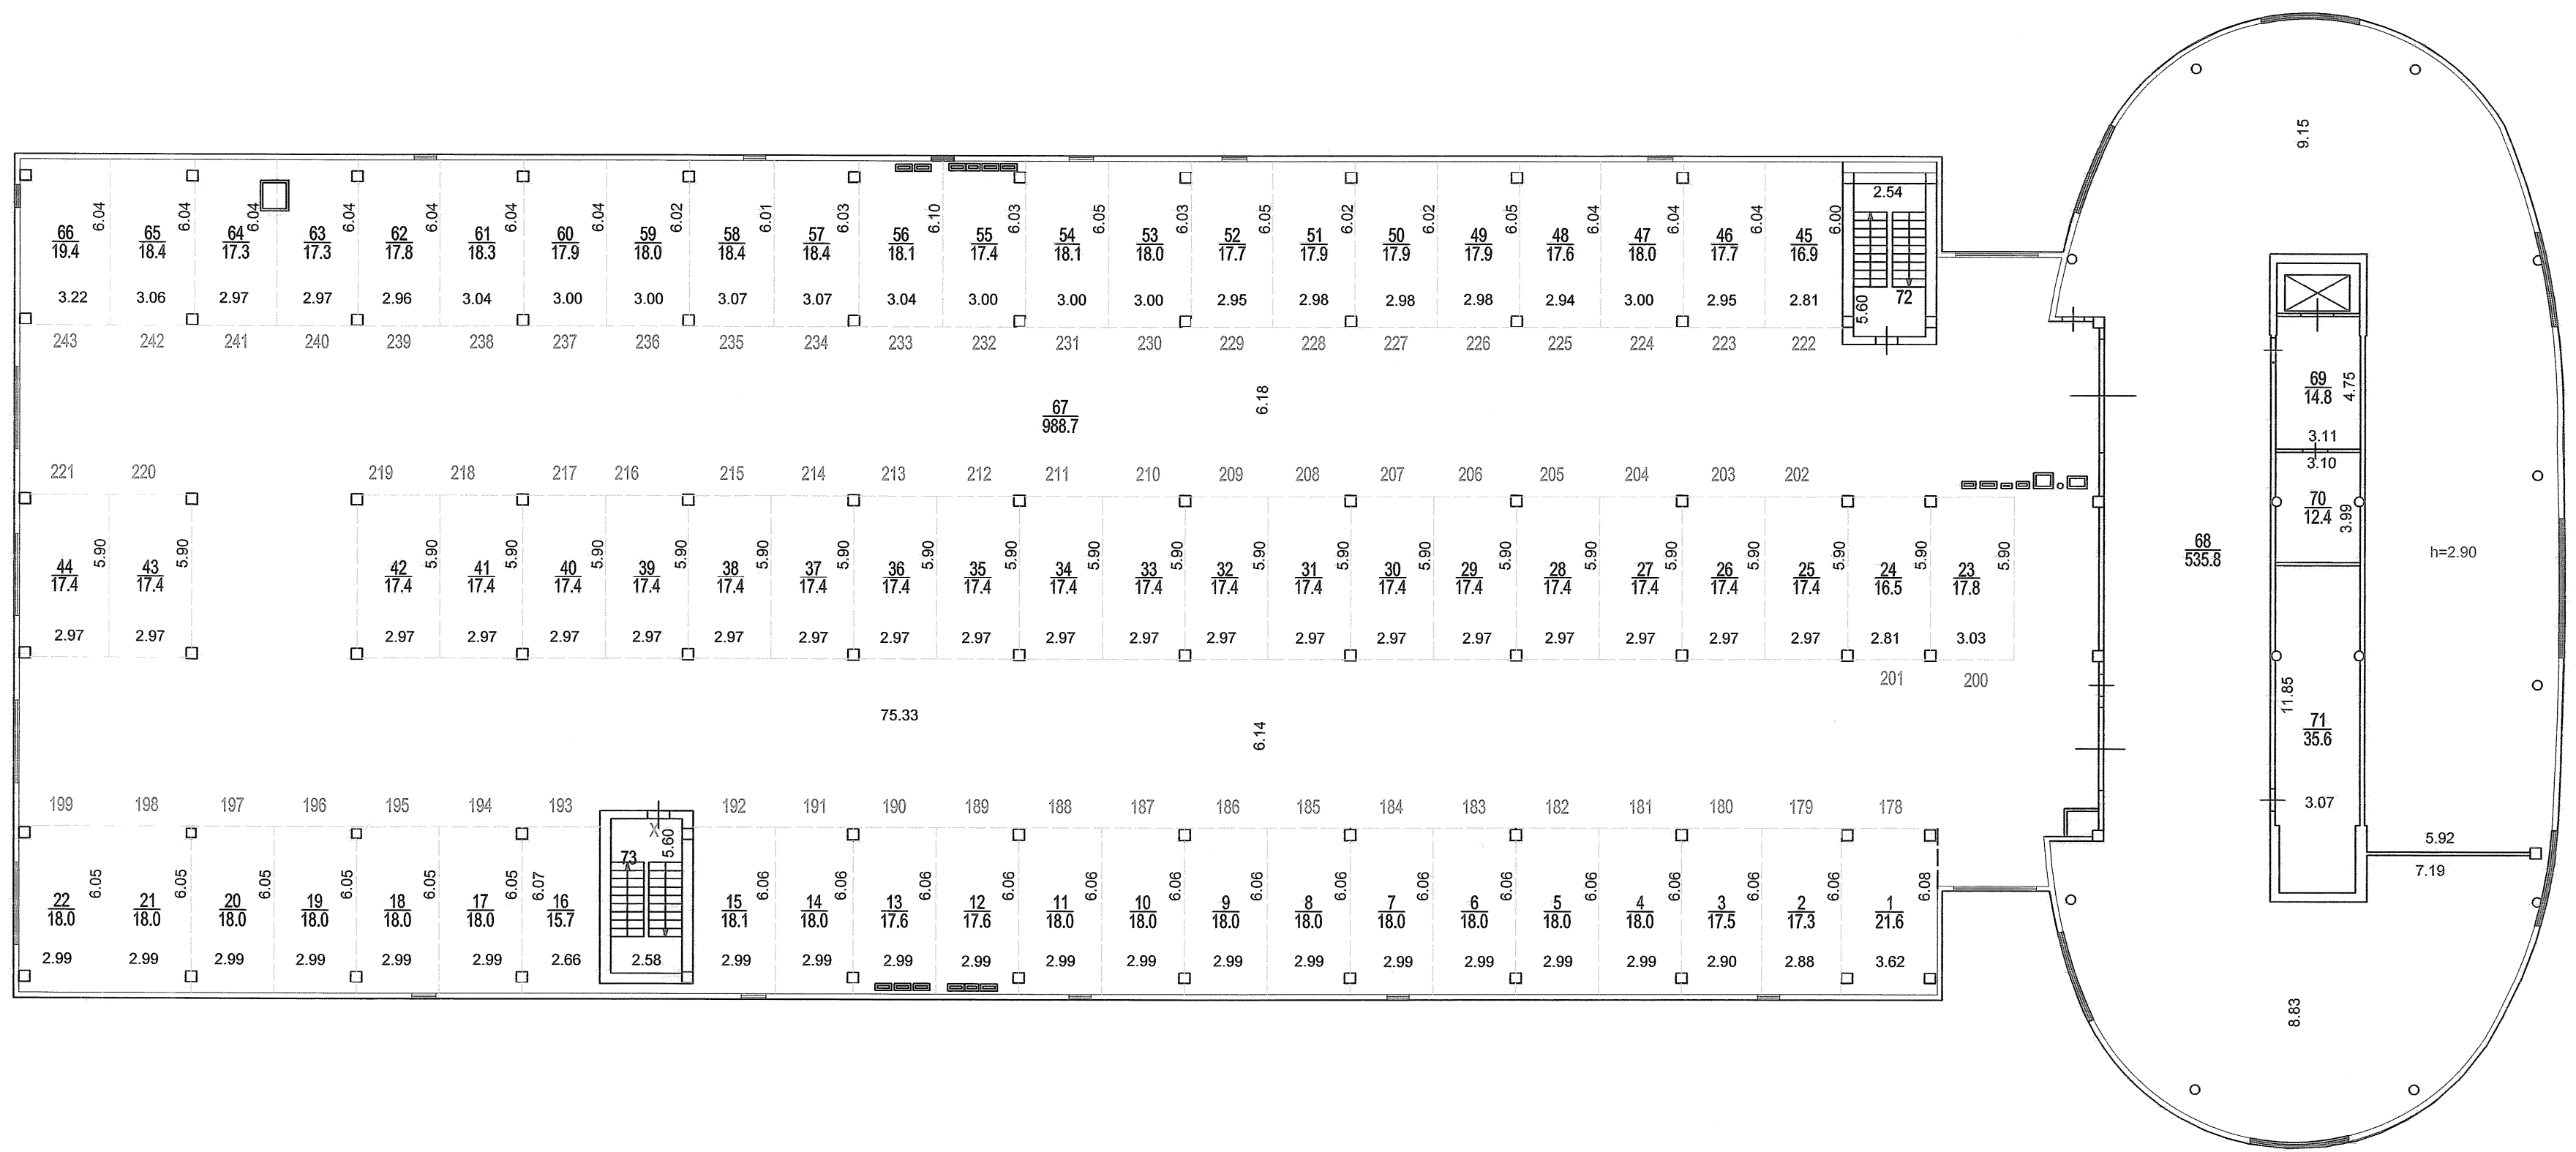

Северо-Восточное
территориальное бюро
технической инвентаризации
города Москвы

Позажный план составлен по состоянию на
"24" 11 2009 г.
П/план снял
Проверил
"04" 03 2014 г.

Масштаб 1:200