



Федеральное государственное унитарное предприятие

«Российский государственный центр инвентаризации и учета объектов недвижимости -

Федеральное БТИ»

(полное наименование ОТИ - организации технического учета и технической инвентаризации объектов капитального строительства)

Ейское городское отделение филиала ФГУП "Ростехинвентаризация - Федеральное БТИ" по

Краснодарскому краю

(наименование обособленного подразделения ОТИ)

ТЕХНИЧЕСКИЙ ПАСПОРТ

На

здание

(вид объекта учета)

Складской корпус. 5 этап строительства

(наименование объекта учета)

Адрес (местоположение) объекта учета:

Субъект Российской Федерации	Краснодарский край	
Район	Ейский	
Муниципальное образование	тип	Городское поселение
	наименование	Ейское
Населенный пункт	тип	город
	наименование	Ейск
Улица (проспект, переулок и т.д.)	тип	улица
	наименование	Щорса
Номер дома	53/4	
Номер корпуса		
Номер строения		
Литера	Е	
Иное описание местоположения		

Инв. №4123

Штамп органа государственного технического учета о внесении сведений
в Единый государственный реестр объектов капитального строительства (ЕГРОКС)

Наименование учетного органа	
Инвентарный номер	
Кадастровый номер	
Дата внесения сведений в ЕГРОКС	

Паспорт составлен по состоянию на «

20 19 года

Руководитель (уполномоченное лицо) О

Мокшина И.Б.

(Фамилия И.О.)

М.П.



I. РЕГИСТРАЦИЯ ПРАВА СОБСТВЕННОСТИ

[illegible]


II. ЭКСПЛИКАЦИЯ ЗЕМЕЛЬНОГО УЧАСТКА - КВ. М

Площадь участка			Незастроенная площадь					
по документа м	фактически	застроен- ная	замощен- ная	озеленен- ная	прочая	грунт		
20000	20000	4381.6	-	-	-	-		

II. Благоустройство полезной площади (кв. м)

[illegible]

СИТУАЦИОННЫЙ ПЛАН

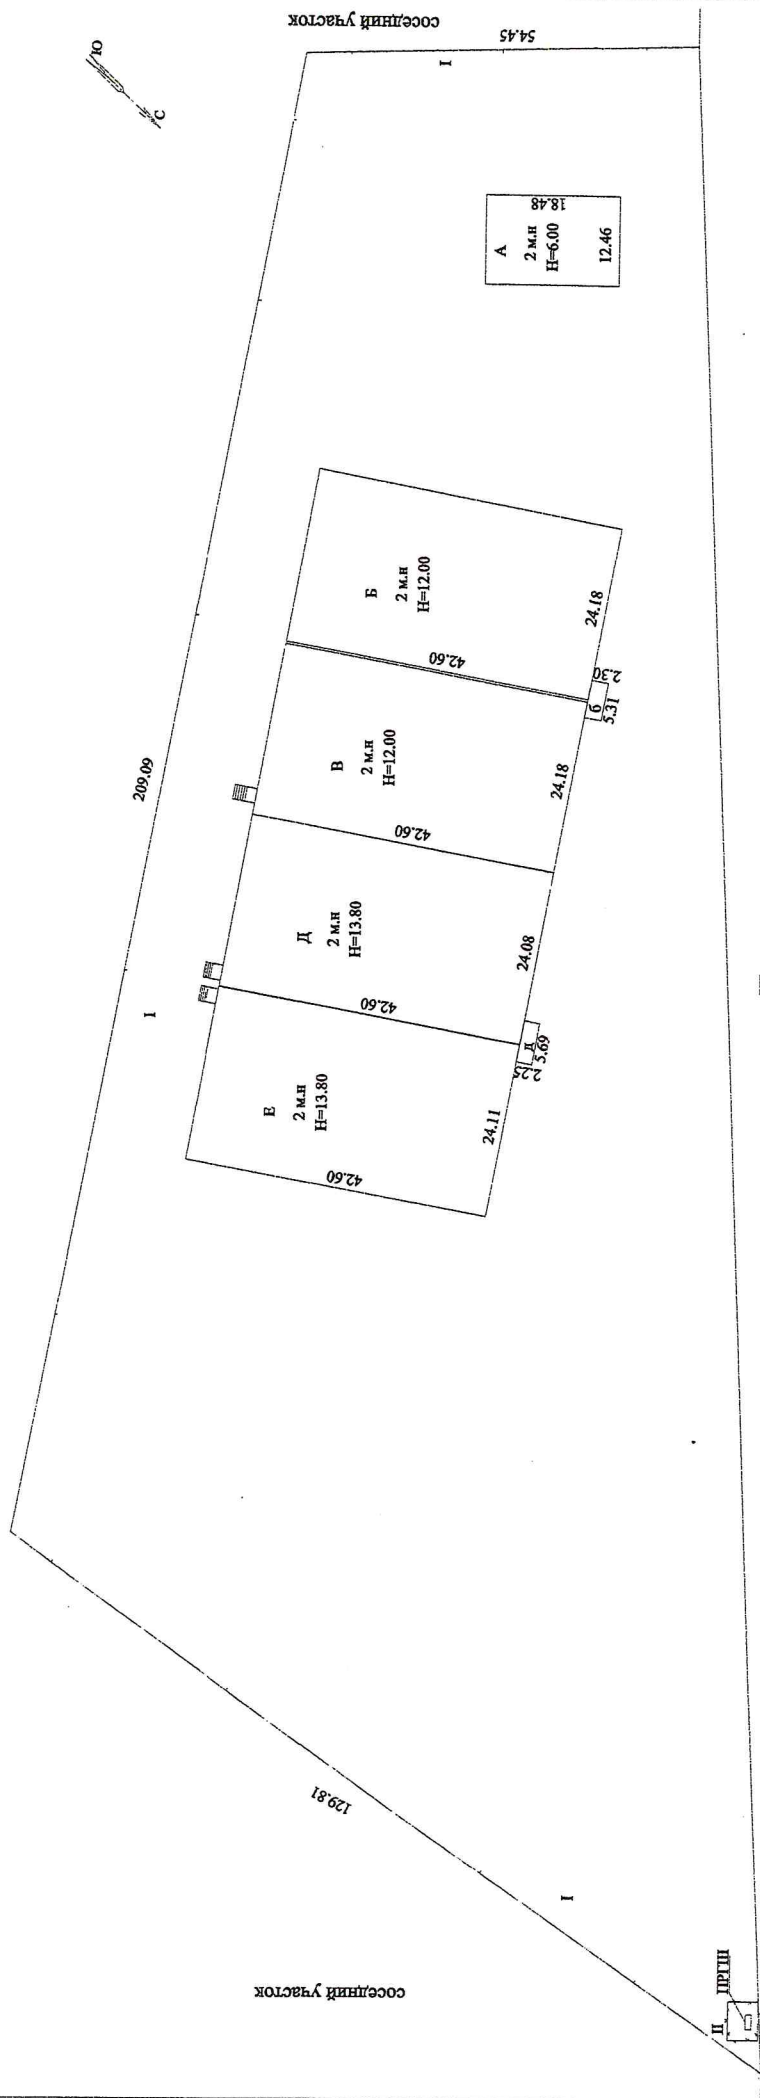

ул. Щорса, 53/4



Производственный участок "Бисит" Южного филиала АО "Гостехинвентаризация" Федеральное РТИ				Лист	1
Начальник отделения: 01.03.2019г.	Мокшина И.Б.	Краснодарский край г. Ейск, ул. Щорса, 53/4	Листов	1	
Проверил: 01.03.2019г.	Мокшина И.Б.	Ситуационный план	Масштаб	1:1000	
Исполнитель: 01.03.2019г.	Бутенко А.В.				

IV. Общие сведения

Назначение	Нежилое
Использование	по назначению
Количество (мощность)	1151.7 м2


Примечание:

Площадь здания в пределах внутренних поверхностей наружных стен-1162,4м2

V. Исчисление площадей и объемов зданий и его частей (подвалов, полуподвалов и пристроек)


[illegible]

Постажный план
1 этаж

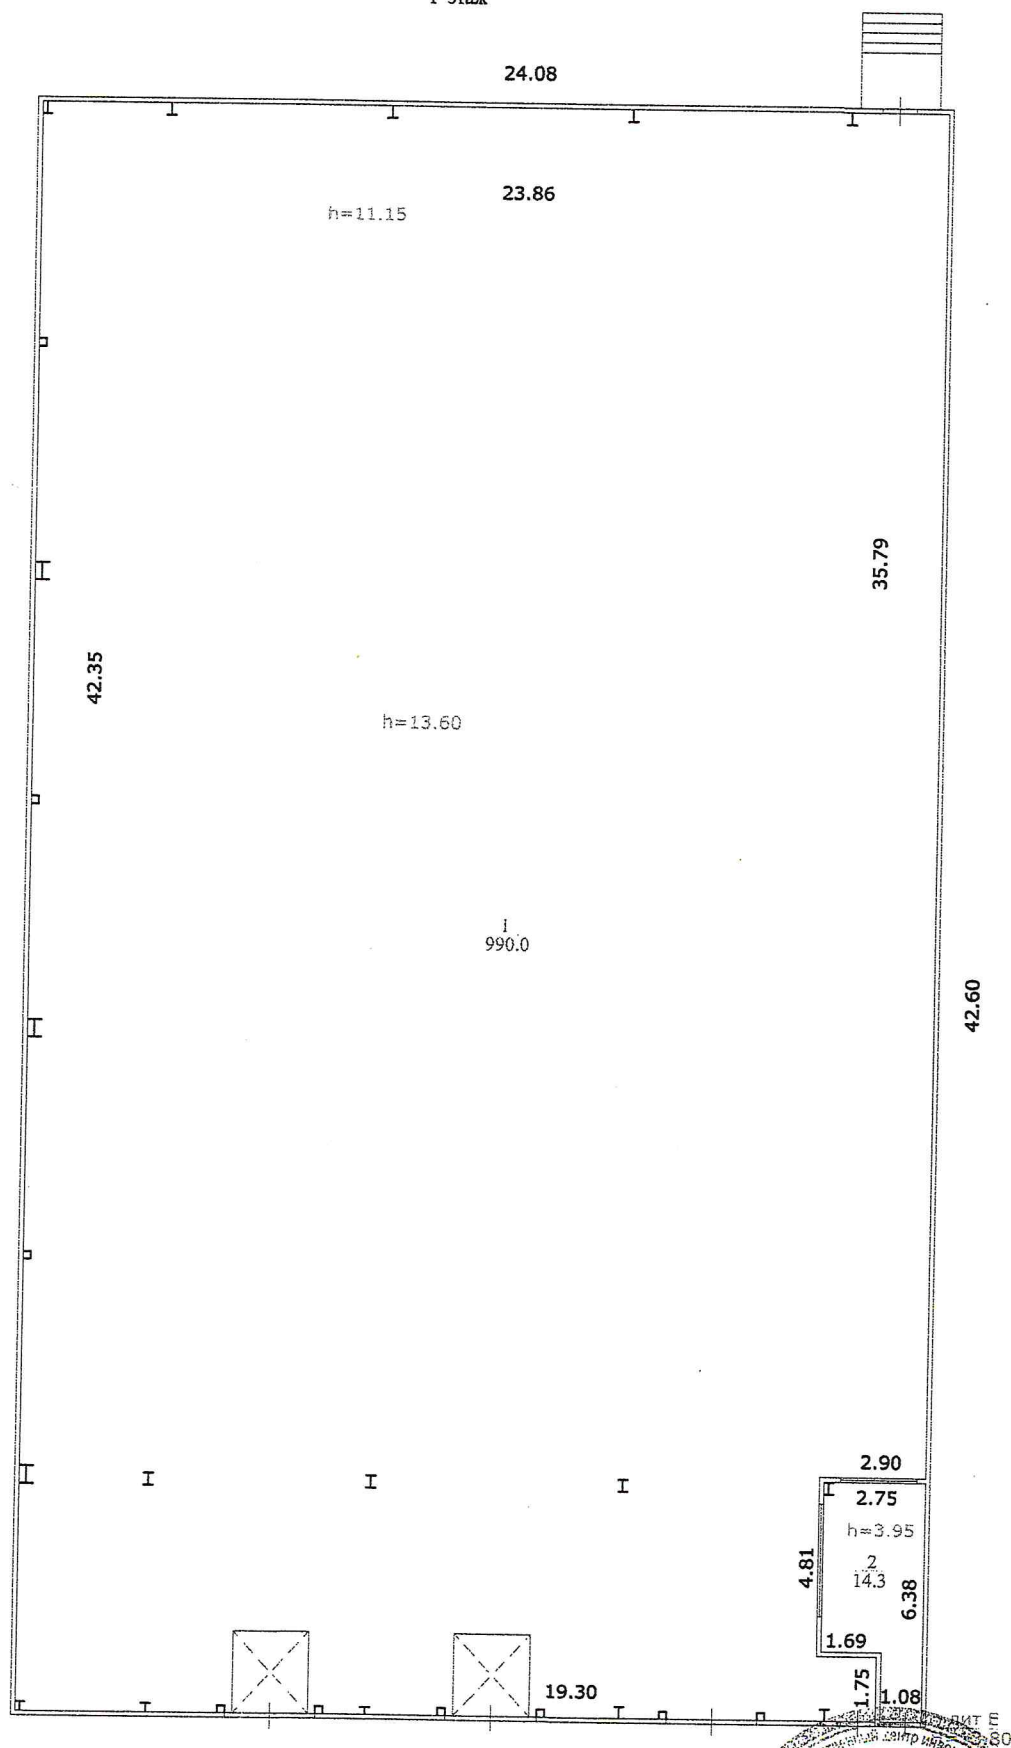

Производственный участок "Ейский"			
Южного филиала АО "Ростехинвентаризация" - Федеральное БТИ			
Начальник отделения:	01.03.2019 г.	Мокшина И.Б.	Постажный план 1-1 этаж
Проверил:	01.03.2019 г.	Мокшина И.Б.	г. Ейск
Исполнитель:	01.03.2019 г.	Бутенко А.В.	Лист 1
			Листов 2
			Масштаб 1:200

Постажный план
2 этаж

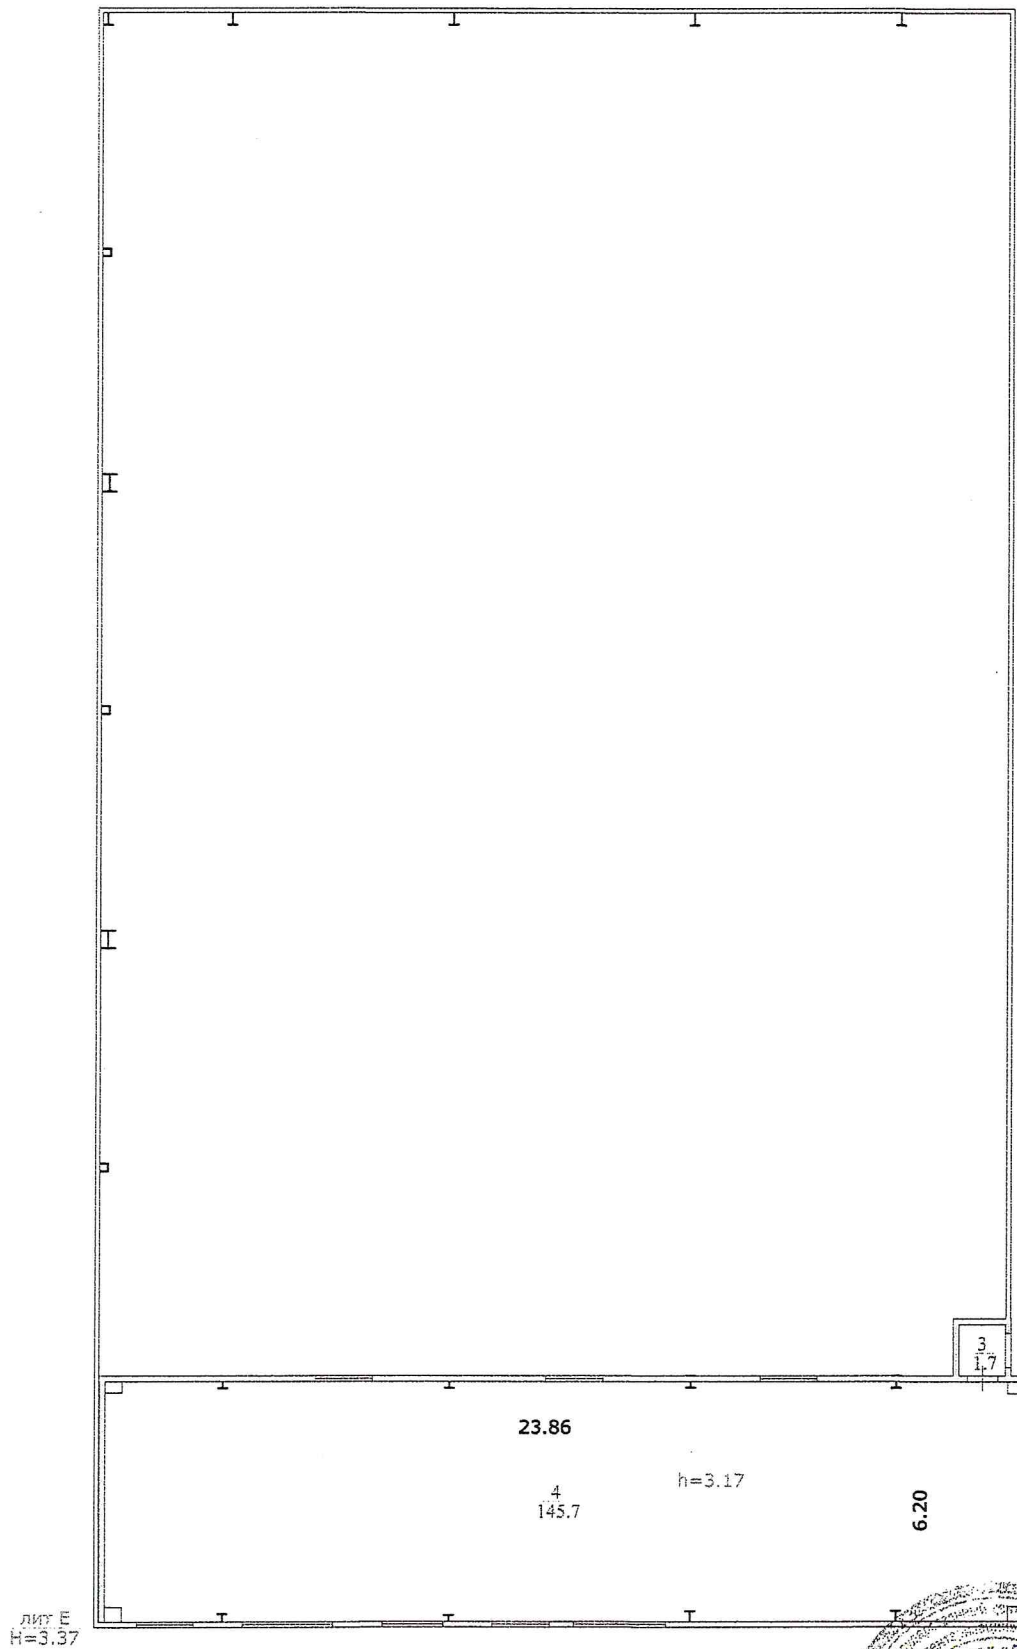

Производственный участок "Байский"			
Южного филиала АО "Ростехинвестаризация - Федеральное БТИ"			
Начальник отделения: 01.03.2019 г	Мокшина И.Б.		Постажный план лит Б-2 этаж
Проверил: 01.03.2019 г	Мокшина И.Б.		г. Бийск
Исполнитель: 01.03.2019 г	Бутенко А.В.		ул. Щорса, 53/4
		Лист	2
		Листов	2
		Масштаб	1:200

На нежилые и жилые строения, имеющие встроенные нежилые помещения

Экспликация № 1

К поэтажному плану строения, расположенного в городе (поселке) г. Ейск по ул.(пер.) ул. Щорса д. 53/4

Литера по плану	Этажи (начиная с 1-го этажа и кончая мезонином)	Номер помещения(квартиры, торгового, складского и т.п.)	Номер по плану строения	Назначение частей помещений: жилая комната, канцелярское помещение, классная комната, кухня, коридор и т.п.	Формула подсчета площади по внутреннему обмеру	Площадь по внутреннему обмеру в кв.м., в том числе предназначенная под помещения						Итого по квартире, этажу, строению	Высота помещений по внутреннему обмеру
						Нежилая							
						основная	вспомогательная	основная	вспомогательная	основная	вспомогательная		
E	1	.	1	Склад		990.0						990.0	13.60
			2	подсобное помещение			14.3					14.3	3.95
					Итого по помещению по : 1-му этажу	990.0	14.3					1004.3	
E	2		3	Тамбур			1.7					1.7	3.17
			4	Нежилое помещение			145.7					145.7	3.17
					Итого по помещению по : 2-му этажу		147.4					147.4	
					Итого по помещению :	990.0	161.7					1151.7	
					Итого по этажам: 1, 2	990.0	161.7					1151.7	
					Итого по зданию	990.0	161.7					1151.7	
					Площадь здания в пределах внутренних поверхностей наружных стен	1162.4							

VI. Описание конструктивных элементов здания и определение износа

Литера Е Год постройки 2019 Число этажей 2
 Группа капитальности _____ Вид внутренней отделки _____

№№ п.п.	Наименование конструктивных элементов	Описание конструктив- ных элементов (материал, конструкция, отделка и пр.)	Техническое со- стояние (осадки, трещины, гниль и т.п.)	Удельный вес по таблице	Поправка к уд. весу в %	Удельный вес конст. элем. с поправкой	Износ %	Процент изно- са к строению	Тек. изм.	
1	2	3	4	5	6	7	8	9	10	11
1	Фундамент	бетонно-ленточный					0			
2	а. Стены и их наружная отделка	металлическая конструкция, сэндвич панели					0			
	б. Перегородки	кирпичные					0			
3	Перекрытия	чердачные	металлоконструкция							
		междуэтажные					0			
		подвальные								
4	Крыша	сэндвич панель кровельная					0			
5	Полы	бетонная стяжка					0			
6	Проемы	Оконные	металлопластиковые							
		Дверные	металлические, металлопластиковые, ролетные ворота				0			
7	Внутренняя отделка						0			
8	Сан. и электротех. устройства	отопление	АГВ и др.							
		водопровод	центральный							
		канализация	местная							
		электроосвещение	да							
		радио								
		телефон								
		телевидение								
		ванны								
		горячее водоснабжение								
		лифты								
9	Разные работы						0			
Итого				100	х		х			

% износа, приведенный к 100 по формуле: $\frac{\text{процент износа (гр. 9)} \times 100}{\text{удельный вес (гр. 7)}} =$

XI. Техническое описание служебных пристроек

Наименование конструктивных элементов	Ступени	Удельный вес по таблице	Ценностный коэффициент	Уд. вес после применения		Удельный вес по таблице	Ценностный коэффициент	Уд. вес после применения		Удельный вес по таблице	Ценностный коэффициент	Уд. вес после применения
	литера .е								литера _			
Фундамент												
Стены и перегородки	бетонны е											
Перекрытия												
Крыша												
Полы												
Проемы												
Отделочные работы												
Электроосвещение												
Прочие работы												
	Итого	100	X	0	Итого	100	X	0	Итого	100	X	

Наименование конструктивных элементов	литера	Удельный вес по таблице	Ценностный коэффициент	Уд. вес после применения	литера	Удельный вес по таблице	Ценностный коэффициент	Уд. вес после применения	литера	Удельный вес по таблице	Ценностный коэффициент	Уд. вес после применения
	—				—				—			
Фундамент												
Стены и перегородки												
Перекрытия												
Крыша												
Полы												
Проемы												
Отделочные работы												
Электроосвещение												
Прочие работы												
	Итого	100	X		Итого	100	X		Итого	100	X	

ХII. Исчисление стоимости служебных пристроек

[illegible]

ХIII. Ограждения и сооружения (замошения) на участке

Литера	Наименование ограждения	Материал и конструкция	Размеры		Площадь кв. м.	№ сборника	№ таблицы	Измеритель	Стоимость измерителя по таблице	Поправка на климат. район	Восстановит. стоим. в руб.	% износа	Действит. стоим. в руб.
			Длина м	Ширина высота м									

ХIII. Общая стоимость, руб.

В ценах какого года	Основные строения		Служебные строения		Сооружения		Всего	
	восстано- вительная	действи- тельная	восстано- вительная	действи- тельная	восстано- вительная	действи- тельная	восстано- вительная	действи- тельная

" 1 " марта 20 19 г.

" " 20 г.

" " 20 г.

Исполнил Бутенко А. В.

Проверил Мокшина И. Б.

Начальник бюро Мокшина И. Б.

ХV. Отметка о последующих обследованиях

Работа выполнена	" " 200 г.	" " 200 г.	" " 200 г.
Обследовал			
Проверил			
Руководитель			