



2 ЭТАЖ

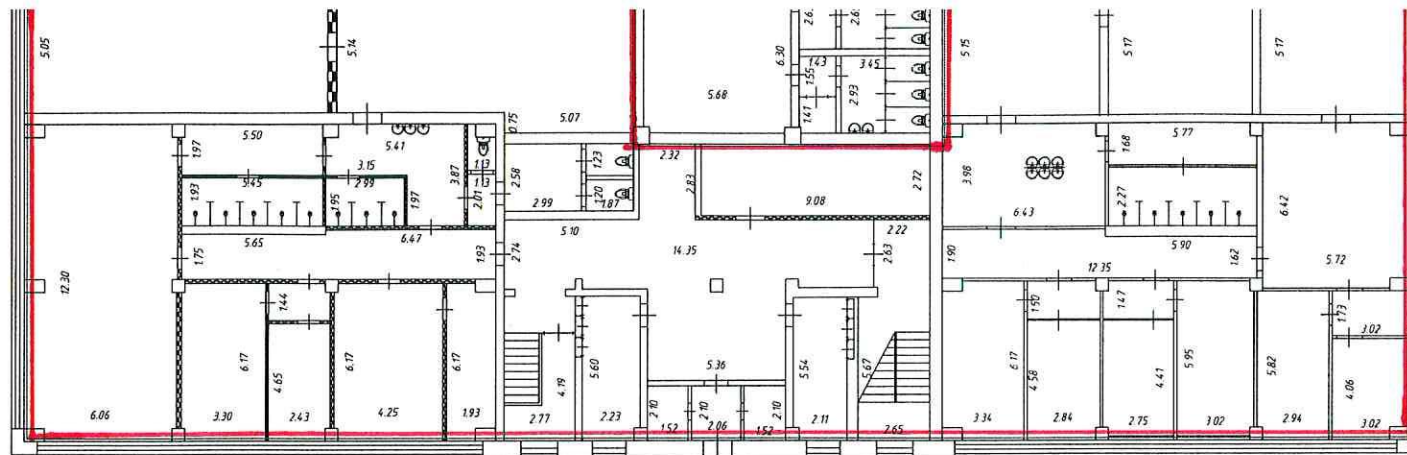

Помещение 2

Антресоль

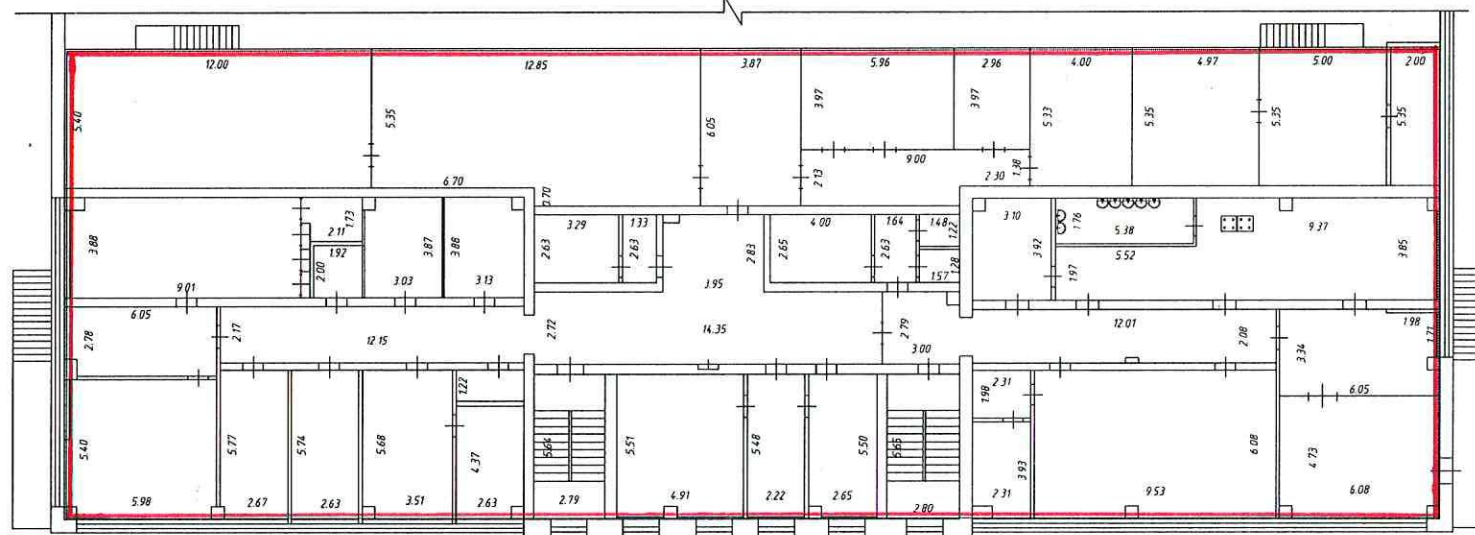



Условные обозначения:
Часть границы геометрической фигуры:

- граница вновь образованного помещения
- стена
- стена с окном и дверью
- перегородка
- лестница
- дверь остекленная (на балкон лоджия)
- колонна
- лифт

Масштаб 1:200

Площадь помещения - 1700,6 кв м

1 ЭТАЖ

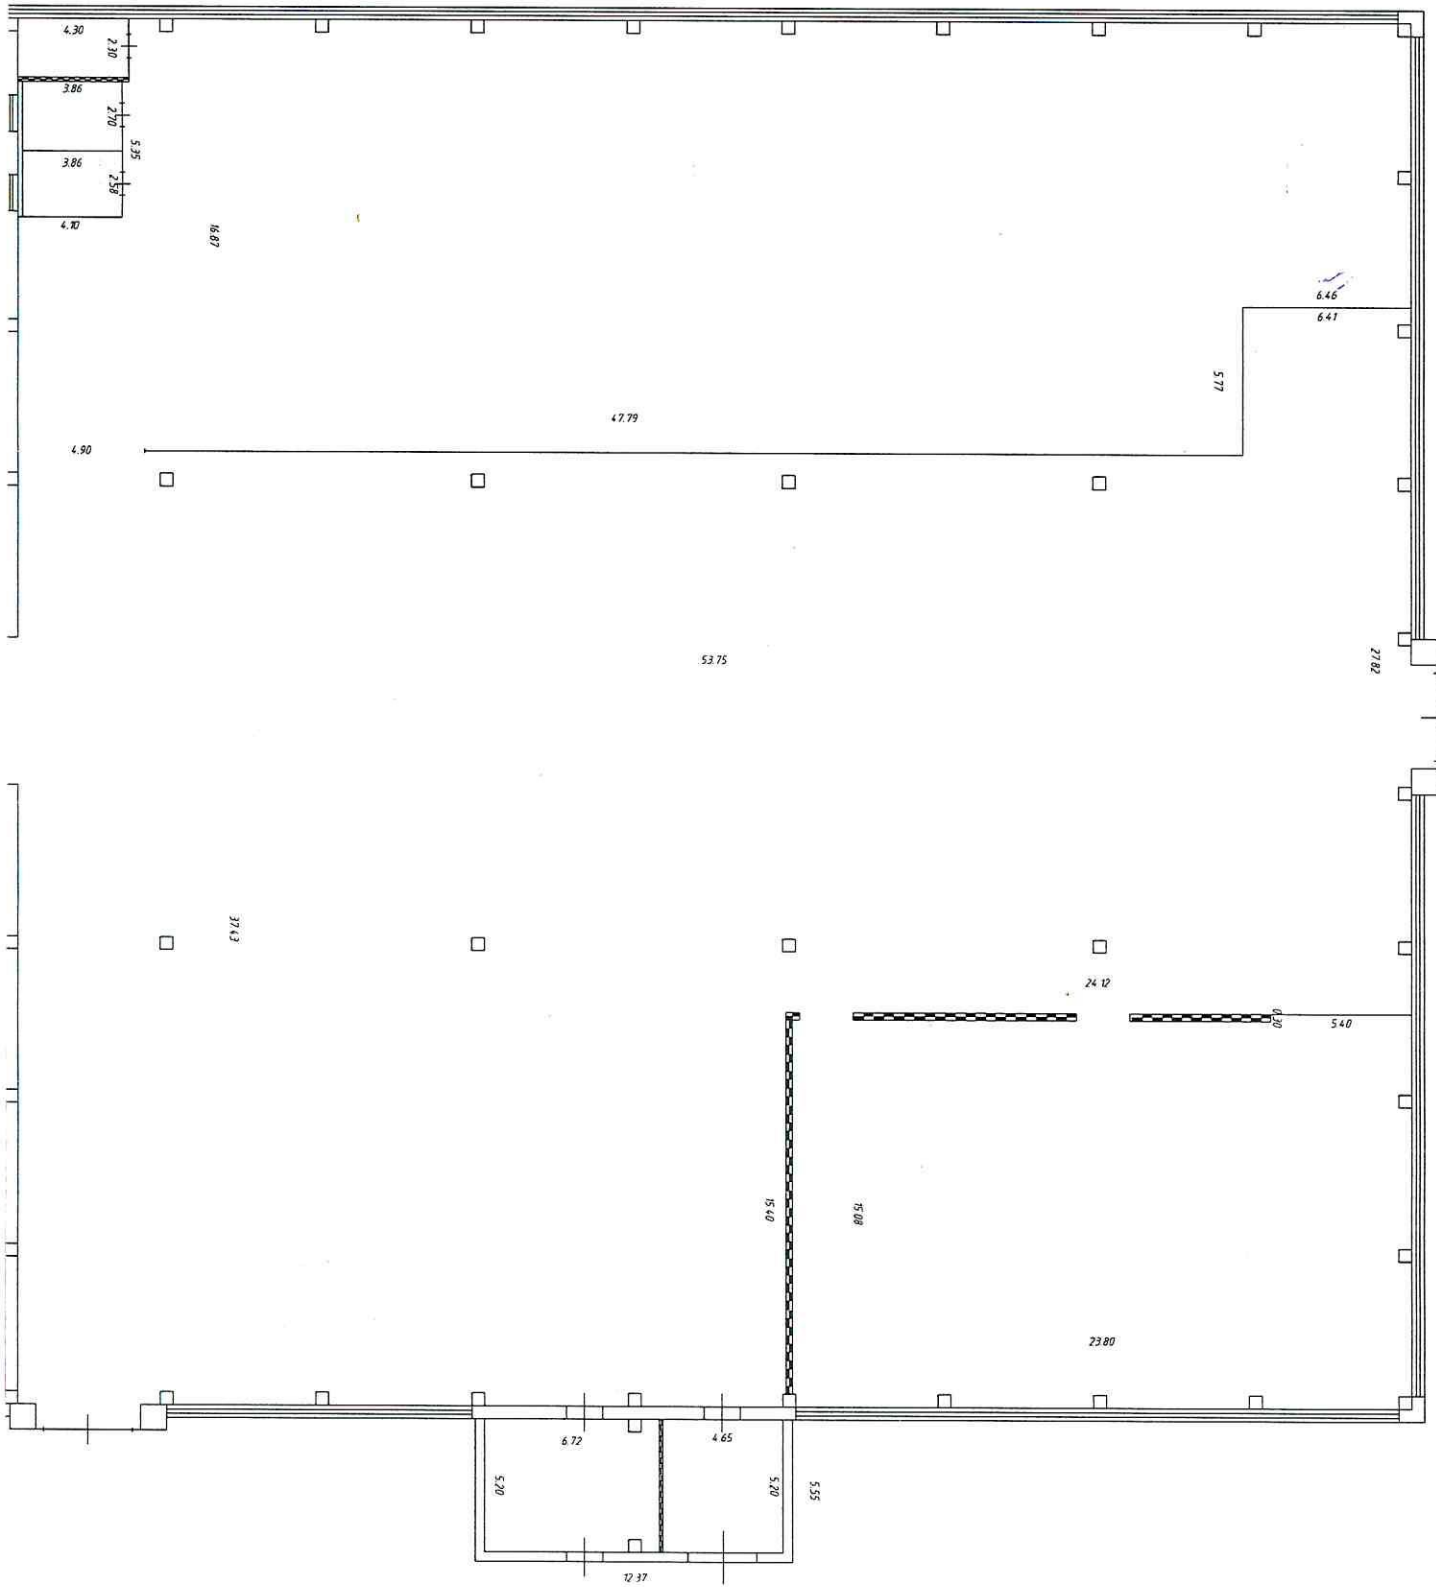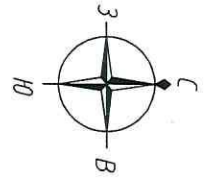

План этажа
1 этаж